

ООО ПСК «СЕРВИС»

Заказчик: ИП

**«Проект реконструкции административного здания
по адресу:
Российская Федерация, Московская область, Люберецкий р-н,
рп Малаховка, ул Чайковского, д1»**

Проектная документация.

Архитектурные решения

Том 3

П-29/0824-АР

2024 г.

ООО ПСК «СЕРВИС»

Заказчик: ИП

**«Проект реконструкции административного здания
по адресу:
Российская Федерация, Московская область, Люберецкий р-н,
рп Малаховка, ул Чайковского, д1»**

Проектная документация.

Архитектурные решения

П-29/0824-АР

Том 3

Генеральный директор

Главный инженер проекта

2024 г.

Содержание тома

Обозначение	Наименование	Примечание (стр.)
1	2	3
1.	Внешний и внутренний вид объекта. Пространственная, планировочная и функциональная организация.	4
2.	Обоснование принятых объёмно-пространственных и архитектурно-художественных решений, в том числе в части соблюдения предельных параметров разрешенного строительства объекта капитального строительства.	7
3.	Описание и обоснование использованных композиционных приемов при оформлении фасадов и интерьеров объекта капитального строительства.	7
4.	Описание решений по отделке помещений основного, вспомогательного, обслуживающего и технического назначения.	8
5.	Архитектурные решения, обеспечивающие естественное освещение помещений с постоянным пребыванием людей.	8
6.	Архитектурно-строительные мероприятия, обеспечивающие защиту помещений от шума, вибрации и другого воздействия.	8
7	Перечень мероприятий по обеспечению соблюдения установленных требований энергетической эффективности к конструктивным решениям, влияющим на энергетическую эффективность зданий, строений и сооружений.	9
8.	Перечень графических материалов.	10
9.	Приложения.	10

Настоящий проект разработан в соответствии с действующими Государственными нормами, стандартами, исходными данными, а так же техническими условиями и требованиями, выданными органами государственного надзора и заинтересованными организациями при согласовании места размещения объекта.

ГИП Е. С

									Лист
									3
Изм.	Лист	№ докум.	Подпись	Дата					

П - 29/0824-AP

Основные технико-экономические показатели

1. Площадь застройки _____ 757,0 м²
2. Строительный объём _____ 8277,0 м³
3. Площадь здания до реконструкции _____ 903,8 м²
4. Общая площадь здания после реконструкции _____ 1843,1
5. Пристраиваемая площадь здания _____ 939,3 м²
6. Площадь помещений после реконструкции _____ 1665,2 м²
7. Высота здания _____ 13,54 м
8. Этажность _____ 3х этажное
9. Количество этажей _____ 4(подвал, 1й этаж, 2й этаж, мансарда)
10. Высота подвала _____ 2,34-3,3 м
11. Высота 1-го этажа _____ 3,63 м
12. Высота 2-го этажа _____ 3,63-4,17 м
13. Высота мансарды _____ 1,96-4,2 м

1. Внешний и внутренний вид объекта. Пространственная, планировочная и функциональная организация.

Настоящий проект: «Проект реконструкции административного здания» расположенный по адресу: Российская Федерация, Московская область, Люберецкий р-н, рп Малаховка, ул Чайковского, д1 выполнен на основании задания на проектирование. Здание представляет собой в плане прямоугольную форму.

За условную отметку 0,000 принят уровень чистого пола первого этажа.

Подземные воды в период изысканий не вскрыты .

Здание запроектировано на площадке со следующими природно-климатическими показателями:

Климат района работ умеренно-континентальный и, согласно СНиП 23-01-99, СНиП 2.01.07.-85* характеризуется следующими основными показателями:- средняя годовая температура воздуха - плюс 4.1° С;
- абсолютный минимум - минус 43° С;
- абсолютный максимум - плюс 38° С;
- количество осадков за год - 644 мм.

Направление ветра:

- зимой –западное, максимальное из средних скоростей ветра по румбам 2,0 м/с; - летом -западное, минимальное из средних скоростей ветра по румбам за июль 0 м/с.

-сейсмичность района строительства (по СНиП II-7-81 и ОСР-97)-6 баллов.

Конструктивная схема проектируемого здания.

Класс ответственности сооружения – II

Степень огнестойкости здания – III

					П - 29/0824-АР	Лист
						4
Изм.	Лист	№ докум.	Подпись	Дата		

Снеговой район по СП 20.13330.2016 - 3. Расчетное значение веса снегового покрова S_q на 1м горизонтальной поверхности земли 210 кгс/м²

Класс конструктивной пожарной опасности – С1;

Класс функциональной пожарной опасности– Ф 3.4;

Архитектурно- художественные решения разработаны исходя из требований и параметров технологического процесса, санитарно-гигиенических и противопожарных норм проектирования, а также техническим заданием на проектирование и с учётом комфортного пребывания персонала на рабочем месте.

Проектируемое здание трёхэтажное с подвалом(подземный)- подвал, первый и второй этаж, мансарда. Здание имеет размеры в осях 33.590 м х 25.49 м. Общая площадь подвала- 168,5м.кв. Общая площадь первого этажа- 567,5м.кв. Общая площадь второго этажа-570,5 м.кв. Общая площадь мансарды-536,6 м.кв. Высота здания 13.54 м., от уровня ближайшего проезда у здания. Кровля- много скатная, не эксплуатируемая.

В здании предусмотрены конструктивные и объемно-планировочные решения, обеспечивающие в случае пожара:

- возможность эвакуации людей независимо от их возраста и физического состояния наружу на прилегающую к зданию территорию до наступления угрозы их жизни и здоровью вследствие воздействия опасных факторов пожара;
- возможность спасения людей;
- возможность доступа личного состава пожарных подразделений и подачи средств пожаротушения к очагу пожара, а также проведения мероприятий по спасению людей и материальных ценностей;
- нераспространение пожара на рядом расположенные здания, в том числе при обрушении горящего здания;
- ограничивающие площадь возможного пожара и препятствующие распространению опасных факторов пожара по помещениям и между отсеками и этажами;
- ограничение пожарной опасности строительных материалов;
- ограничение прямого и косвенного материального ущерба, включая содержимое здания и само здание, при экономически обоснованном соотношении величины ущерба и расходов на противопожарные мероприятия, пожарную охрану и ее техническое оснащение.

В соответствии с требований строительных норм СНиП 21-01-97* "Пожарная безопасность зданий и сооружений", СНиП 31-06-2009 "Общественные здания", СНиП 31-05-2003 "Общественные здания административного назначения", МДС 21-1.98 "Предотвращение распространения пожара" (Пособие к СНиП 21-01-97 "Пожарная

					П - 29/0824-AP	Лист
						5
Изм.	Лист	№ докум.	Подпись	Дата		

безопасность зданий и сооружений"), с учетом этажности (высоты) и площади этажей пожарных отсеков, здание запроектировано IV - ой степени огнестойкости.

Двери эвакуационных выходов из здания открываются по направлению выхода.

Ширина эвакуационных путей предусмотрена такой, чтобы с учетом их геометрии по ним можно беспрепятственно пронести носилки с лежащим на них человеком.

Двери открываются по ходу эвакуации и не имеют запоров, препятствующих открыванию дверей изнутри без ключа. Двери лестничных клеток при открывании не уменьшают ширины маршей и площадок, имеют устройства для само закрывания и уплотнения в притворах.

Допустимая высота здания и площадь этажа в пределах пожарного отсека соответствует степени огнестойкости и класса конструктивной пожарной опасности здания.

В проектируемом здании для обеспечения требуемого предела огнестойкости несущих элементов применена только конструктивная огнезащита.

Внутренние стены здания на путях будут отделаны негорючими материалами после ввода здания в эксплуатацию.

Принимаемые в проекте узлы пересечения кабелями и трубопроводами ограждающих конструкций с нормируемой огнестойкостью и пожарной опасностью не снижают требуемых пожарно-технических показателей конструкции. Заделка зазоров и отверстий в местах прокладки коммуникаций предусмотрена негорючими материалами.

Ограждение кровли h-1,2м

Проектом предусмотрен подъезд пожарной и спец техники.

Металлические конструкции должны быть окрашены эмалью ПФ-115 ГОСТ 6465-76*за 2 раза по слою грунтовки ГФ -021 ГОСТ 25129-82

Конструктивная схема здания– стеновая

Наружные стены –из кирпича

Внутренние стены и перегородки - кирпич и пенобетонных блоки;

Фундамент – монолитный, ленточный.

Перекрытия между этажами - монолитное железобетонное.

Крыша – много скатная по деревянной стропильной конструкции

Кровля - металлочерепица.

Водосток - наружный.

					П - 29/0824-AP	Лист
						6
Изм.	Лист	№ докум.	Подпись	Дата		

2. Обоснование принятых объёмно-пространственных и архитектурно-художественных решений, в том числе в части соблюдения предельных параметров разрешенного строительства объекта капитального строительства.

Восприятием архитектурного объекта является ощущение объёмно-пространственного построения. Созданию зрительного образа способствует гармония соотношений его объёмов, плоскостей и проёмов, и сочетание таких архитектурных средств, как художественный контраст, игра теней на поверхности фасада, пропорциональный строй его архитектурных элементов, а также цвет.

Практическая целесообразность является существенной предпосылкой привлекательности архитектуры.

3. Описание и обоснование использованных композиционных приемов при оформлении фасадов и интерьеров объекта капитального строительства.

Цветовая схема выполнена в корпоративных цветах.

Конструктивная схема –стеновая .

Фундаменты- монолитные ж/б ленточный.

Перекрытие- ж/б плиты.

Стены оштукатурены – цвет охра

4. Описание решений по отделке помещений основного, вспомогательного, обслуживающего и технического назначения.

Внутренняя отделка помещений будет производиться после ввода здания в эксплуатацию, с учётом требований технологического процесса, норм пожарной безопасности и эстетико-комфортных решений объекта.

5. Архитектурные решения, обеспечивающие естественное освещение помещений с постоянным пребыванием людей.

Естественная освещённость рабочих мест обеспечивается через оконные проёмы в наружных стенах. Естественное освещение не предусматривается в гараже, автомойки, санузлах.

В местах недостаточной освещённости предусматривается дополнительное искусственное освещение.

					П - 29/0824-AP	Лист
						7
Изм.	Лист	№ докум.	Подпись	Дата		

Суммарная продолжительность инсоляции самой темной части здания составляет 2 часа. В прочих помещениях обеспечивается непрерывная инсоляция не менее 2,5 часов. Ограничение избыточного теплового воздействия не предусмотрено.

Группа административного района по ресурсам светового климата – 1

Разряд зрительной работы IV

Коэффициент пропускания солнечной радиации окон с твердым селективным покрытием (примененных в проекте) – 0,75

Коэффициент пропускания солнечной радиации окон с обычным остеклением – 0,76

Естественное освещение в помещении является достаточным.

6. Архитектурно-строительные мероприятия, обеспечивающие защиту помещений от шума, вибрации и другого воздействия.

Шумоизоляция – отделение помещений перегородками. Виброизоляция – отделение конструкции пола демпфирующими прокладками от фундаментов технологического оборудования.

В полах здания предусмотрена стяжка цементно-песчаная по звукоизоляционной упругой подложке, что обеспечивает защиту помещений от ударного шума. От воздушного шума защиту помещений обеспечивает диск перекрытия, работающая совместно со стяжкой. Оборудование инженерных помещений устанавливается на пол или фундамент с устройством амортизаторов.

Предусмотрена гидроизоляция полов в мокрых помещениях - Технониколь «Унифлекс ЭПП» в два слоя

Согласно п.1.6 СП 23-103-2003 расчет влияния шума является предварительной оценкой ожидаемого уровня шума. Окончательная оценка звукоизоляции конструкций должна производиться на основании натурных испытаний по ГОСТ 27296-87.

В случае несоответствия результата натурных испытаний расчетному, в проект необходимо внести изменения в части повышения звуковой комфортности.

					П - 29/0824-AP	Лист
						8
Изм.	Лист	№ докум.	Подпись	Дата		

7. Перечень мероприятий по обеспечению соблюдения установленных требований энергетической эффективности к конструктивным решениям, влияющим на энергетическую эффективность зданий, строений и сооружений.

Основными мероприятиями по обеспечению соблюдения установленных требований энергетической эффективности к конструктивным решениям, влияющим на энергетическую эффективность проектируемого здания, являются поэлементные требования нормируемых значений приведенного сопротивления теплопередаче ограждающих конструкций. Базовое значение требуемого сопротивления теплопередаче ограждающей конструкции, принимается в зависимости от градусо-суток отопительного периода региона строительства, и определяется по таблице 3 СП 50.13330.2012.

К ограждающим конструкциям проектируемого здания относятся:

- стены, представленные из кирпича и пенобетонных блоков;
- покрытия из металлочерепицы с минераловатным утеплителем (по мансарде);
- наружные окна и двери.

Примененные конструкции и материалы обеспечивают соблюдение установленных требований энергетической эффективности к конструктивным решениям.

Приведенное сопротивление теплопередачи отдельных элементов зданий превышает нормируемое значение.

8. Перечень графических материалов.

№ п/п	Наименование	Шифр, лист
1	2	3
«Архитектурные решения»		
1	Общие данные	
2.	План Подвал до реконструкции	
3.	План 1-го этажа до реконструкции	
4.	План 2-го этажа до реконструкции.	
5.	План 1-го этажа. Демонтажный план	
6.	План 2-го этажа. Демонтажный план	
7.	План Подвал. Монтажный план	
8.	План 1-го этажа. Монтажный план	
9.	План 2-го этажа. Монтажный план	

					П - 29/0824-AP	Лист
						9
Изм.	Лист	№ докум.	Подпись	Дата		

10	План Мансарды. Монтажный план	
11	План Подвал.	
12	План 1-го этажа.	
13	План 2-го этажа.	
14	План Мансарды.	
15	План кровли.	
16	Разрез 1-1.	
17	Фасад в осях 1-8	
18	Фасад в осях 8-1	
19.	Фасад в осях А-И	
20	Фасад в осях И-А	
21	Цветовое решение. Фасад в осях 1-8	
22	Цветовое решение. Фасад в осях 8-1	
23	Цветовое решение. Фасад в осях А-И	
24	Цветовое решение. Фасад в осях И-А	


9. Приложения.

					П - 29/0824-AP	Лист
						10
Изм.	Лист	№ докум.	Подпись	Дата		

</

ПЛАН ПОДВАЛА ДО РЕКОНСТРУКЦИИ ПО ПЛАНУ БТИ

М 1:100

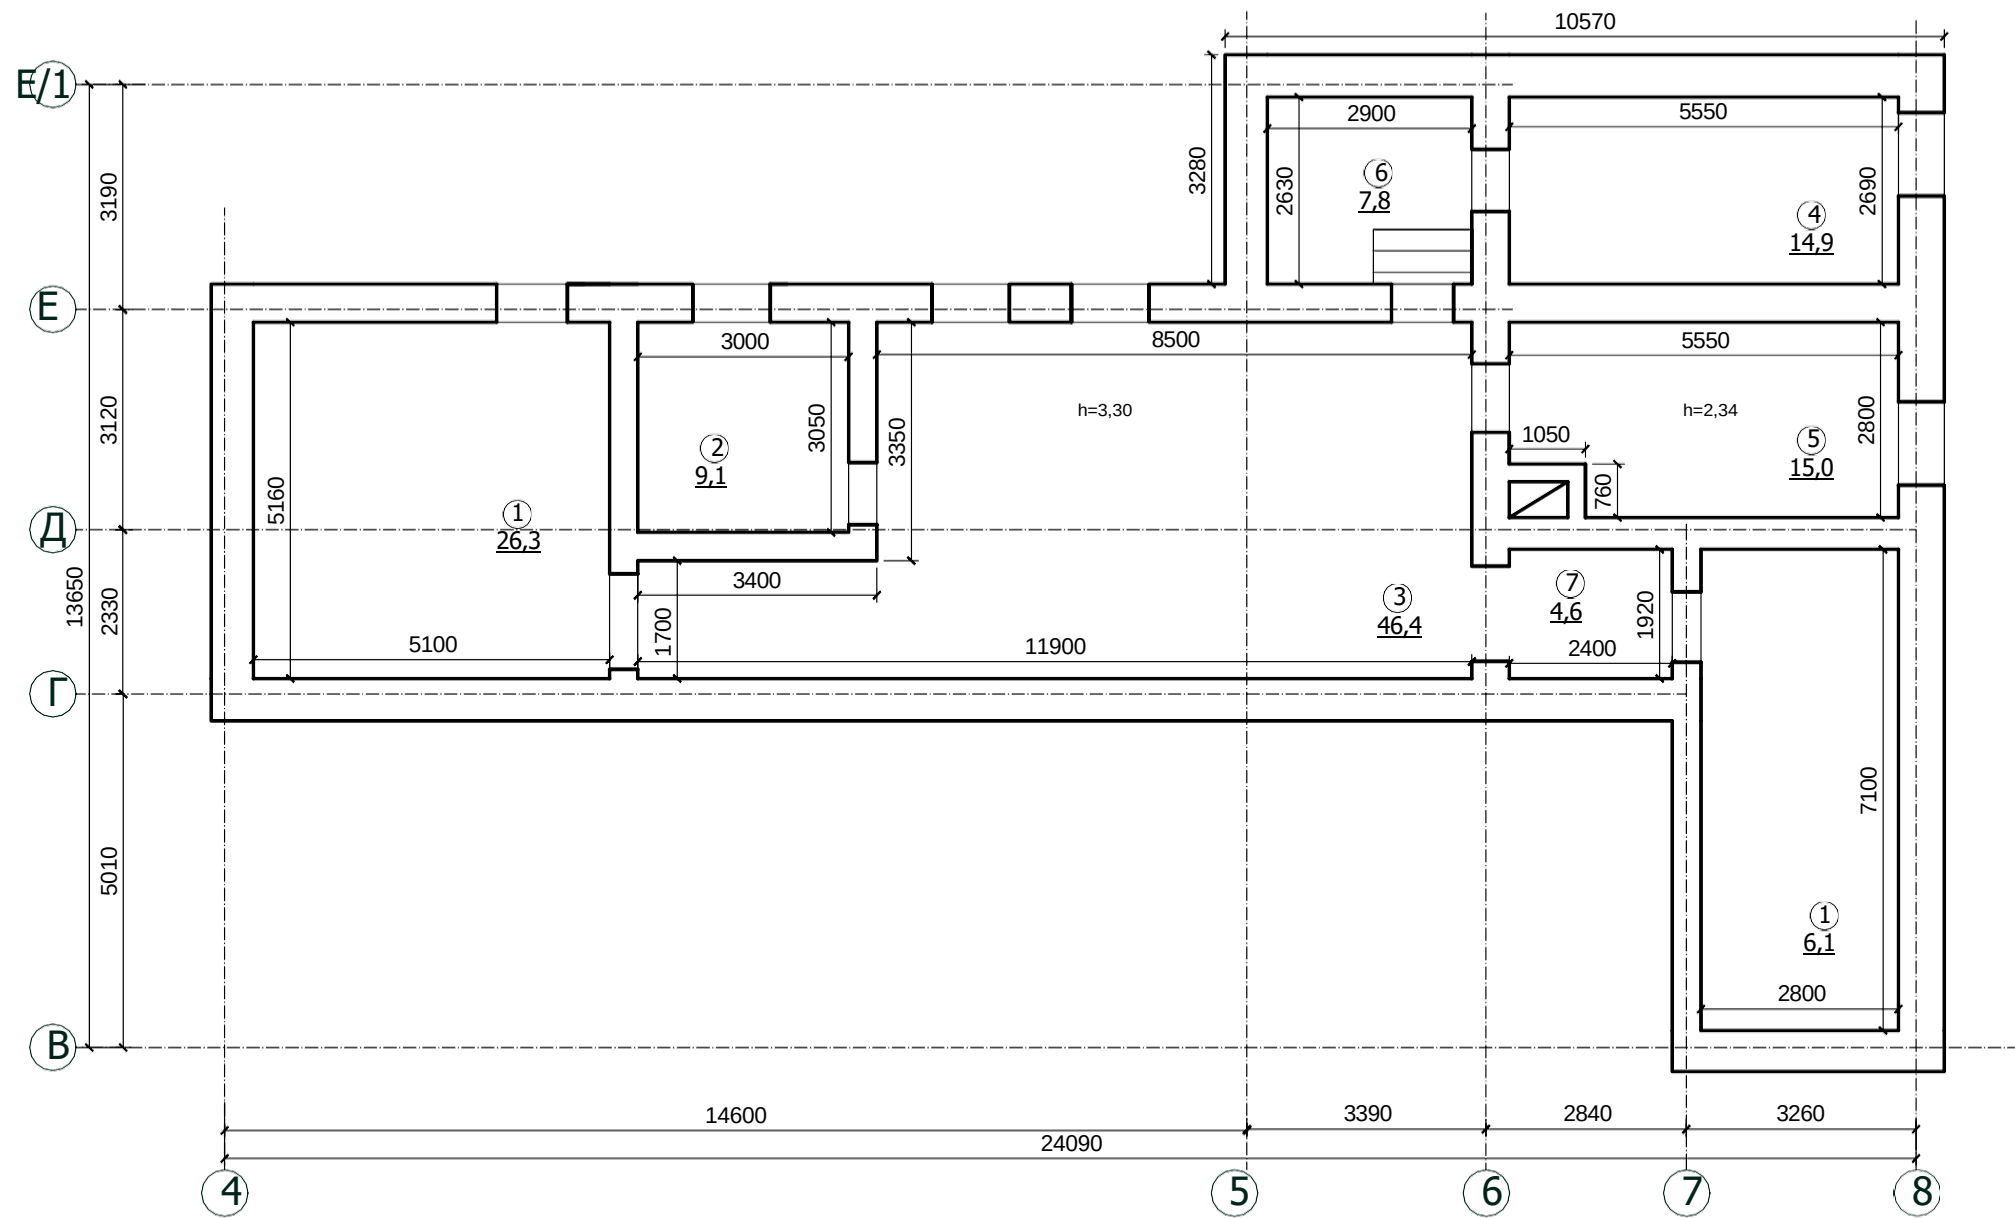

Экспликация помещений:

№ по плану		Площадь м2
1	Помещение	26,3
2	Помещение	9,1
3	Помещение	46,4
4	Помещение	14,9
5	Помещение	15,0
6	Помещение	7,8
7	Помещение	4,6
Итого:		124,1

						Заказчик: ИП							Шифр: П 29/0824			
						Адрес: : Российская Федерация, Московская область, Люберецкий р-н, рп Малаховка, ул Чайковского,д1										
Изм.	Кол. уч.	Лист	№ док.	Подп.	Дата											
Ген. дер.													Стадия		Лист	Листов
ГАП													П		2	
ГИП																
						План подвала до реконструкции по планам БТИ М 1:100							ООО ПСК "СЕРВИС"			

Копировал

А3


Согласовано

И.п. ? Подп. и дата

И.п. ? Подп. и дата


Экспликация помещений:

№ по плану	Помещение	Площадь м2
1	Помещение	18,9
2	Помещение	16,8
3	Помещение	111,3
4	Помещение	50,8
5	Помещение	63,8
6	Помещение	4,7
7	Помещение	26,2
8	Помещение	27,4
9	Помещение	39,6
10	Помещение	60,3
11	Помещение	4,8
12	Помещение	49,4
13	Помещение	15,5
Итого:		489,7

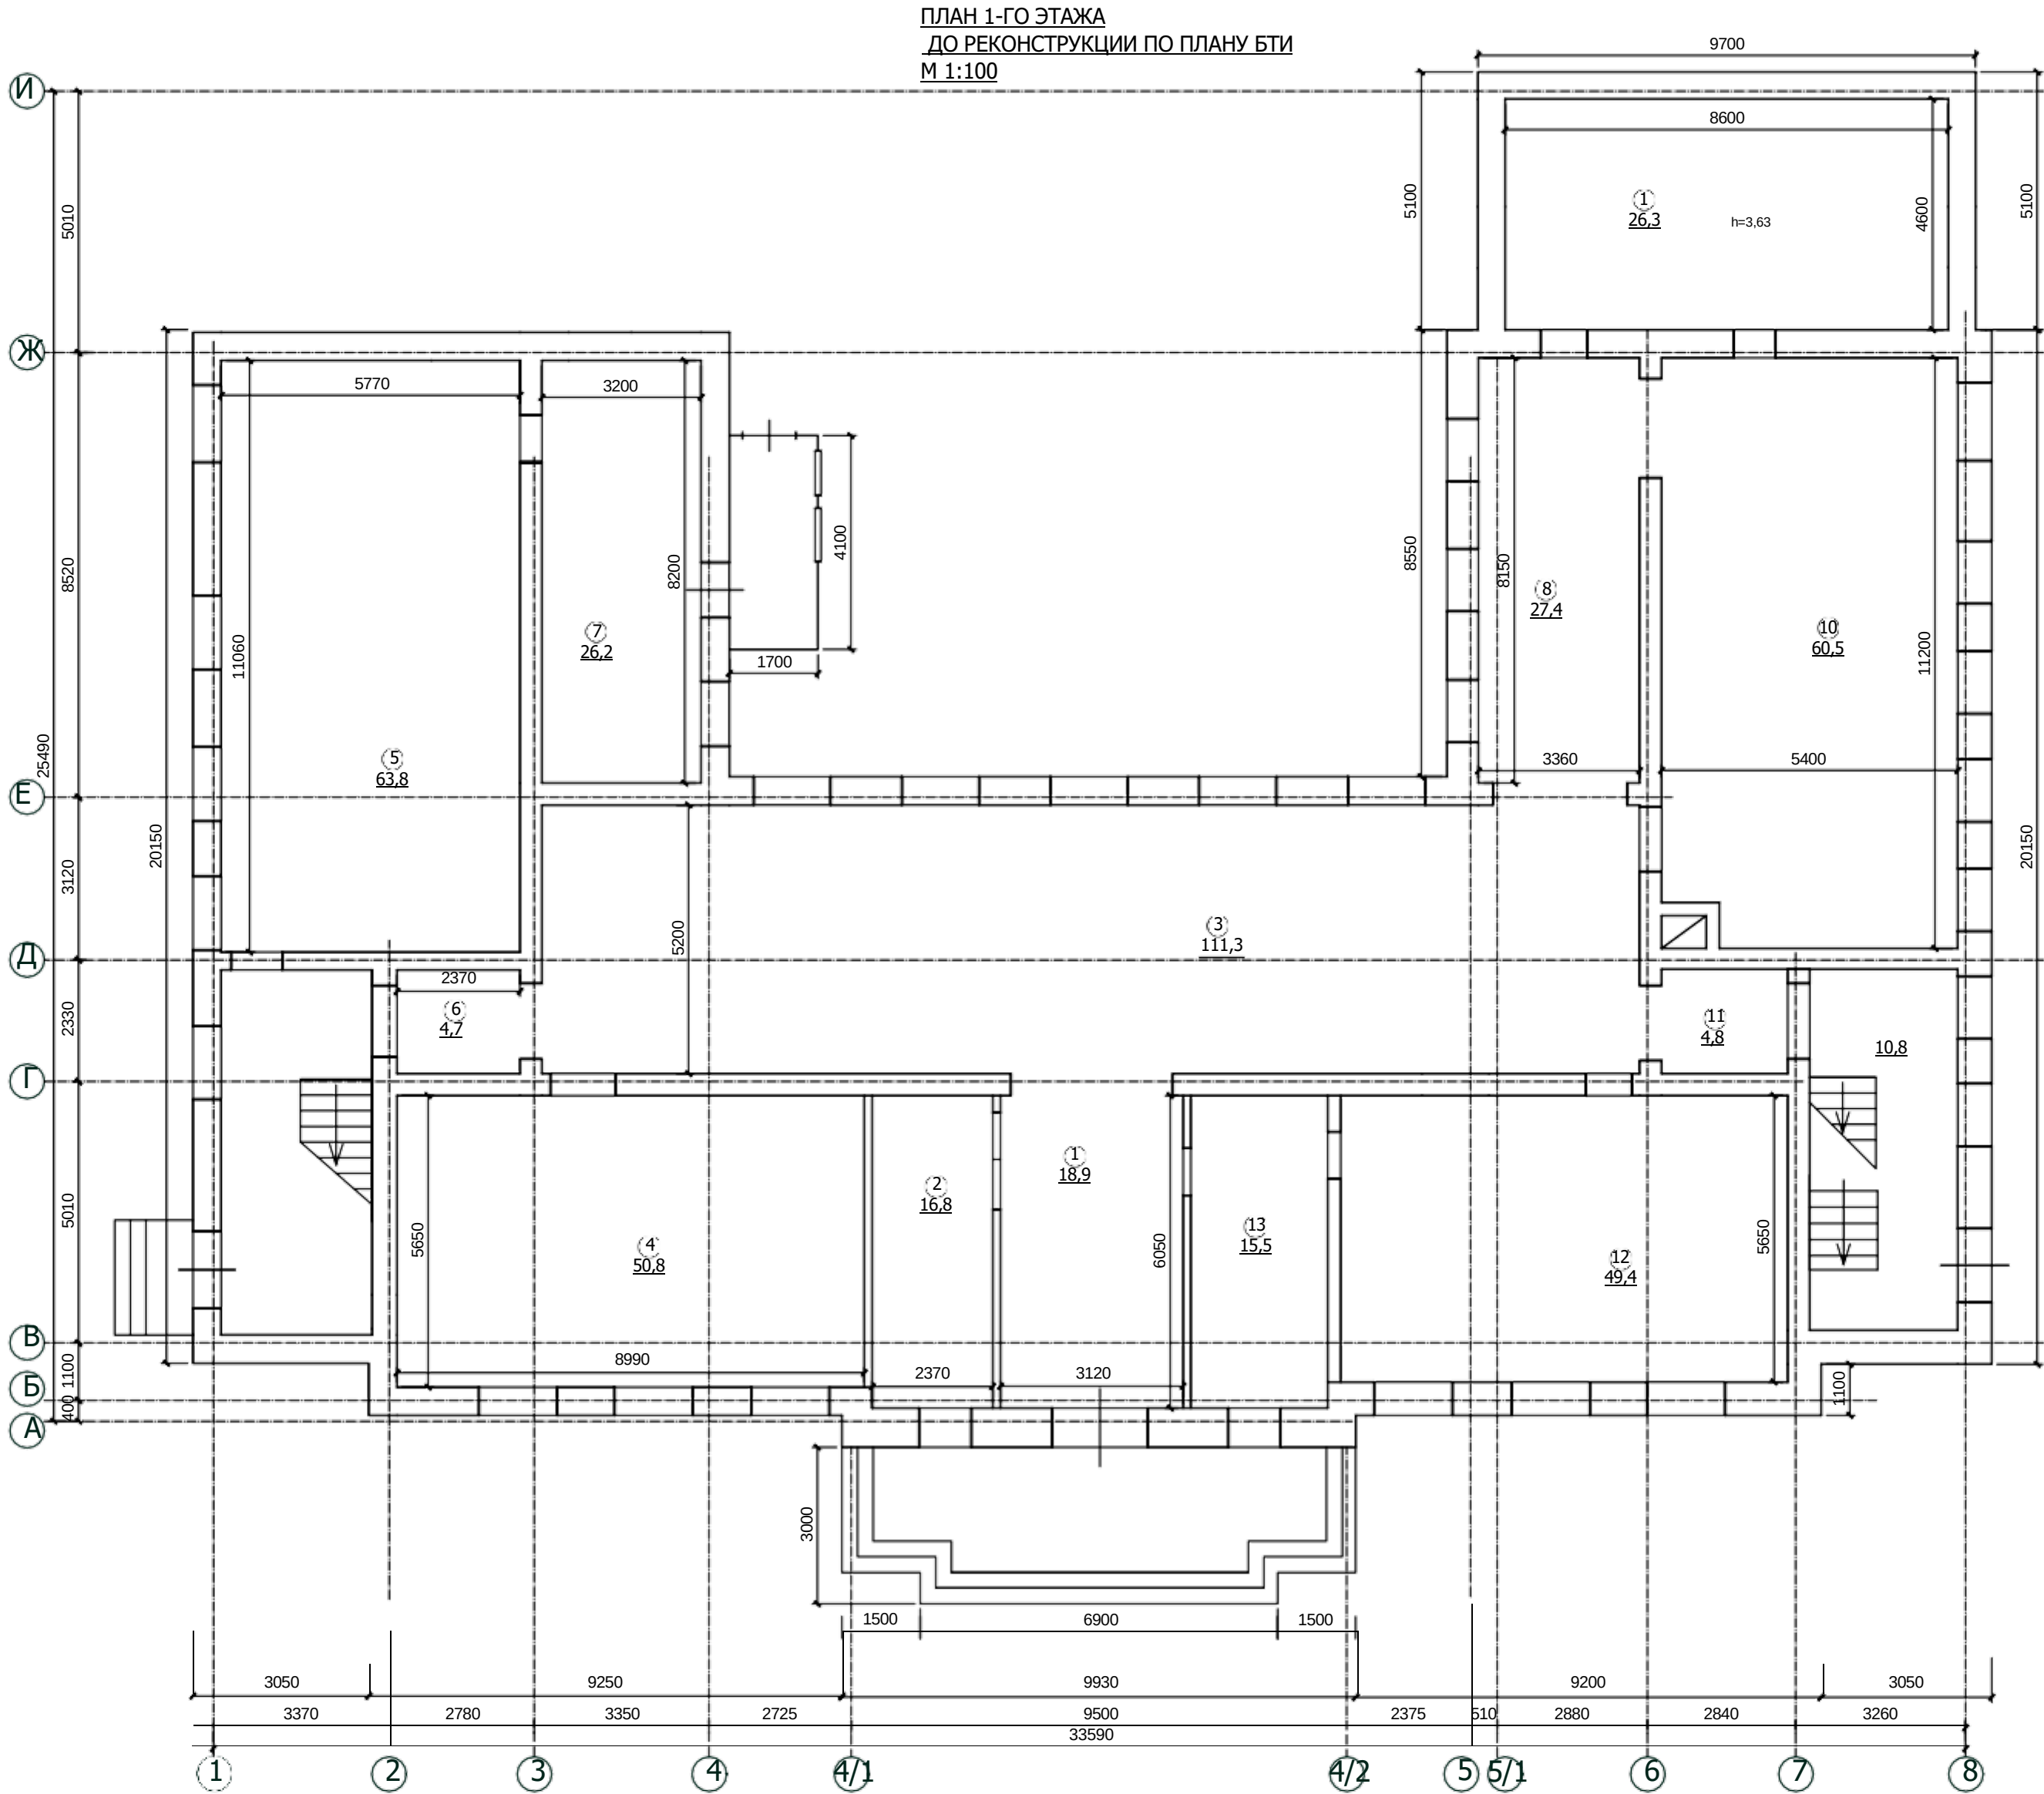

Изм.	Кол. уч.	Лист	№ док.	Подп.	Дата	Заказчик: ИП	Шифр: П 29/0824		
Ген. дер.						Адрес: : Российская Федерация, Московская область, Люберецкий р-н, рп Малаховка, ул Чайковского,д1			
ГАП						Проект реконструкции административного здания	Стадия П	Лист 3	Листов
ГИП						План 1-го этажа до реконструкции по планам БТИ М 1:100	ООО ПСК "СЕРВИС"		

ПЛАН 2-ГО ЭТАЖА
ДО РЕКОНСТРУКЦИИ ПО ПЛАНУ БТИ
М 1:100

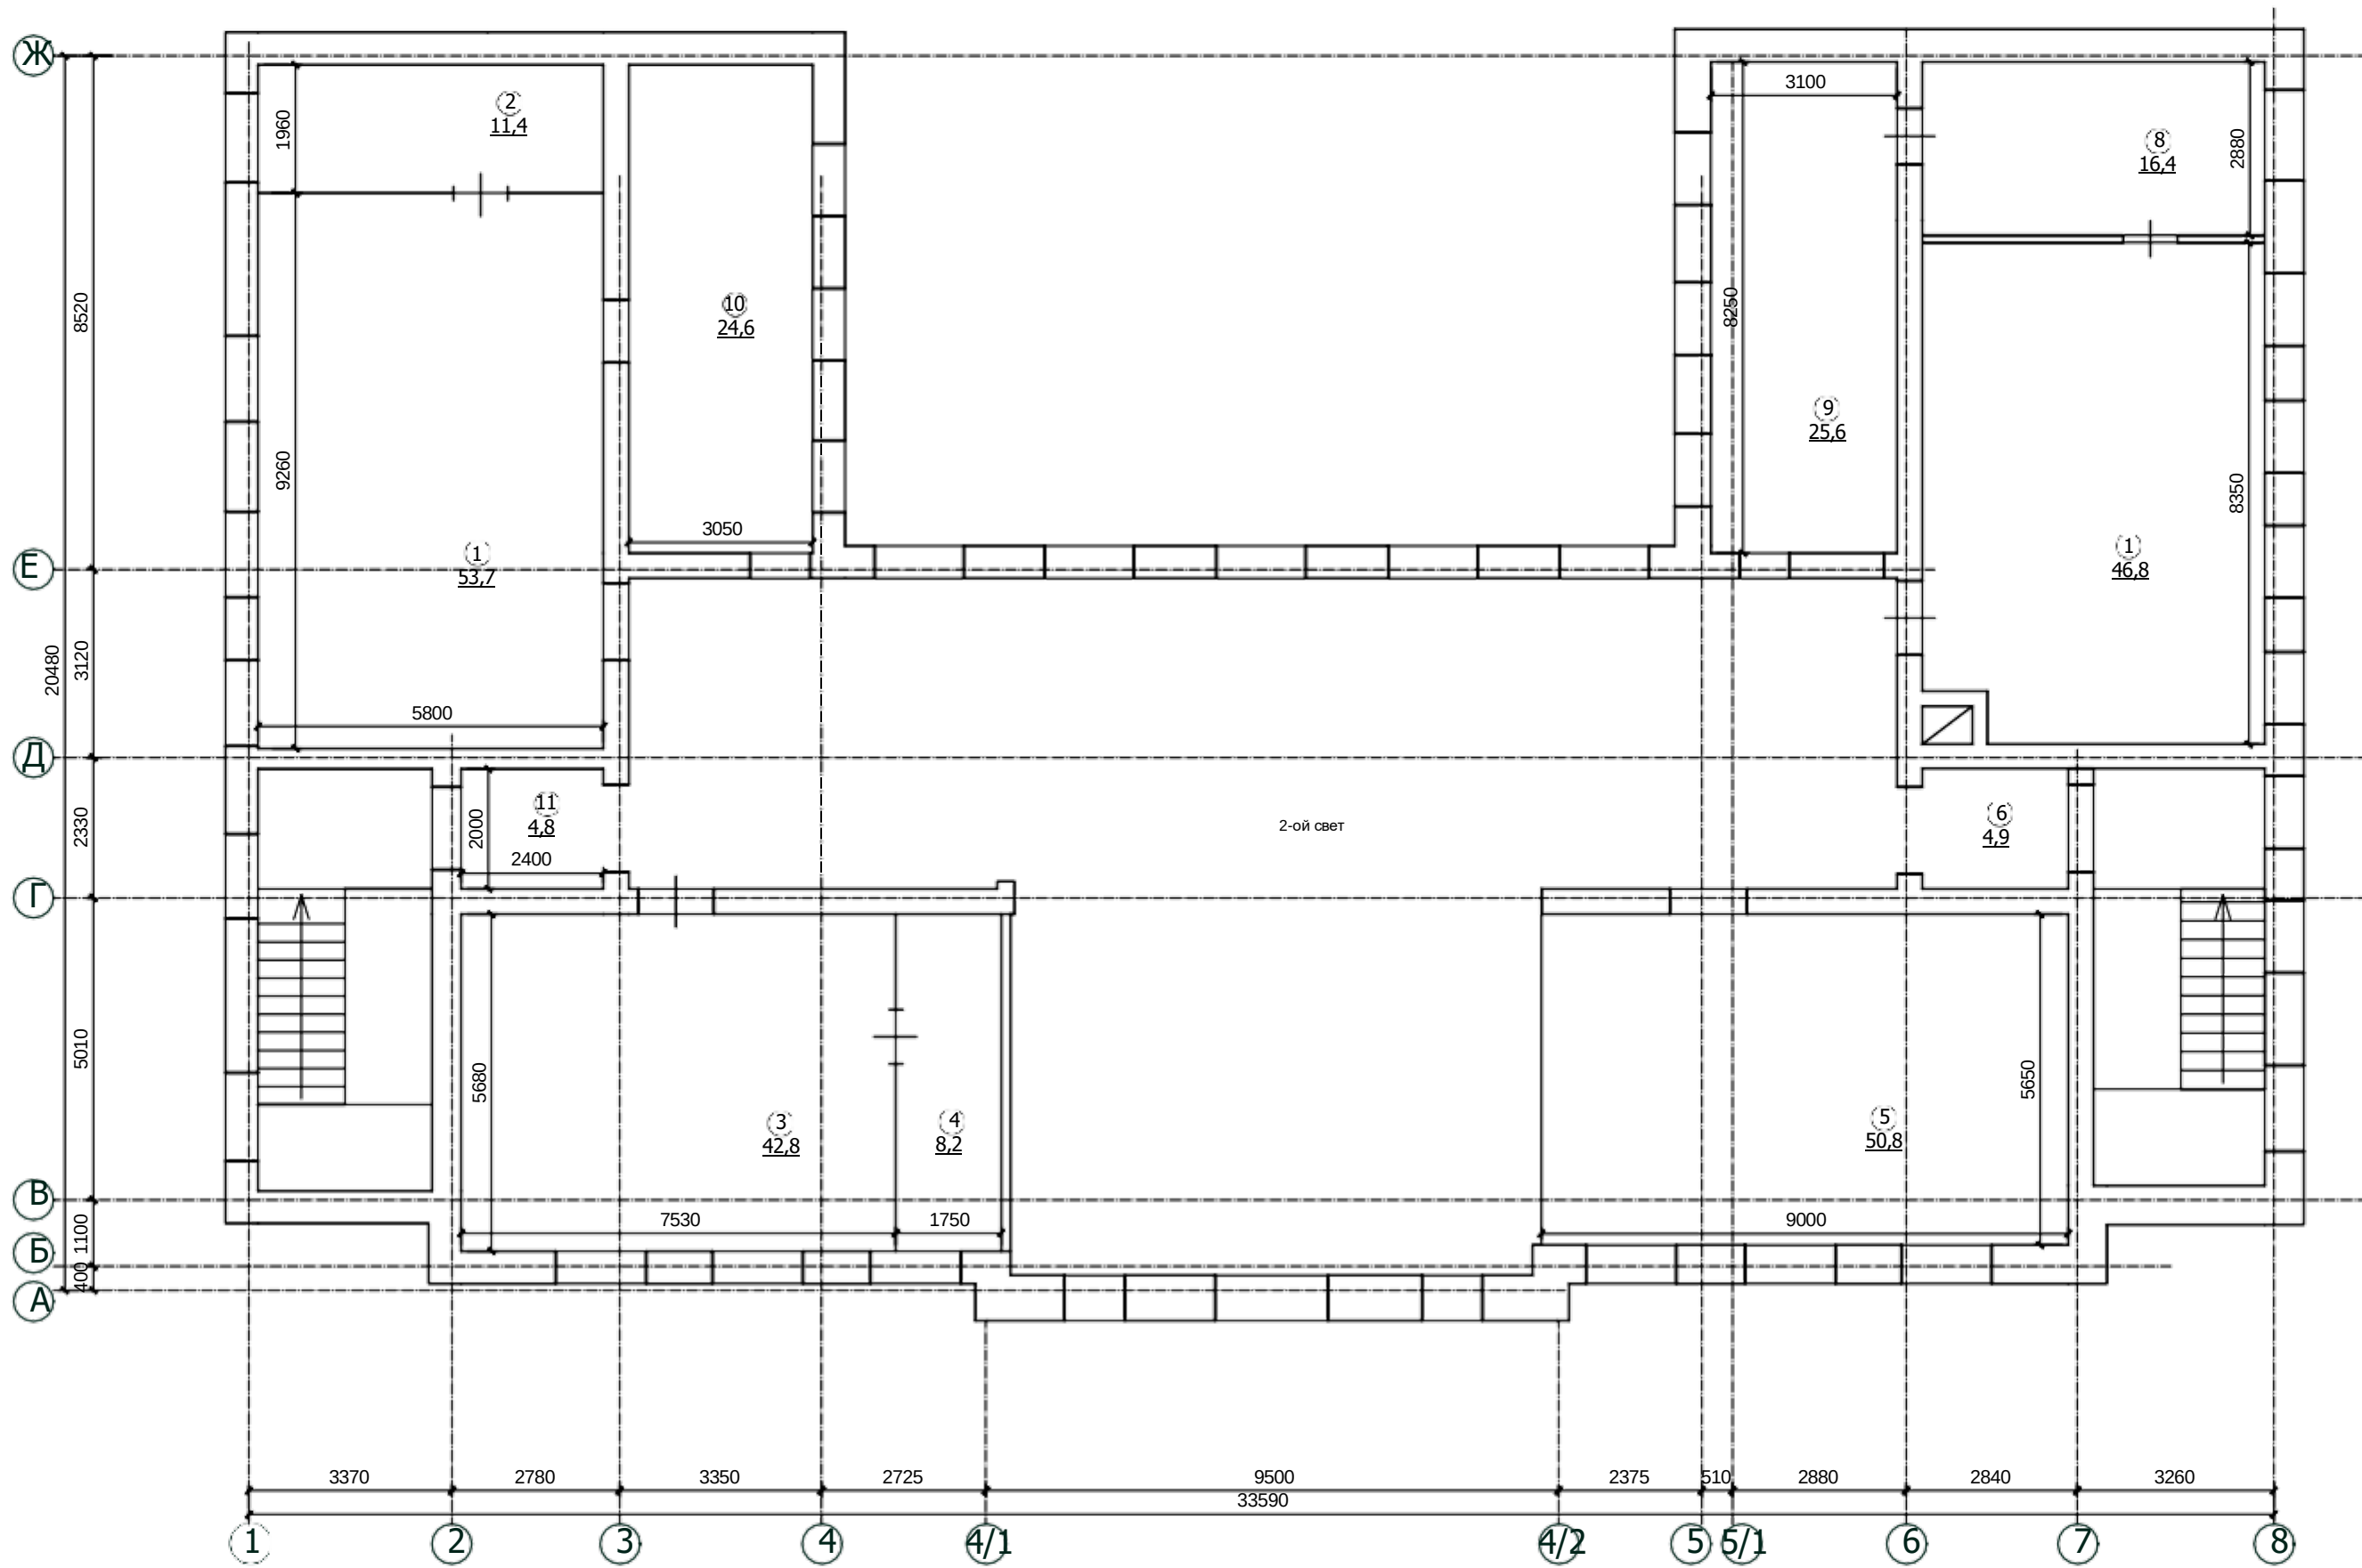

Экспликация помещений:

№ по плану		Площадь м2
1	Помещение	53,0
2	Помещение	11,4
3	Помещение	42,0
4	Помещение	8,2
5	Помещение	50,8
6	Помещение	4,9
7	Помещение	46,8
8	Помещение	16,4
9	Помещение	25,6
10	Помещение	24,6
11	Помещение	4,8
	Итого:	290,0


						Заказчик: ИП _____ Шифр: П 29/0824			
						Адрес: : Российская Федерация, Московская область, Люберецкий р-н, рп Малаховка, ул Чайковского,д1			
Изм.	Кол. уч.	Лист	№ док.	Подп.	Дата	Проект реконструкции административного здания	Стадия	Лист	Листов
Ген. дер.							П	4	
ГАП						План 2-го этажа до реконструкции по планам БТИ М 1:100	ООО ПСК "СЕРВИС"		
ГИП									

Согласовано
Уд. ? подп. Подп. и дата
Инб. ?

Экспликация помещений:

№ по плану	Помещение	Площадь м2
1	Помещение	18,9
2	Помещение	16,8
3	Помещение	111,3
4	Помещение	50,8
5	Помещение	63,8
6	Помещение	4,7
7	Помещение	26,2
8	Помещение	27,4
9	Помещение	39,6
10	Помещение	60,3
11	Помещение	4,8
12	Помещение	49,4
13	Помещение	15,5
Итого:		489,7

ПЛАН 1-ГО ЭТАЖА
М 1:100
ДЕМОНТАЖНЫЙ ПЛАН

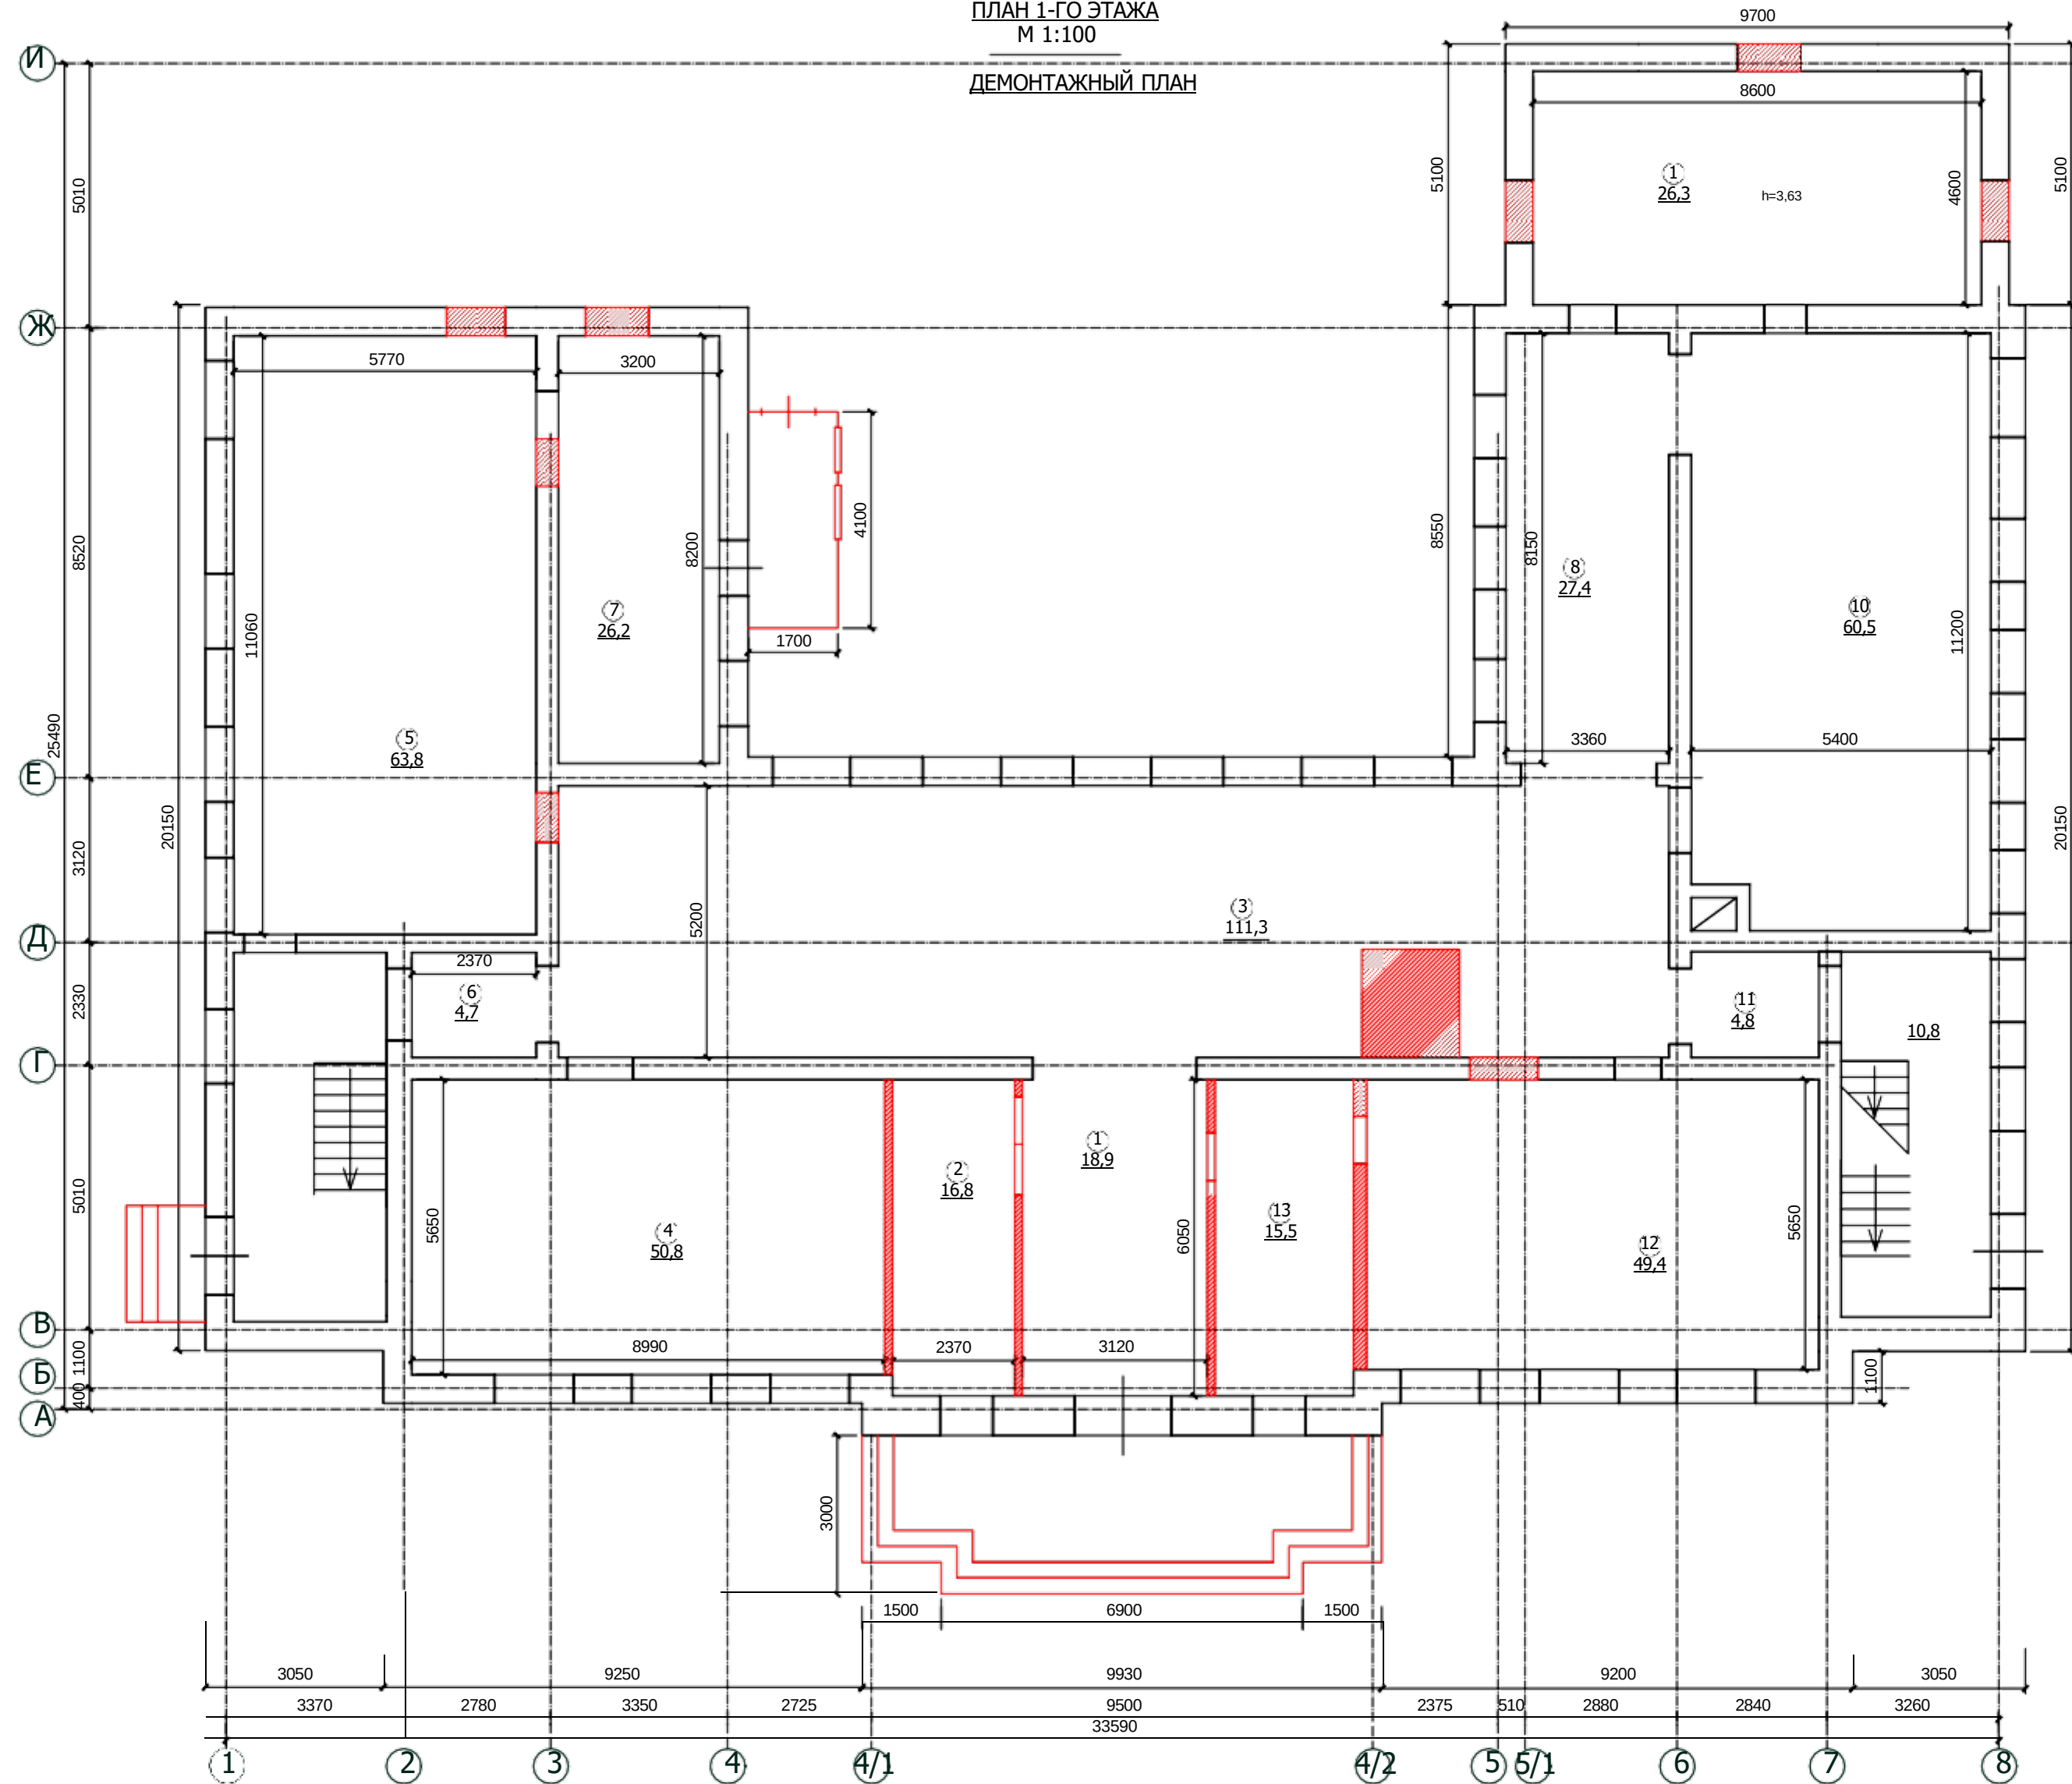


Условные обозначения

- Существующая дверь
- Демонтируемые перегородки
- Существующие стены и перегородки

						Заказчик: ИП	Шифр: П 29/0824				
						Адрес: : Российская Федерация, Московская область, Люберецкий р-н, рп Малаховка, ул Чайковского,д1					
Изм.	Кол. уч.	Лист	№ док.	Подп.	Дата			Стадия	Лист	Листов	
Ген. дер.						Проект реконструкции административного здания		П	5		
ГАП											
ГИП						План 1-го этажа демонтажный план М 1:100		ООО ПСК "СЕРВИС"			

ПЛАН 2-ГО ЭТАЖА
М 1:100
ДЕМОНТАЖНЫЙ ПЛАН

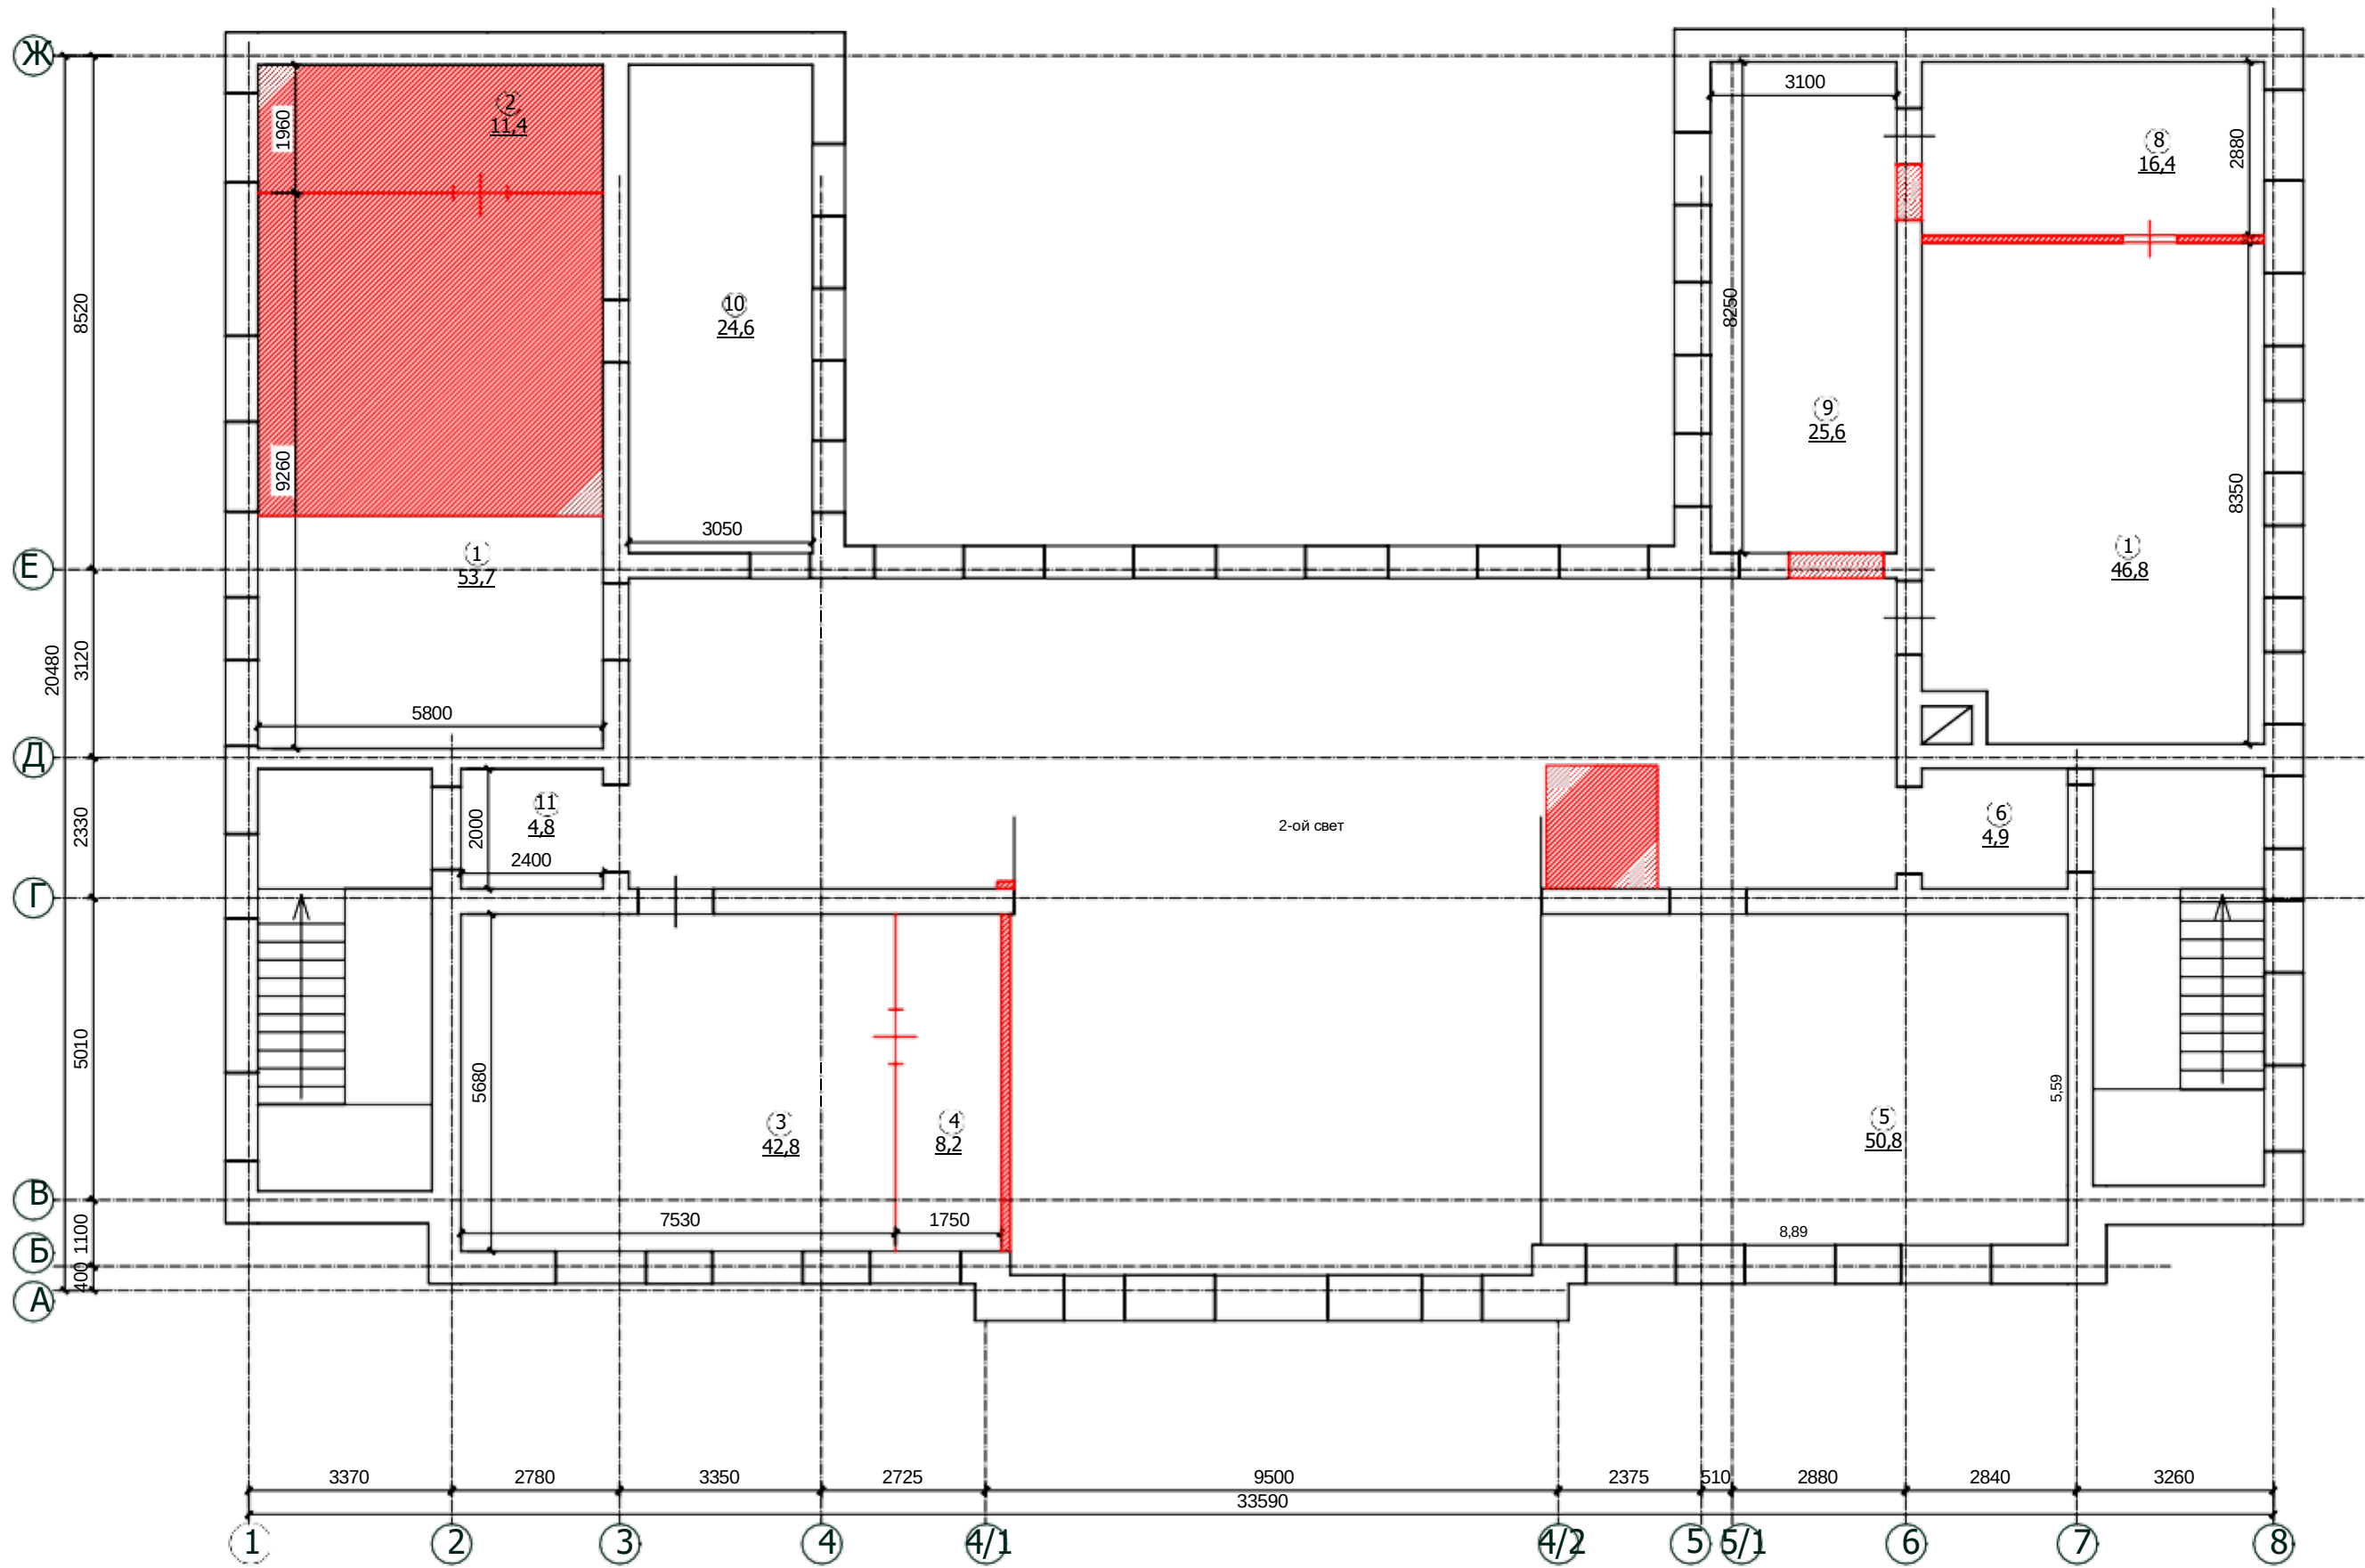

Экспликация помещений:

№ по плану		Площадь м2
1	Помещение	53,0
2	Помещение	11,4
3	Помещение	42,0
4	Помещение	8,2
5	Помещение	50,8
6	Помещение	4,9
7	Помещение	46,8
8	Помещение	16,4
9	Помещение	25,6
10	Помещение	24,6
11	Помещение	4,8
	Итого:	290,0

Условные обозначения


- Существующая дверь
- Демонтируемые перегородки
- Существующие стены и перегородки

						Заказчик: ИП _____ Шифр: П 29/0824			
						Адрес: : Российская Федерация, Московская область, Люберецкий р-н, рп Малаховка, ул Чайковского,д1			
Изм.	Кол. уч.	Лист	№ док.	Подп.	Дата	Проект реконструкции административного здания	Стадия	Лист	Листов
Ген. дер.							П	6	
ГАП						План 2-го этажа демонтажный план М 1:100	ООО ПСК "СЕРВИС"		
ГИП									

Копировать

A2

ПЛАН ПОДВАЛА
М 1:100
МОНТАЖНЫЙ ПЛАН

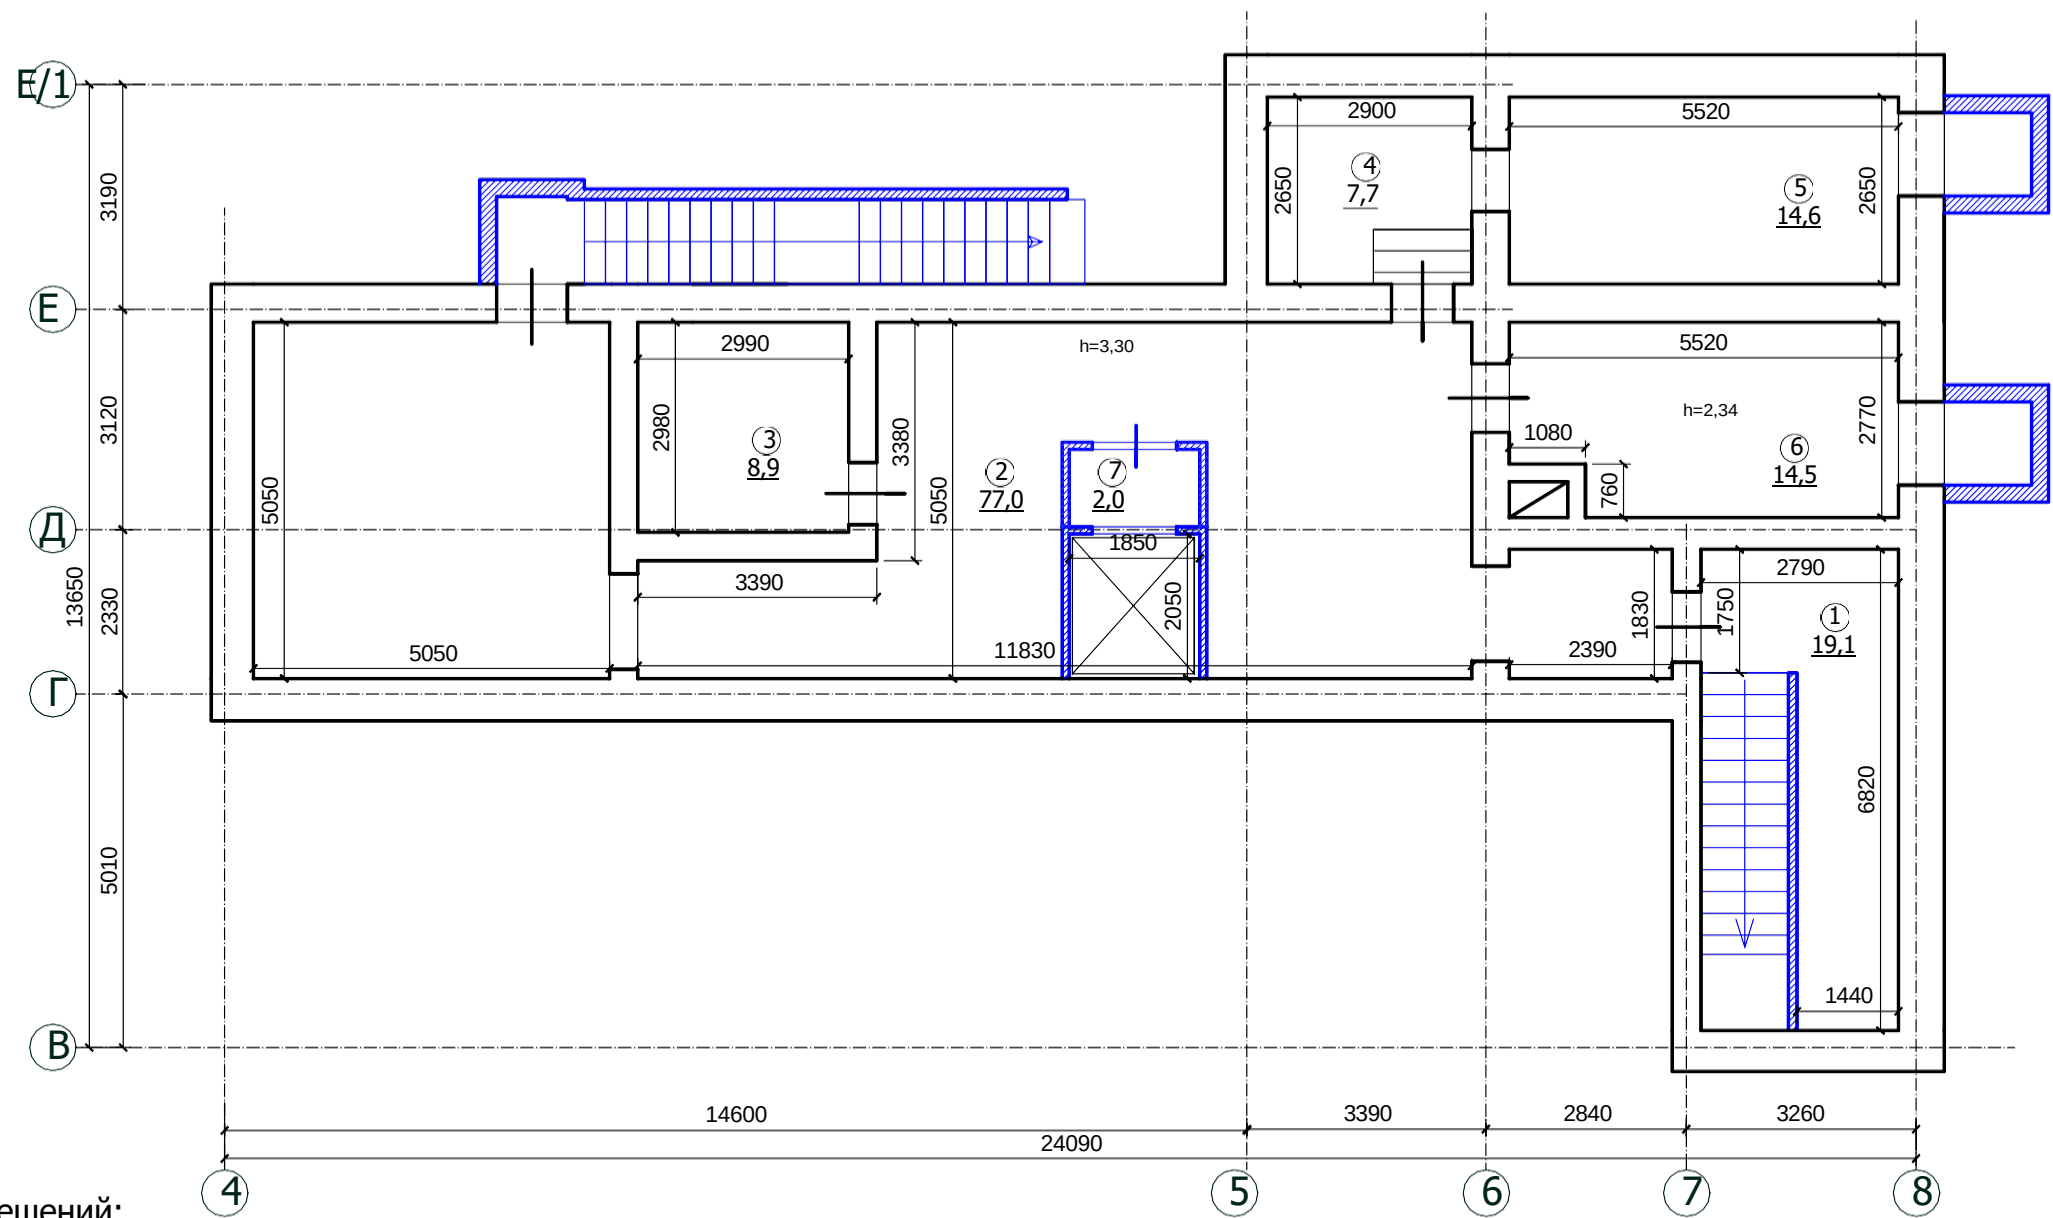

Экспликация помещений:

№ по плану	Помещение	Площадь м2
1	Помещение	19,1
2	Коридор	77,0
3	Помещение	8,9
4	Помещение	7,7
5	Помещение	14,6
6	Помещение	14,5
7	Тамбур	2,0
Итого:		143,7
Общая площадь этажа		168,5


Условные обозначения




- Закладываемый проем



- Возводимые стены и перегородки

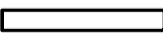

- Существующие перегородки

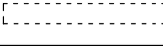

- Сносимые перегородки

						Заказчик: ИП				Шифр: П 29/0824			
						Адрес: : Российская Федерация, Московская область, Люберецкий р-н, рп Малаховка, ул Чайковского,д1							
Изм.	Кол. уч.	Лист	№ док.	Подп.	Дата	Проект реконструкции административного здания				Стадия	Лист	Листов	
Ген. дер.										П	7		
ГАП													
ГИП						План подвала монтажный план М 1:100				ООО ПСК "СЕРВИС"			


Копировал

А3

Согласовано
Инв. ? Подп. и дата
Инв. ? Подп. и дата

Экспликация помещений:

№ по плану		Площадь м2
1	Вестибюль	268,5
2	Лестничная клетка	15,1
3	Помещение	64,6
4	Помещение	24,7
5	Помещение	25,2
6	Помещение	37,6
7	Помещение	63,3
8	Лестничная клетка	10,8
9	Тамбур	4,2
10	Помещение	1,5
Итого:		515,5
Общая площадь этажа		567,5

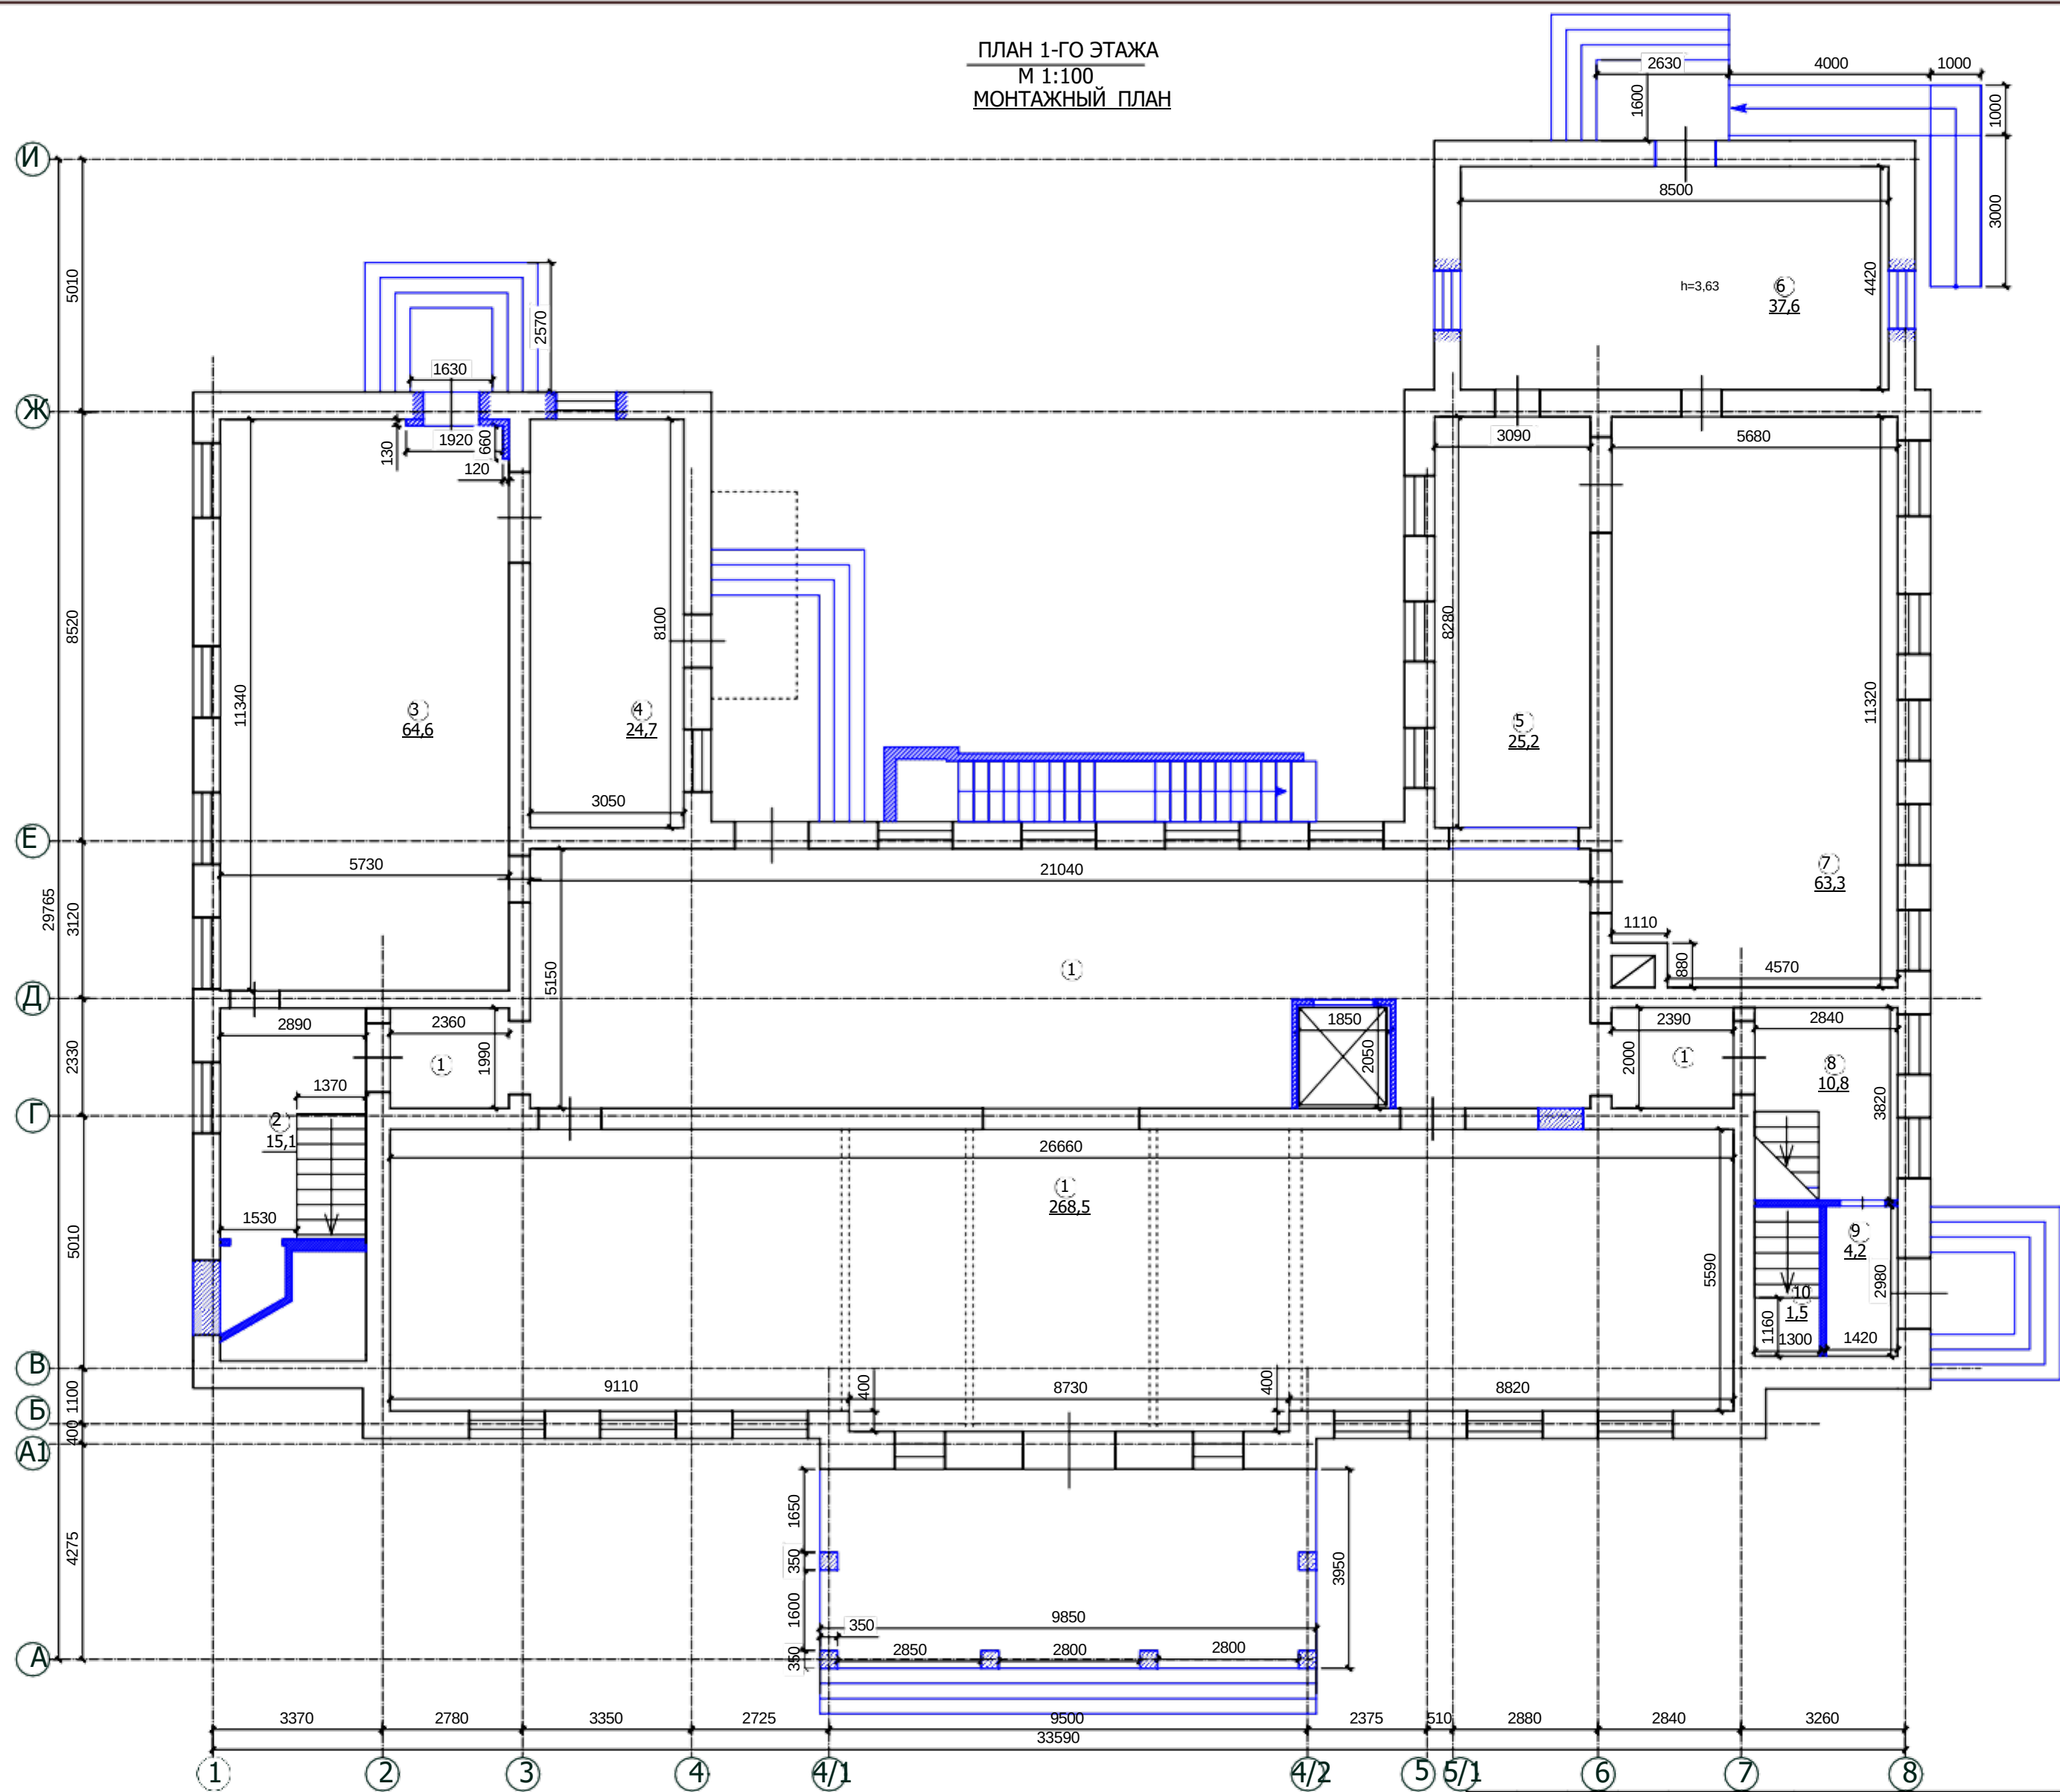


- Условные обозначения
- Закладываемый проем
 - Возводимые стены и перегородки
 - Существующие перегородки
 - Сносимые перегородки

Изм.	Кол. уч.	Лист	№ док.	Подп.	Дата	Заказчик: ИП	Шифр: П 29/0824		
Ген. дер.						Адрес: : Российская Федерация, Московская область, Люберецкий р-н, рп Малаховка, ул Чайковского, д1			
ГАП						Проект реконструкции административного здания	Стадия П	Лист 8	Листов
ГИП						План 1-го этажа монтажный план М 1:100	ООО ПСК "СЕРВИС"		

Экспликация помещений:

№ по плану		Площадь м2
1	Вестибюль	151,6
2	Вестибюль	104,6
3	Коридор	4,7
4	Коридор	4,8
5	Лестничная клетка	5,8
6	Помещение	22,1
7	Помещение	24,7
8	Помещение	25,2
9	Помещение	38,3
10	Помещение	63,3
11	Лестничная клетка	5,7
12	Помещение	35,2
	Итого:	486,0
	Общая площадь этажа	570,5

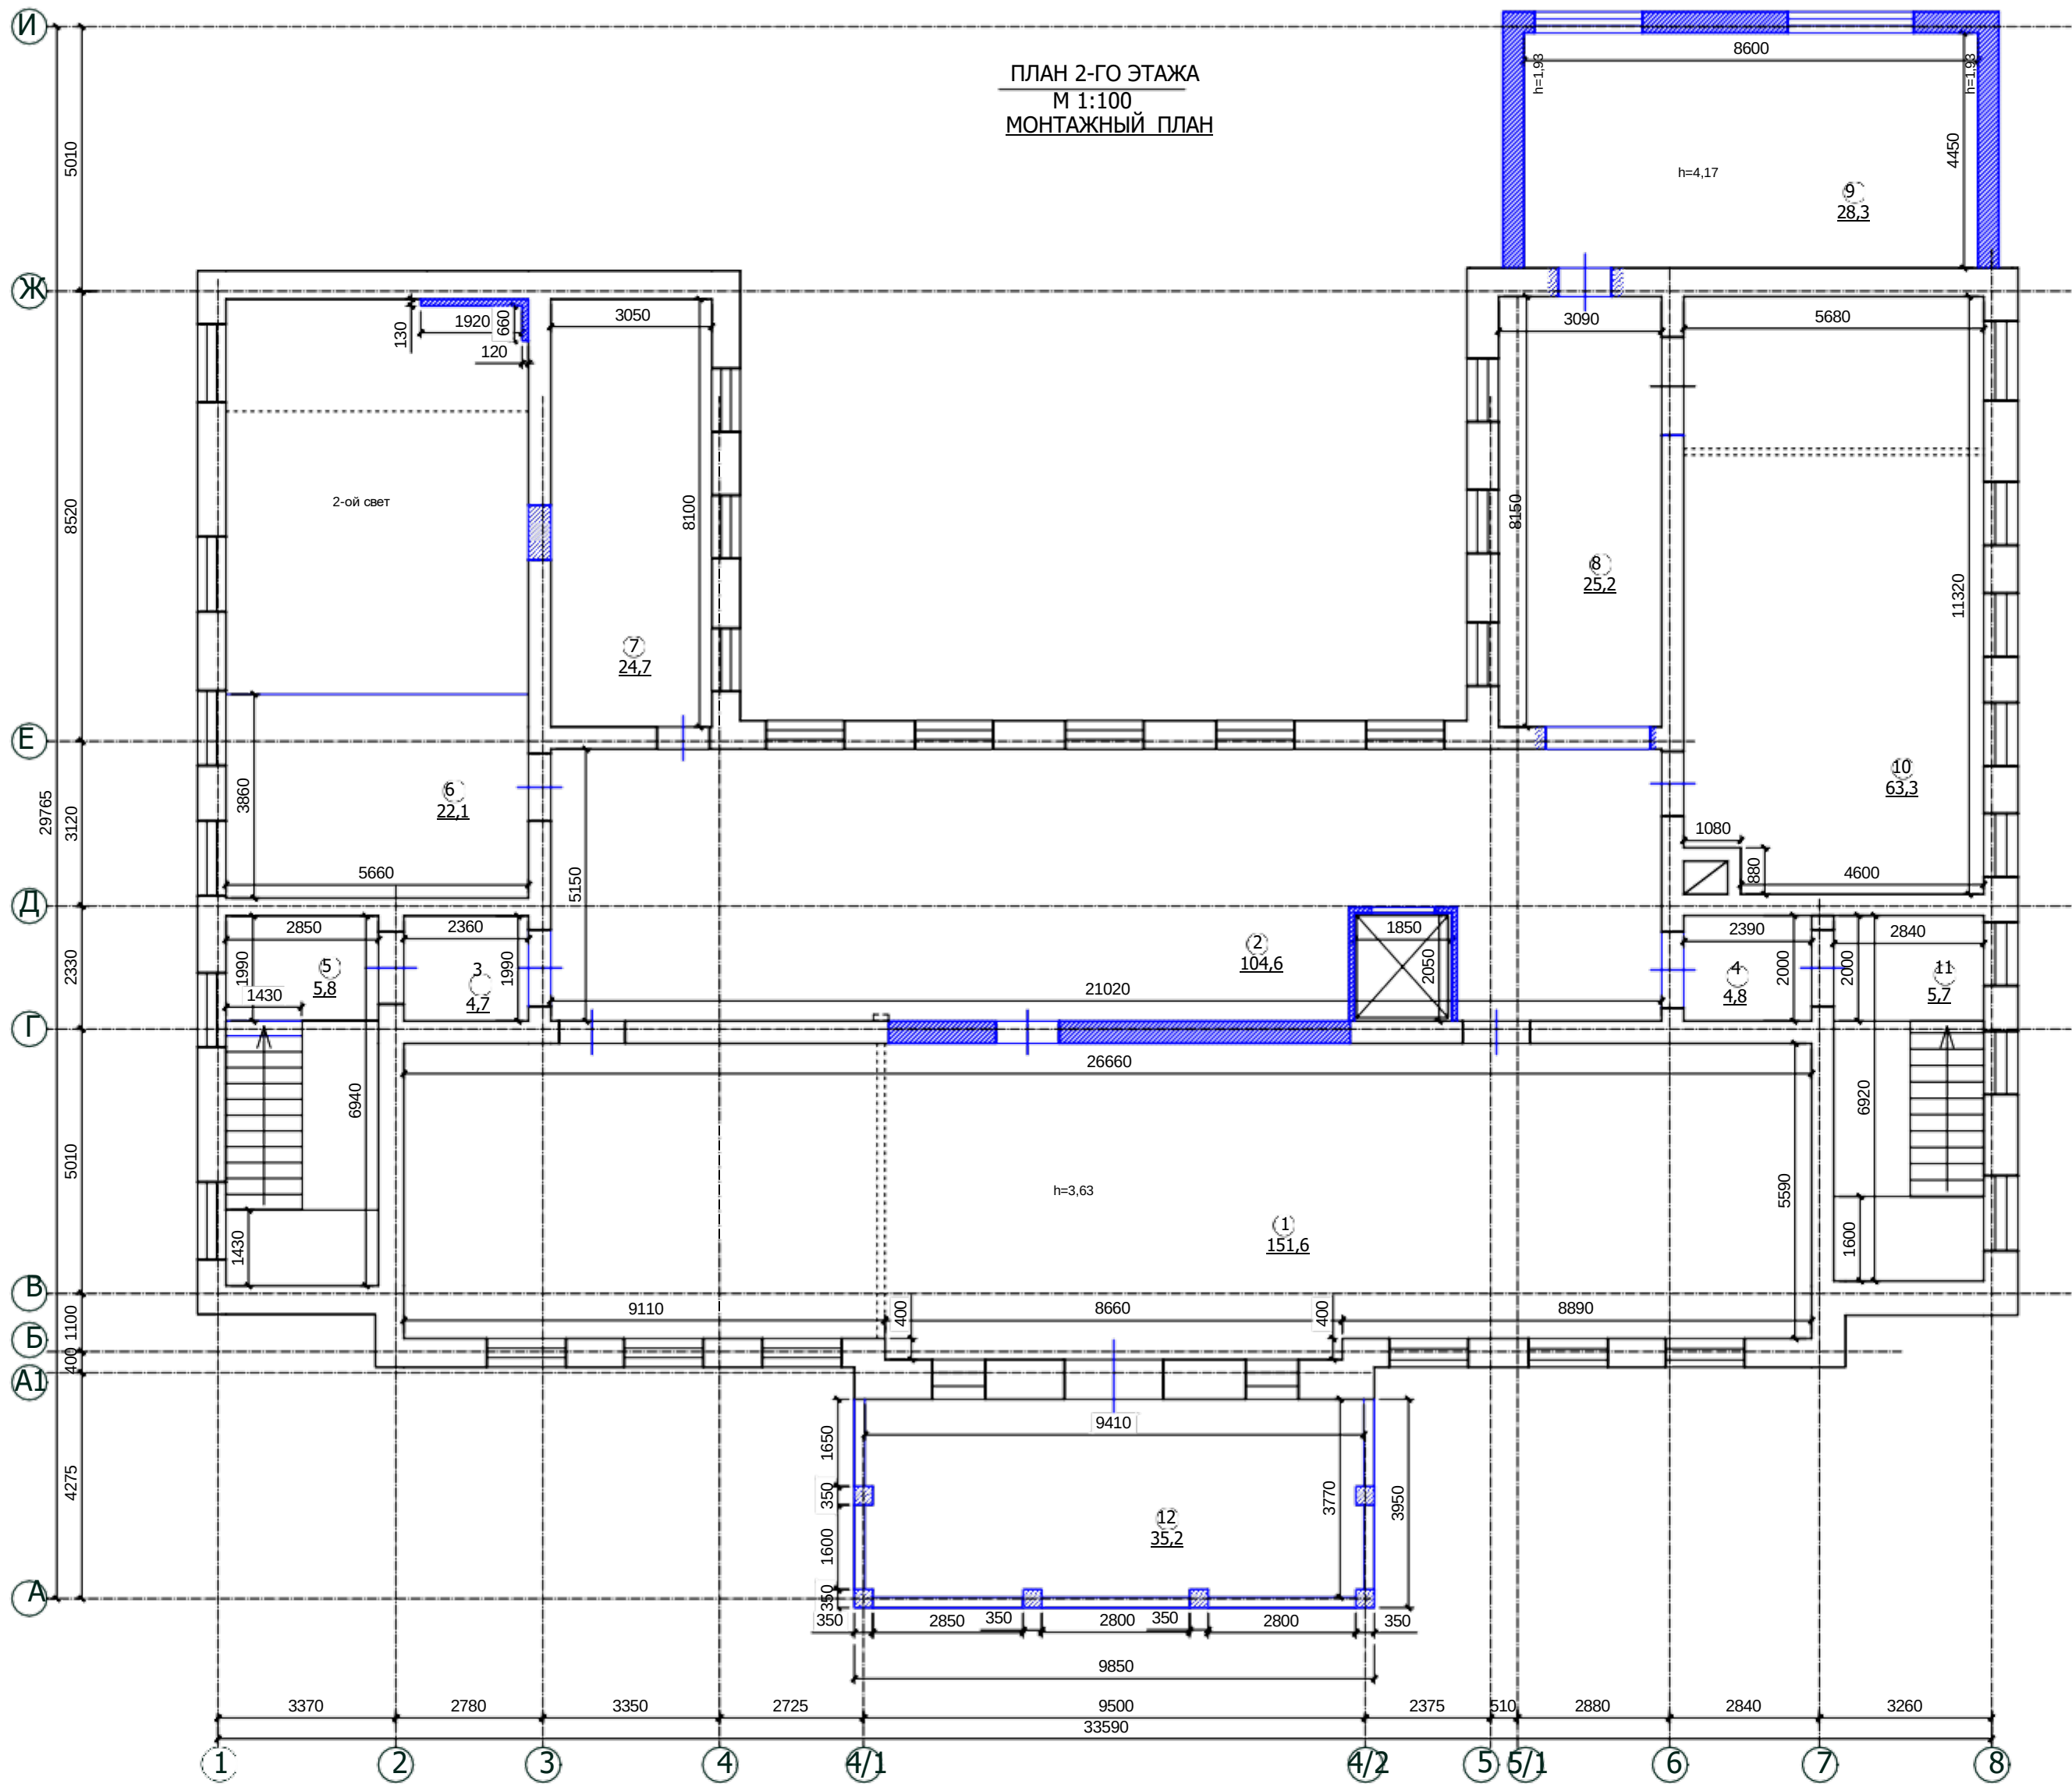

Условные обозначения

- Закладываемый проем
- Возводимые стены и перегородки
- Существующие перегородки
- Сносимые перегородки

Изм.	Кол. уч.	Лист	№ док.	Подп.	Дата	Заказчик: ИП	Шифр: П 29/0824
Ген. дер.	ГАП	ГИП				Адрес: : Российская Федерация, Московская область, Люберецкий р-н, рп Малаховка, ул Чайковского,д1	
						Проект реконструкции административного здания	Стадия Лист Листов П 9
						План 2-го этажа монтажный план М 1:100	ООО ПСК "СЕРВИС"


Согласовано

И.И.И. ? подп. и дата

Экспликация помещений:

№ по плану	Помещение	Площадь м2
1	Помещение	307,1
2	Помещение	161,9
3	Лестничная клетка	20,2
4	Лестничная клетка	20,2
5	Коридор	5,1
6	Коридор	5,4
Итого:		519,9
Общая площадь этажа		536,6

ПЛАН МАНСАРДЫ
М 1:100
МОНТАЖНЫЙ ПЛАН

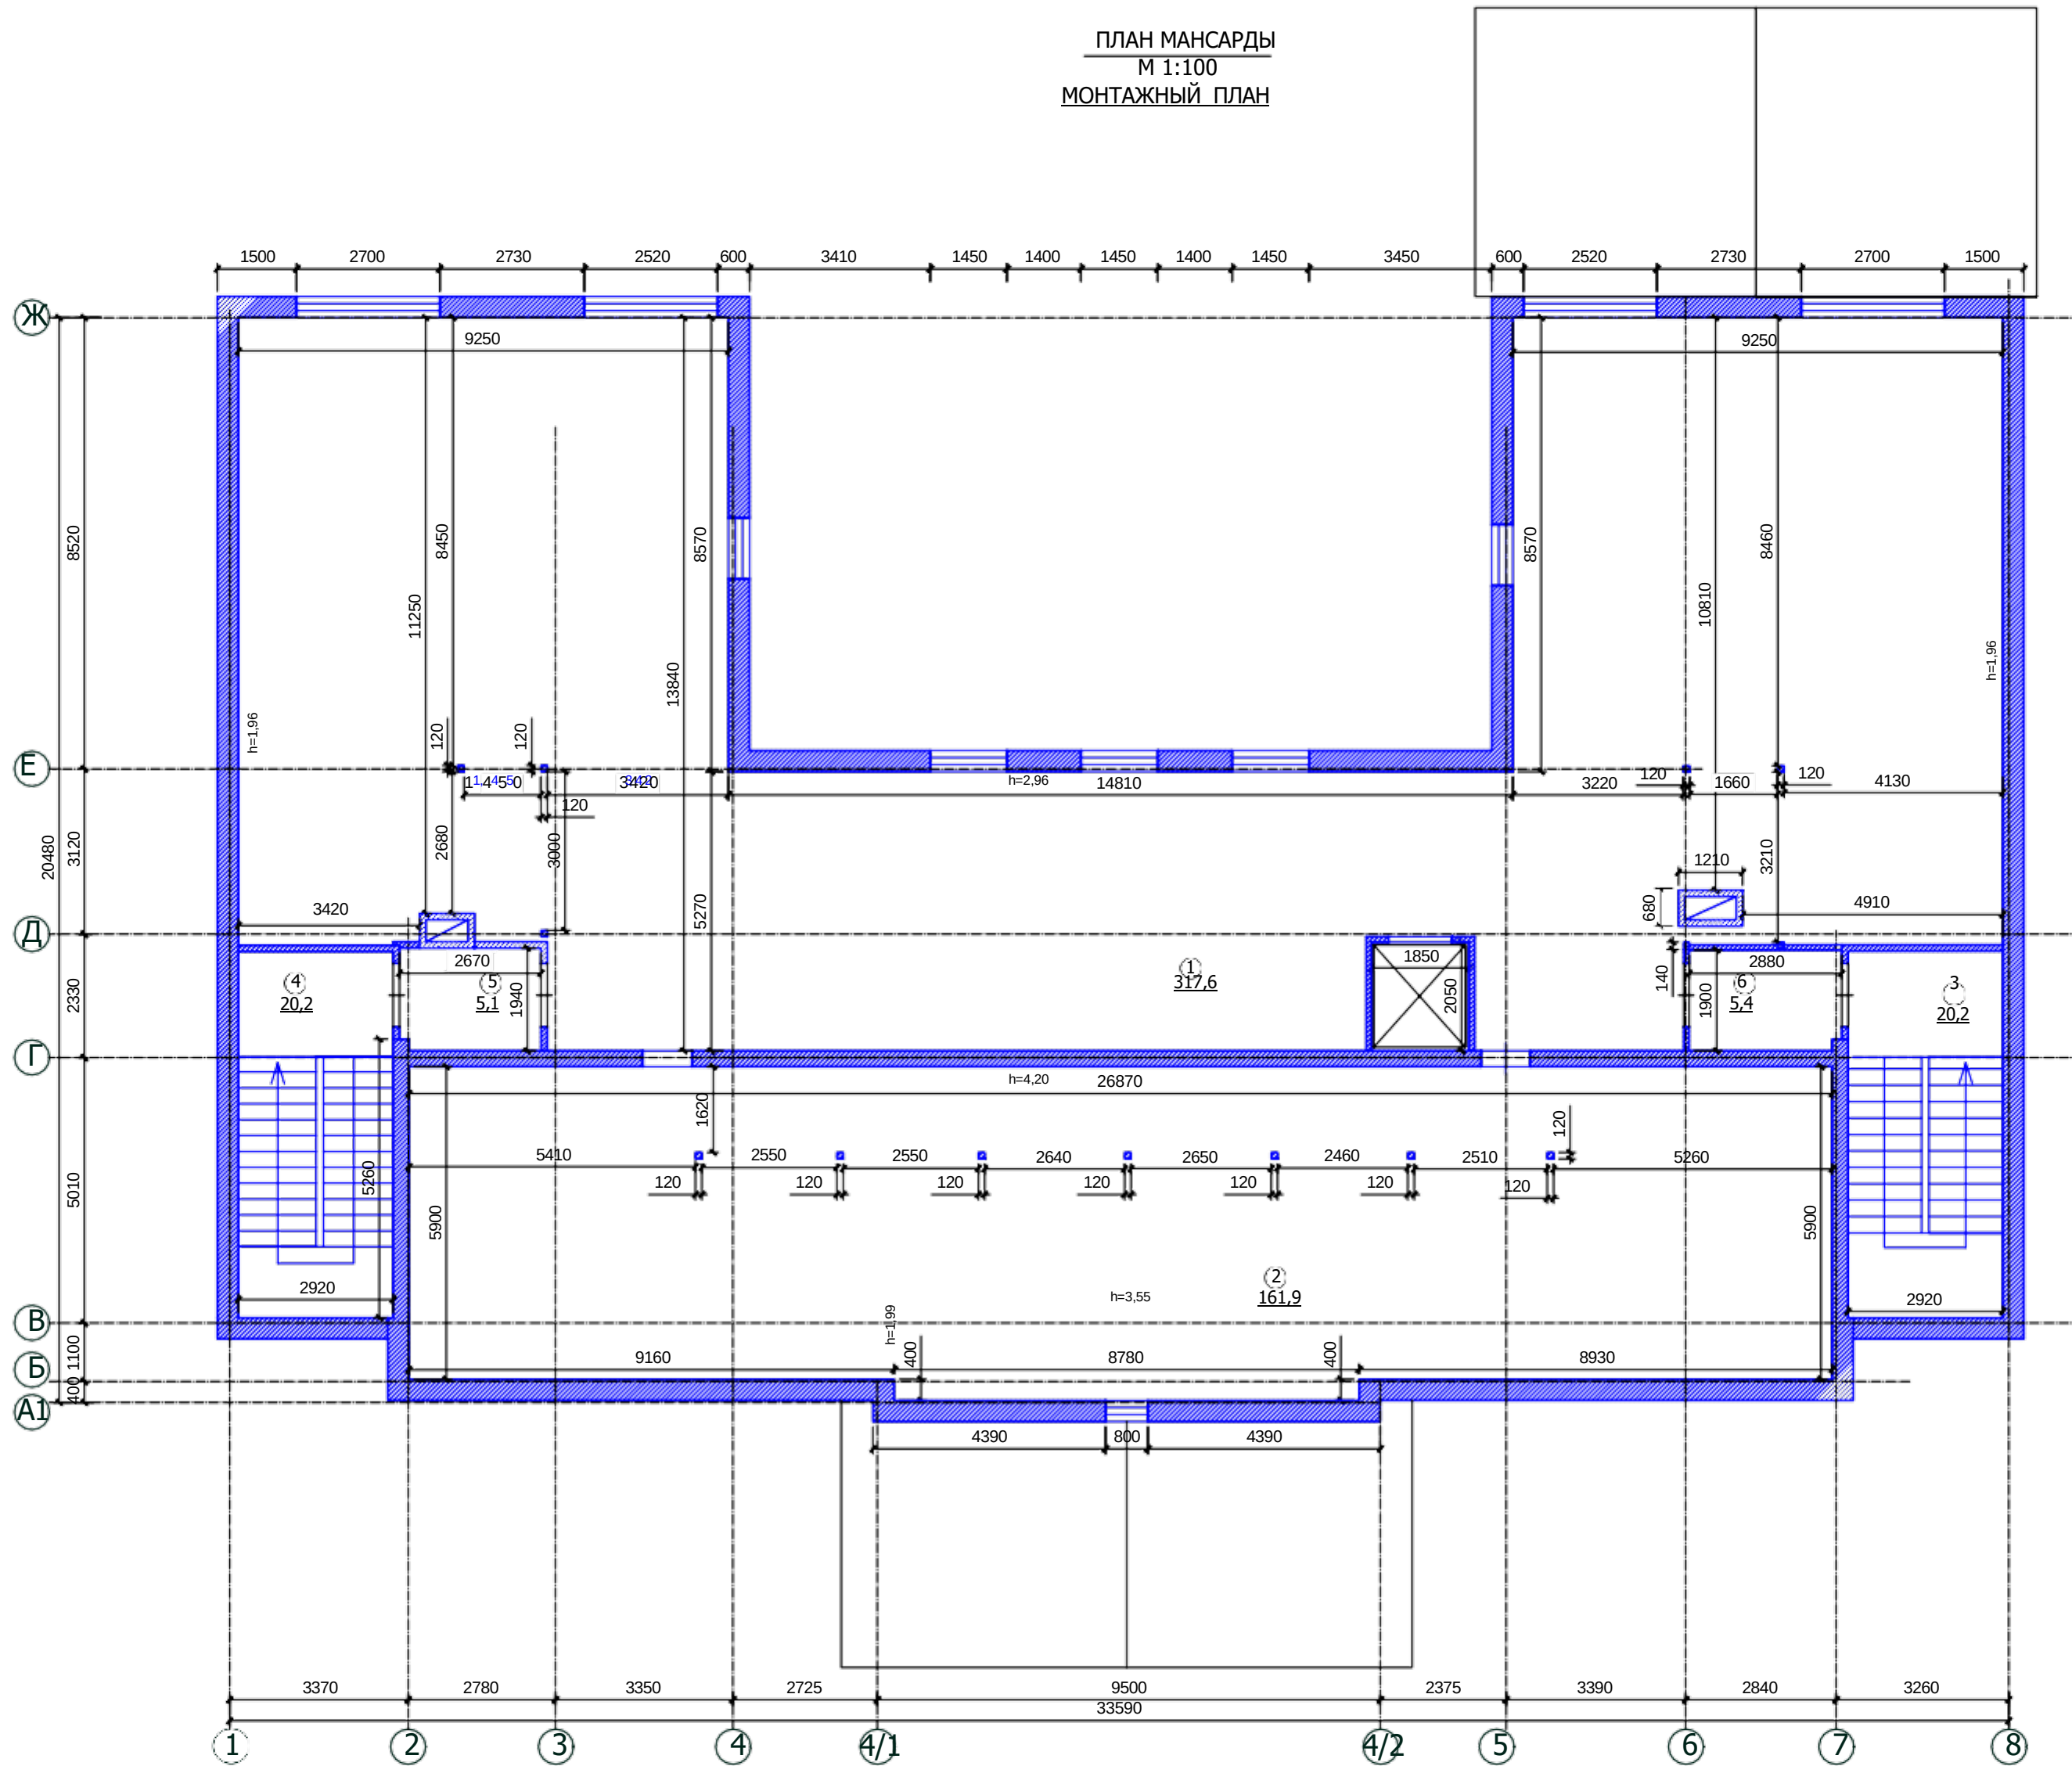


Условные обозначения

- Закладываемый проем
- Возводимые стены и перегородки
- Существующие перегородки
- Сносимые перегородки

						Заказчик: ИП _____ Шифр: П 29/0824				
						Адрес: : Российская Федерация, Московская область, Люберецкий р-н, рп Малаховка, ул Чайковского,д1				
Изм.	Кол. уч.	Лист	№ док.	Подп.	Дата					
Ген. дер.						Проект реконструкции административного здания		Стадия	Лист	Листов
ГАП								П	10	
ГИП						План мансарды монтажный план М 1:100		ООО ПСК "СЕРВИС"		

Копировать

ПЛАН ПОДВАЛА
ПОСЛЕ РЕКОНСТРУКЦИИ
М 1:100

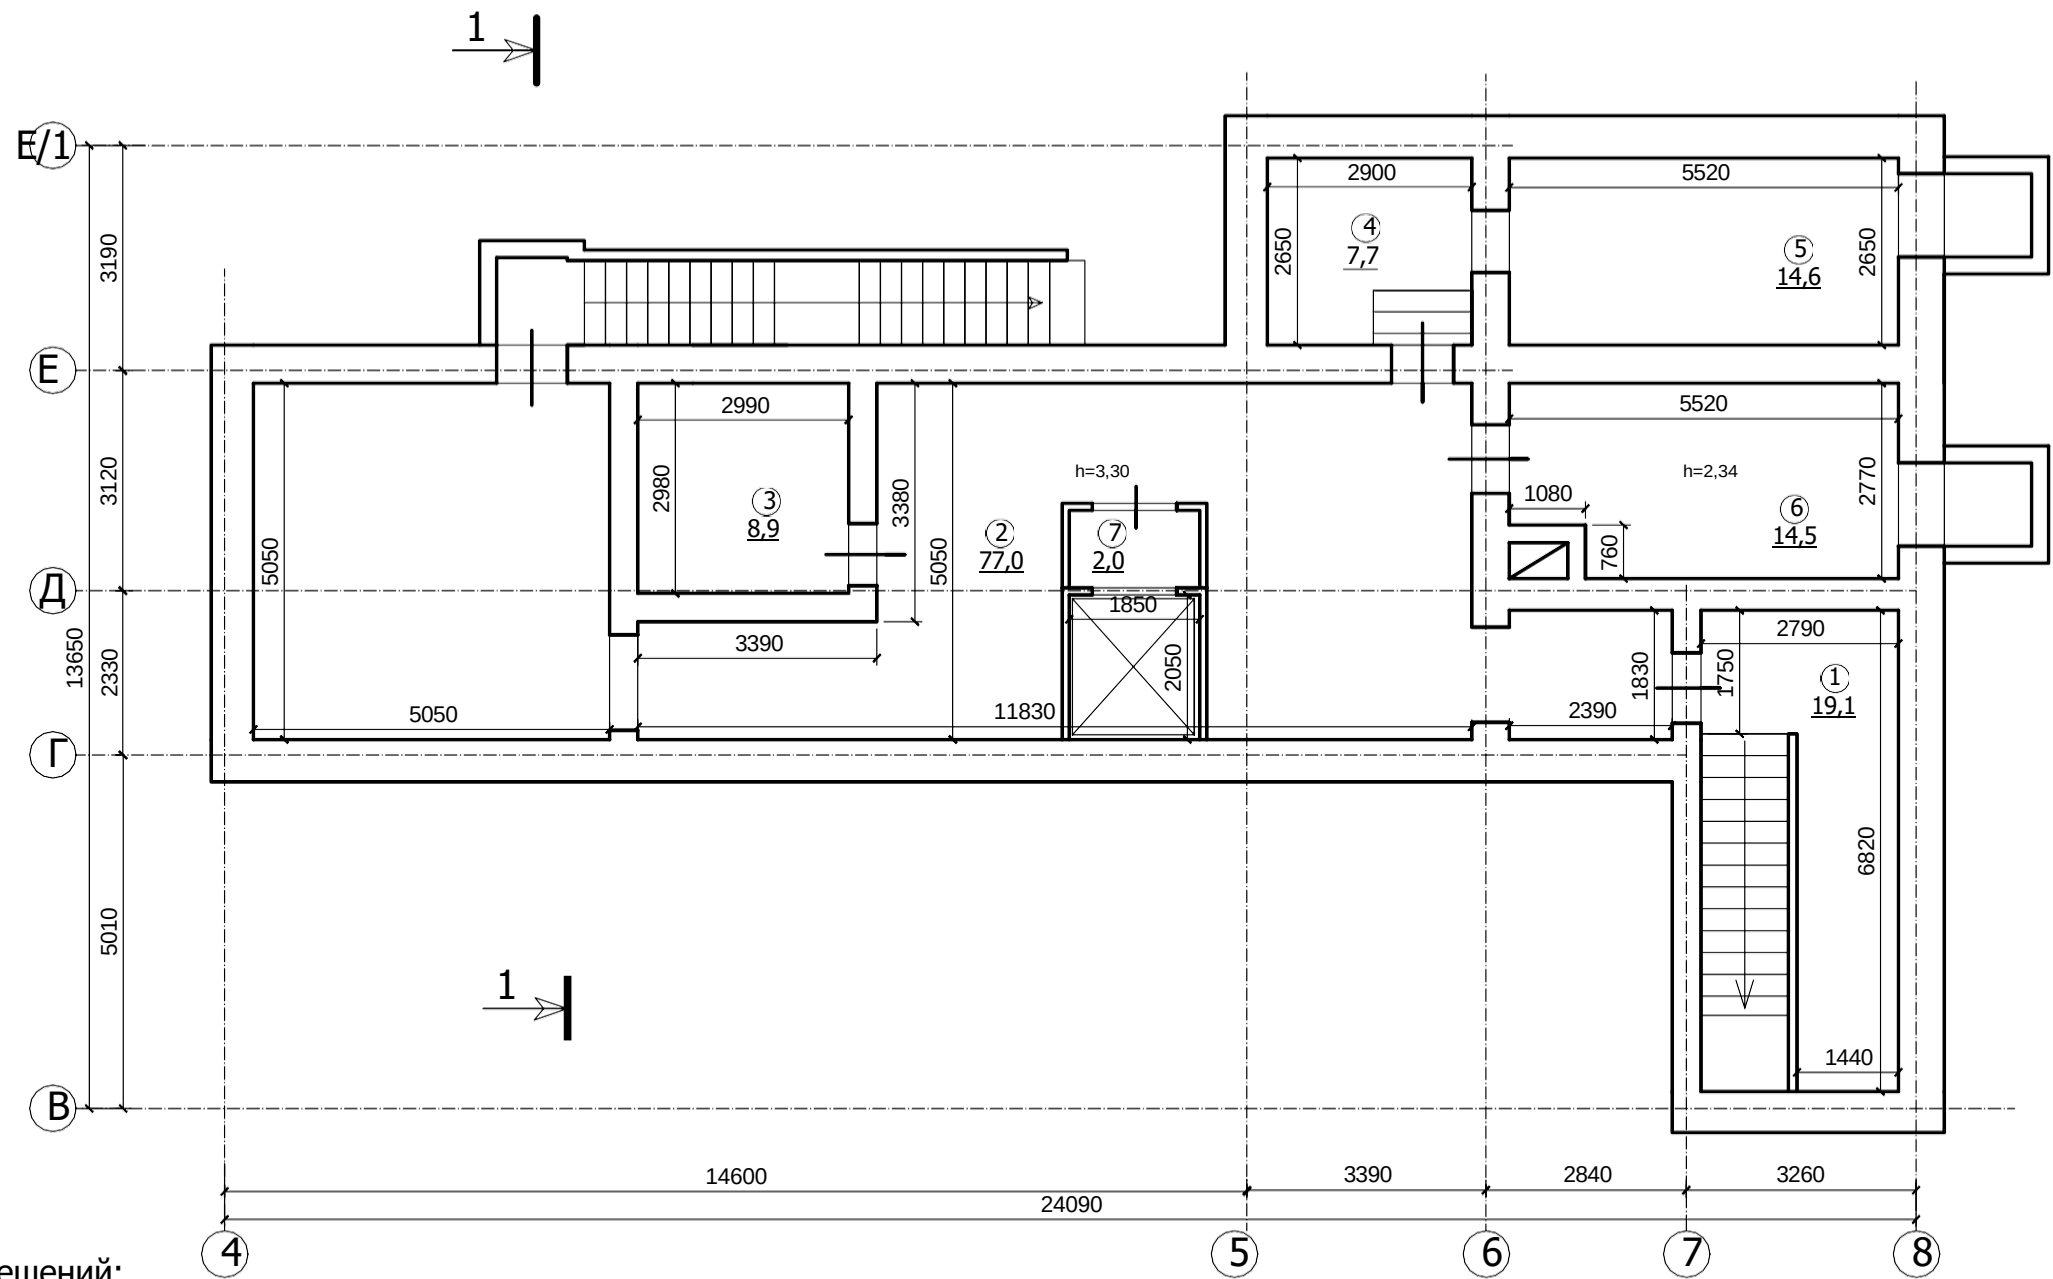

Экспликация помещений:

№ по плану	Помещение	Площадь м2
1	Помещение	19,1
2	Коридор	77,0
3	Помещение	8,9
4	Помещение	7,7
5	Помещение	14,6
6	Помещение	14,5
7	Тамбур	2,0
Итого:		143,7
Общая площадь этажа		168,5

						Заказчик: ИП							Шифр: П 29/0824		
						Адрес: : Российская Федерация, Московская область, Люберецкий р-н, рп Малаховка, ул Чайковского,д1									
Изм.	Кол. уч.	Лист	№ док.	Подп.	Дата	Проект реконструкции административного здания							Стадия	Лист	Листов
Ген. дер.													П	11	
ГАП															
ГИП															
						План подвала после реконструкции М 1:100							ООО ПСК "СЕРВИС"		


Копировал

А3

Согласовано
Уд. ? под. Подп. и дата
Инв. ?


Экспликация помещений:

№ по плану		Площадь м2
1	Вестибюль	268,5
2	Лестничная клетка	15,1
3	Помещение	64,6
4	Помещение	24,7
5	Помещение	25,2
6	Помещение	37,6
7	Помещение	63,3
8	Лестничная клетка	10,8
9	Тамбур	4,2
10	Помещение	1,5
Итого:		515,5
Общая площадь этажа		567,5

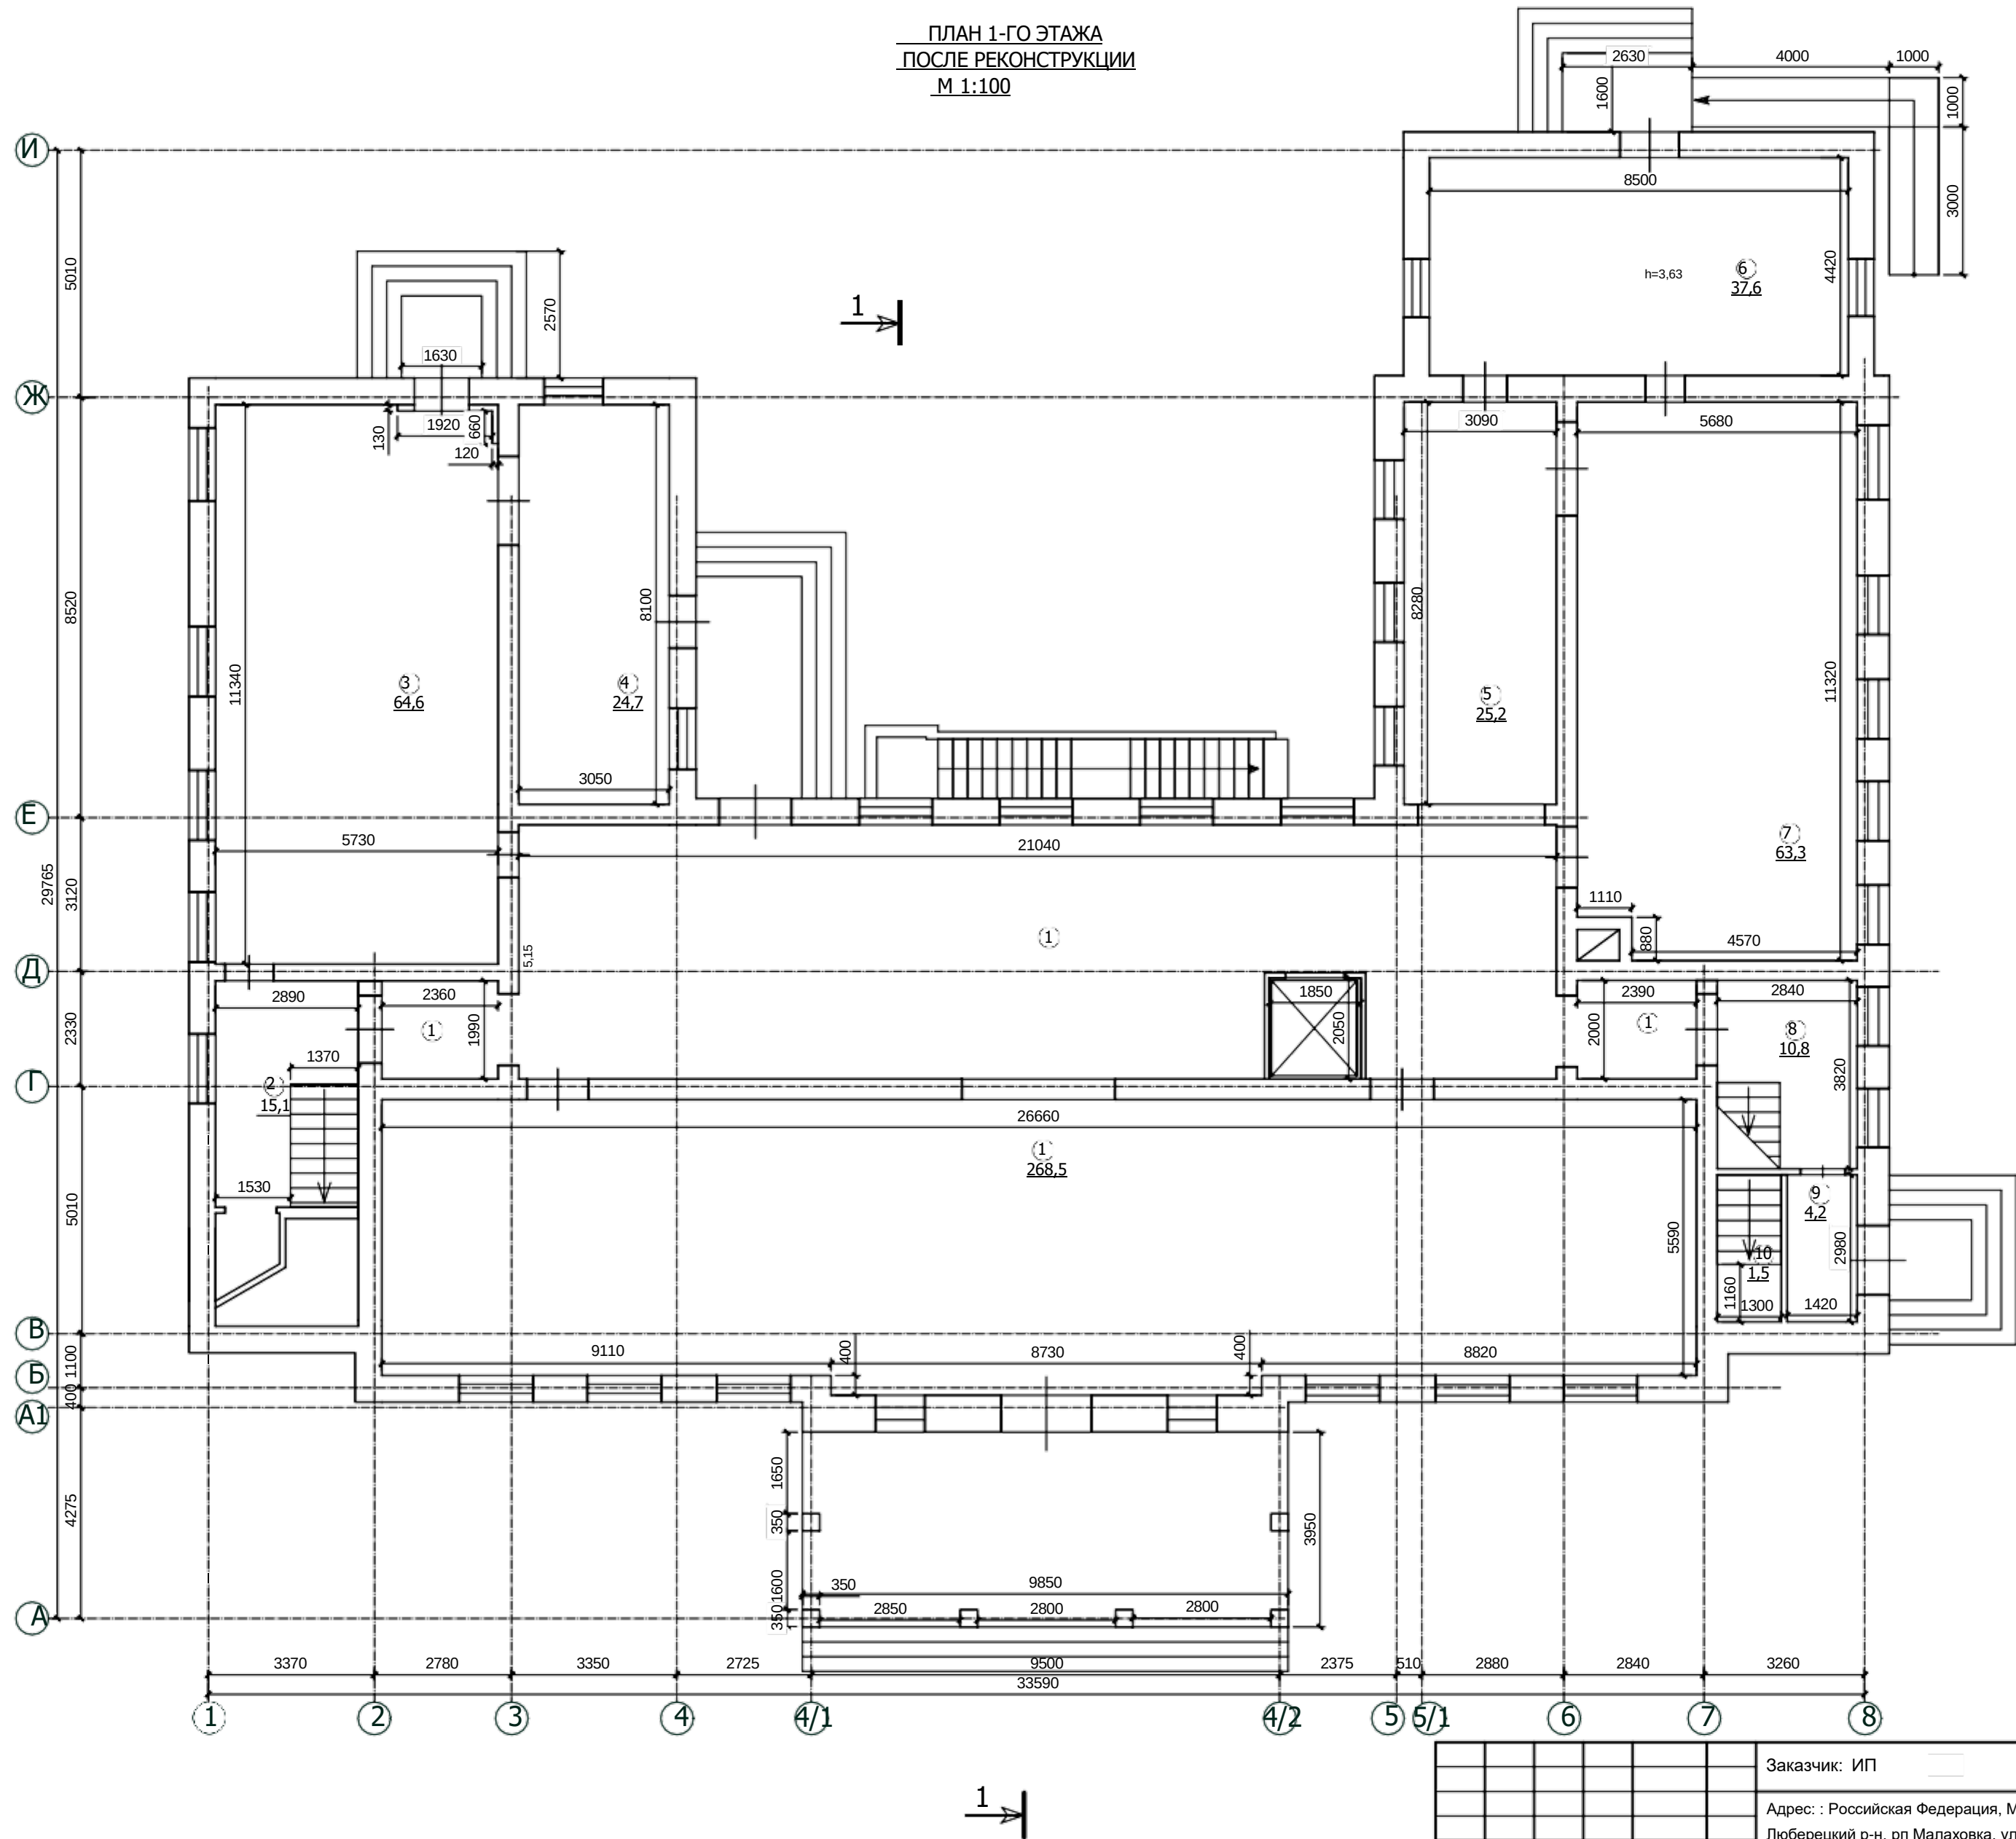

						Заказчик: ИП				Шифр: П 29/0824			
						Адрес: : Российская Федерация, Московская область, Люберецкий р-н, рп Малаховка, ул Чайковского,д1							
Изм.	Кол. уч.	Лист	№ док.	Подп.	Дата	Проект реконструкции административного здания				Стадия	Лист	Листов	
Ген. дер.										П	12		
ГАП													
ГИП													
						План 1-го этажа после реконструкции М 1:100				ООО ПСК "СЕРВИС"			

ПЛАН 2-ГО ЭТАЖА
ПОСЛЕ РЕКОНСТРУКЦИИ
М 1:100

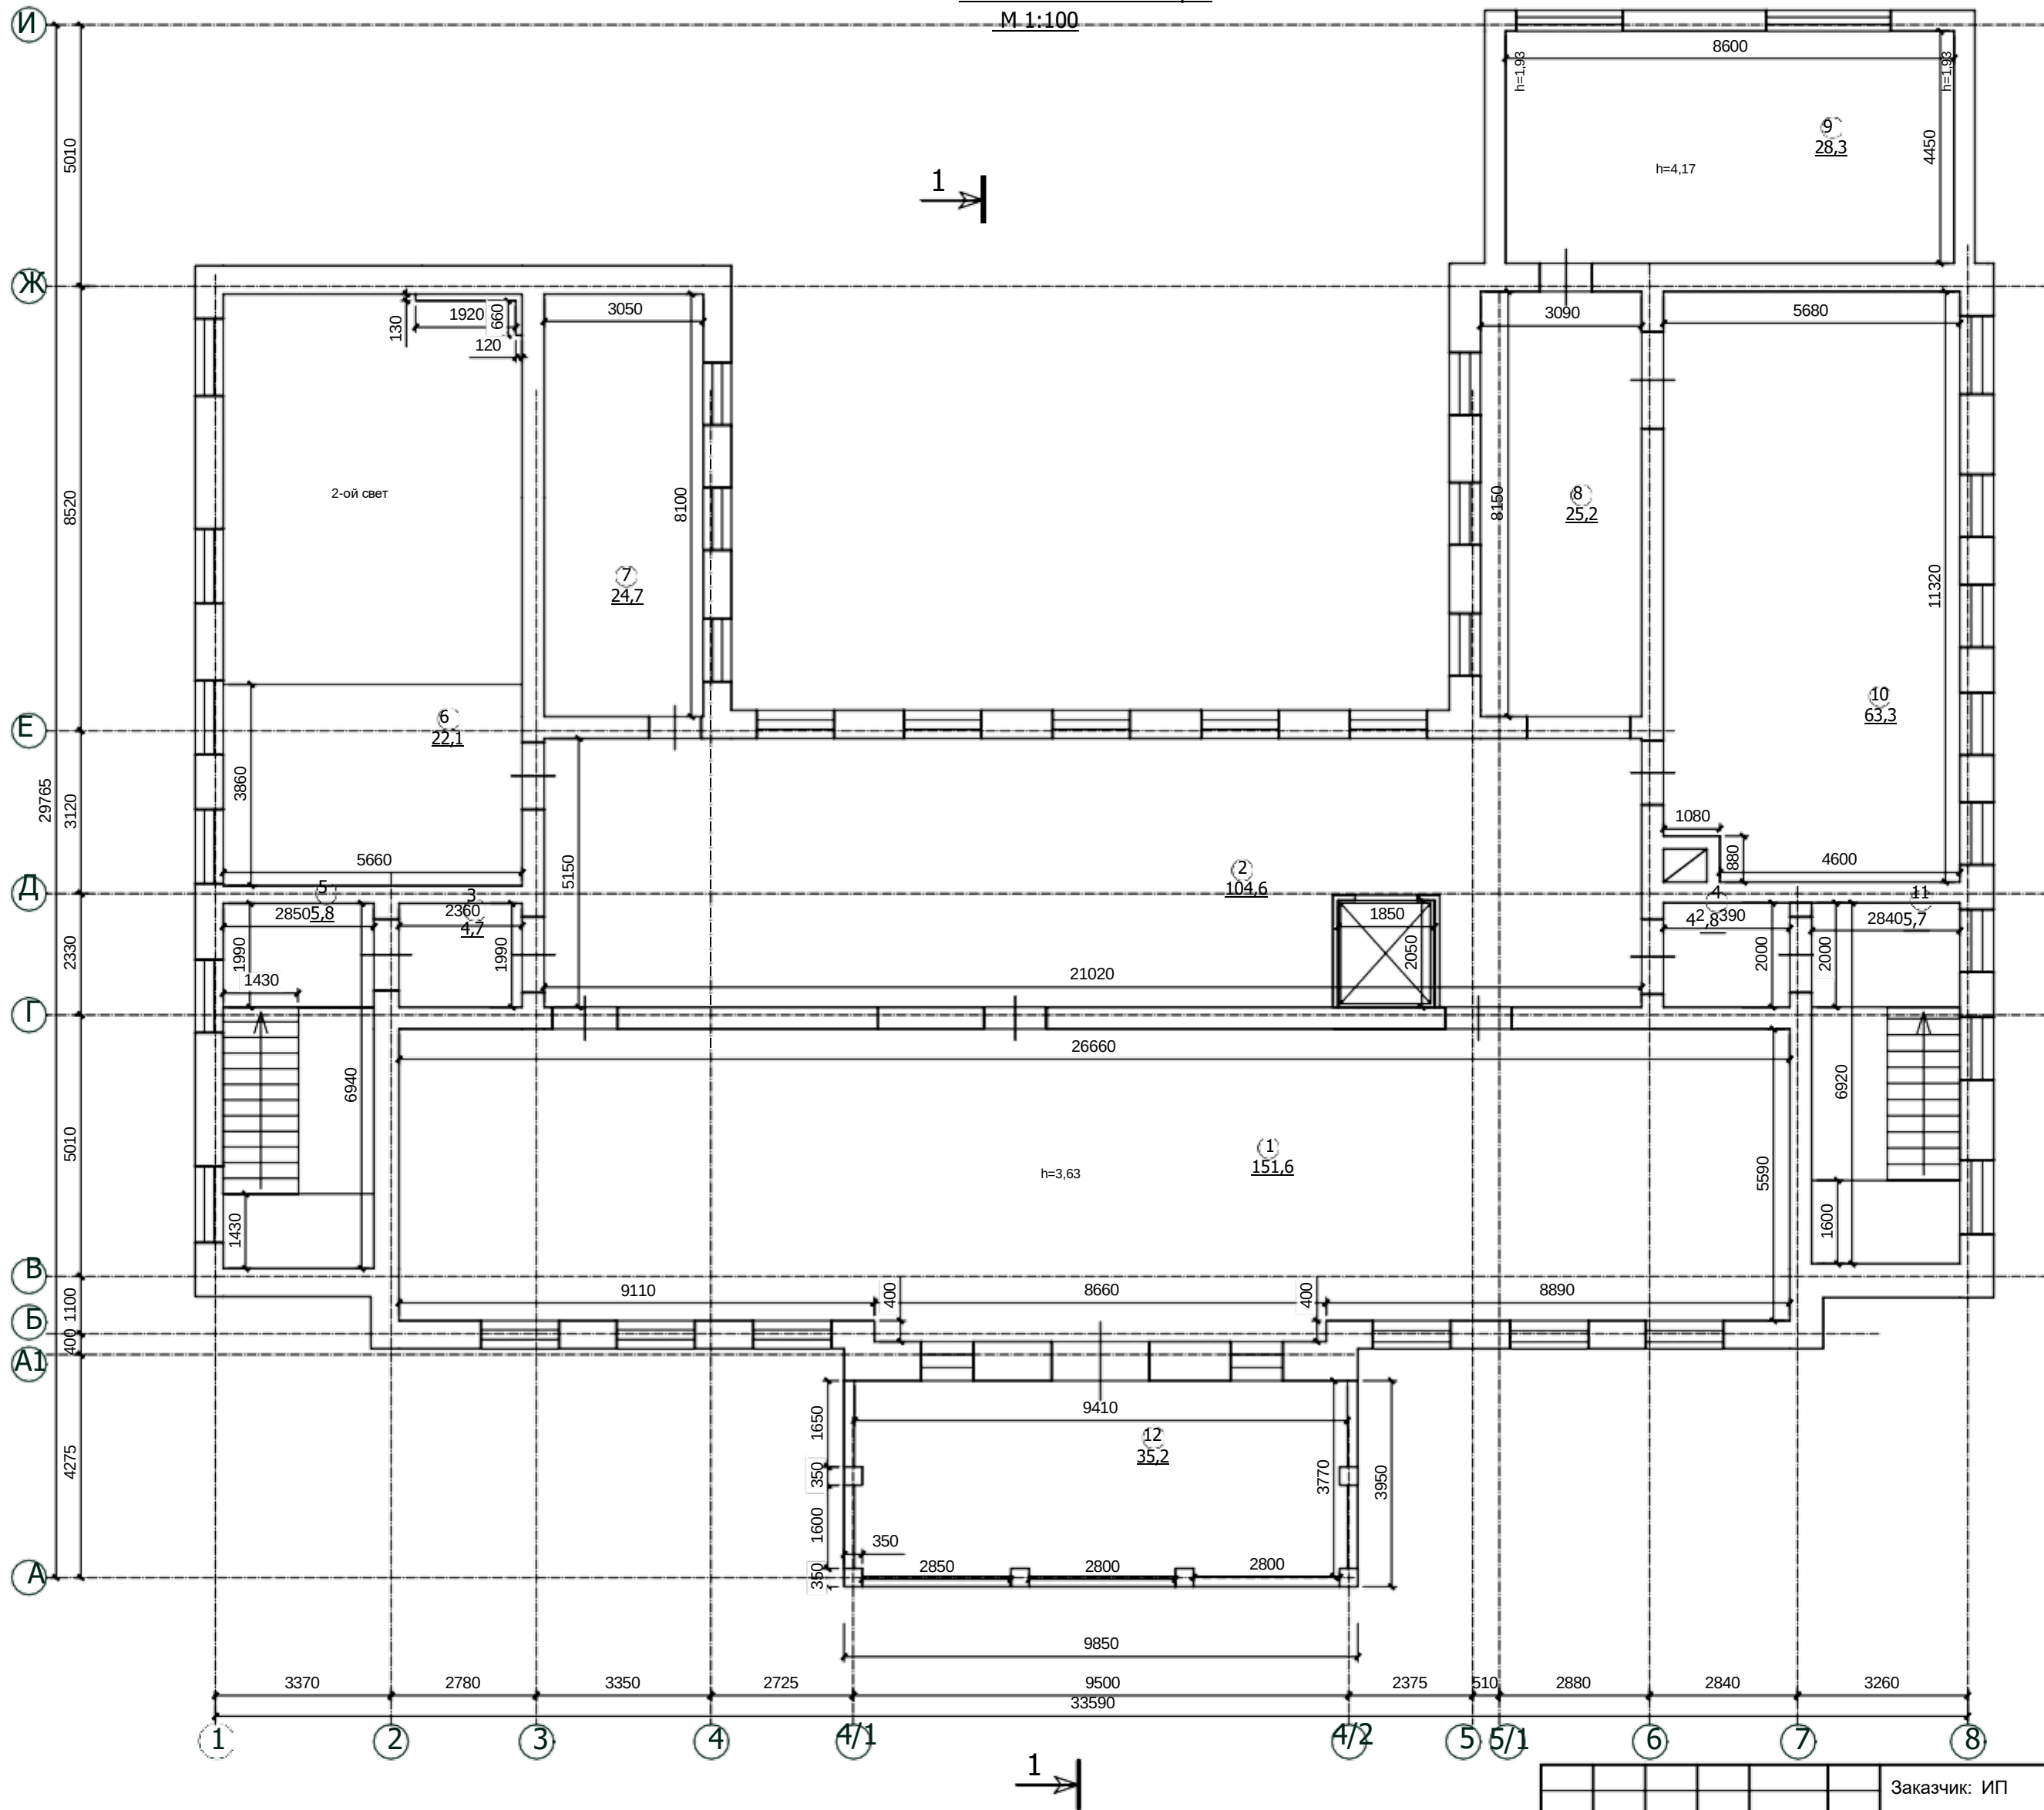

Экспликация помещений:

№ по плану		Площадь м2
1	Вестибюль	151,6
2	Вестибюль	104,6
3	Коридор	4,7
4	Коридор	4,8
5	Лестничная клетка	5,8
6	Помещение	22,1
7	Помещение	24,7
8	Помещение	25,2
9	Помещение	38,3
10	Помещение	63,3
11	Лестничная клетка	5,7
12	Помещение	35,2
	Итого:	486,0
	Общая площадь этажа	570,5


						Заказчик: ИП				Шифр: П 29/0824		
						Адрес: : Российская Федерация, Московская область, Люберецкий р-н, рп Малаховка, ул Чайковского,д1						
Изм.	Кол. уч.	Лист	№ док.	Подп.	Дата							
Ген. дер.						Проект реконструкции административного здания				Стадия	Лист	Листов
ГАП										П	13	
ГИП						План 2-го этажа после реконструкции М 1:100				ООО ПСК "СЕРВИС"		
			</									

Согласовано

И.п. ? подп. И.п. ?

Подп. и дата


ПЛАН МАНСАРДЫ
ПОСЛЕ РЕКОНСТРУКЦИИ
М 1:100

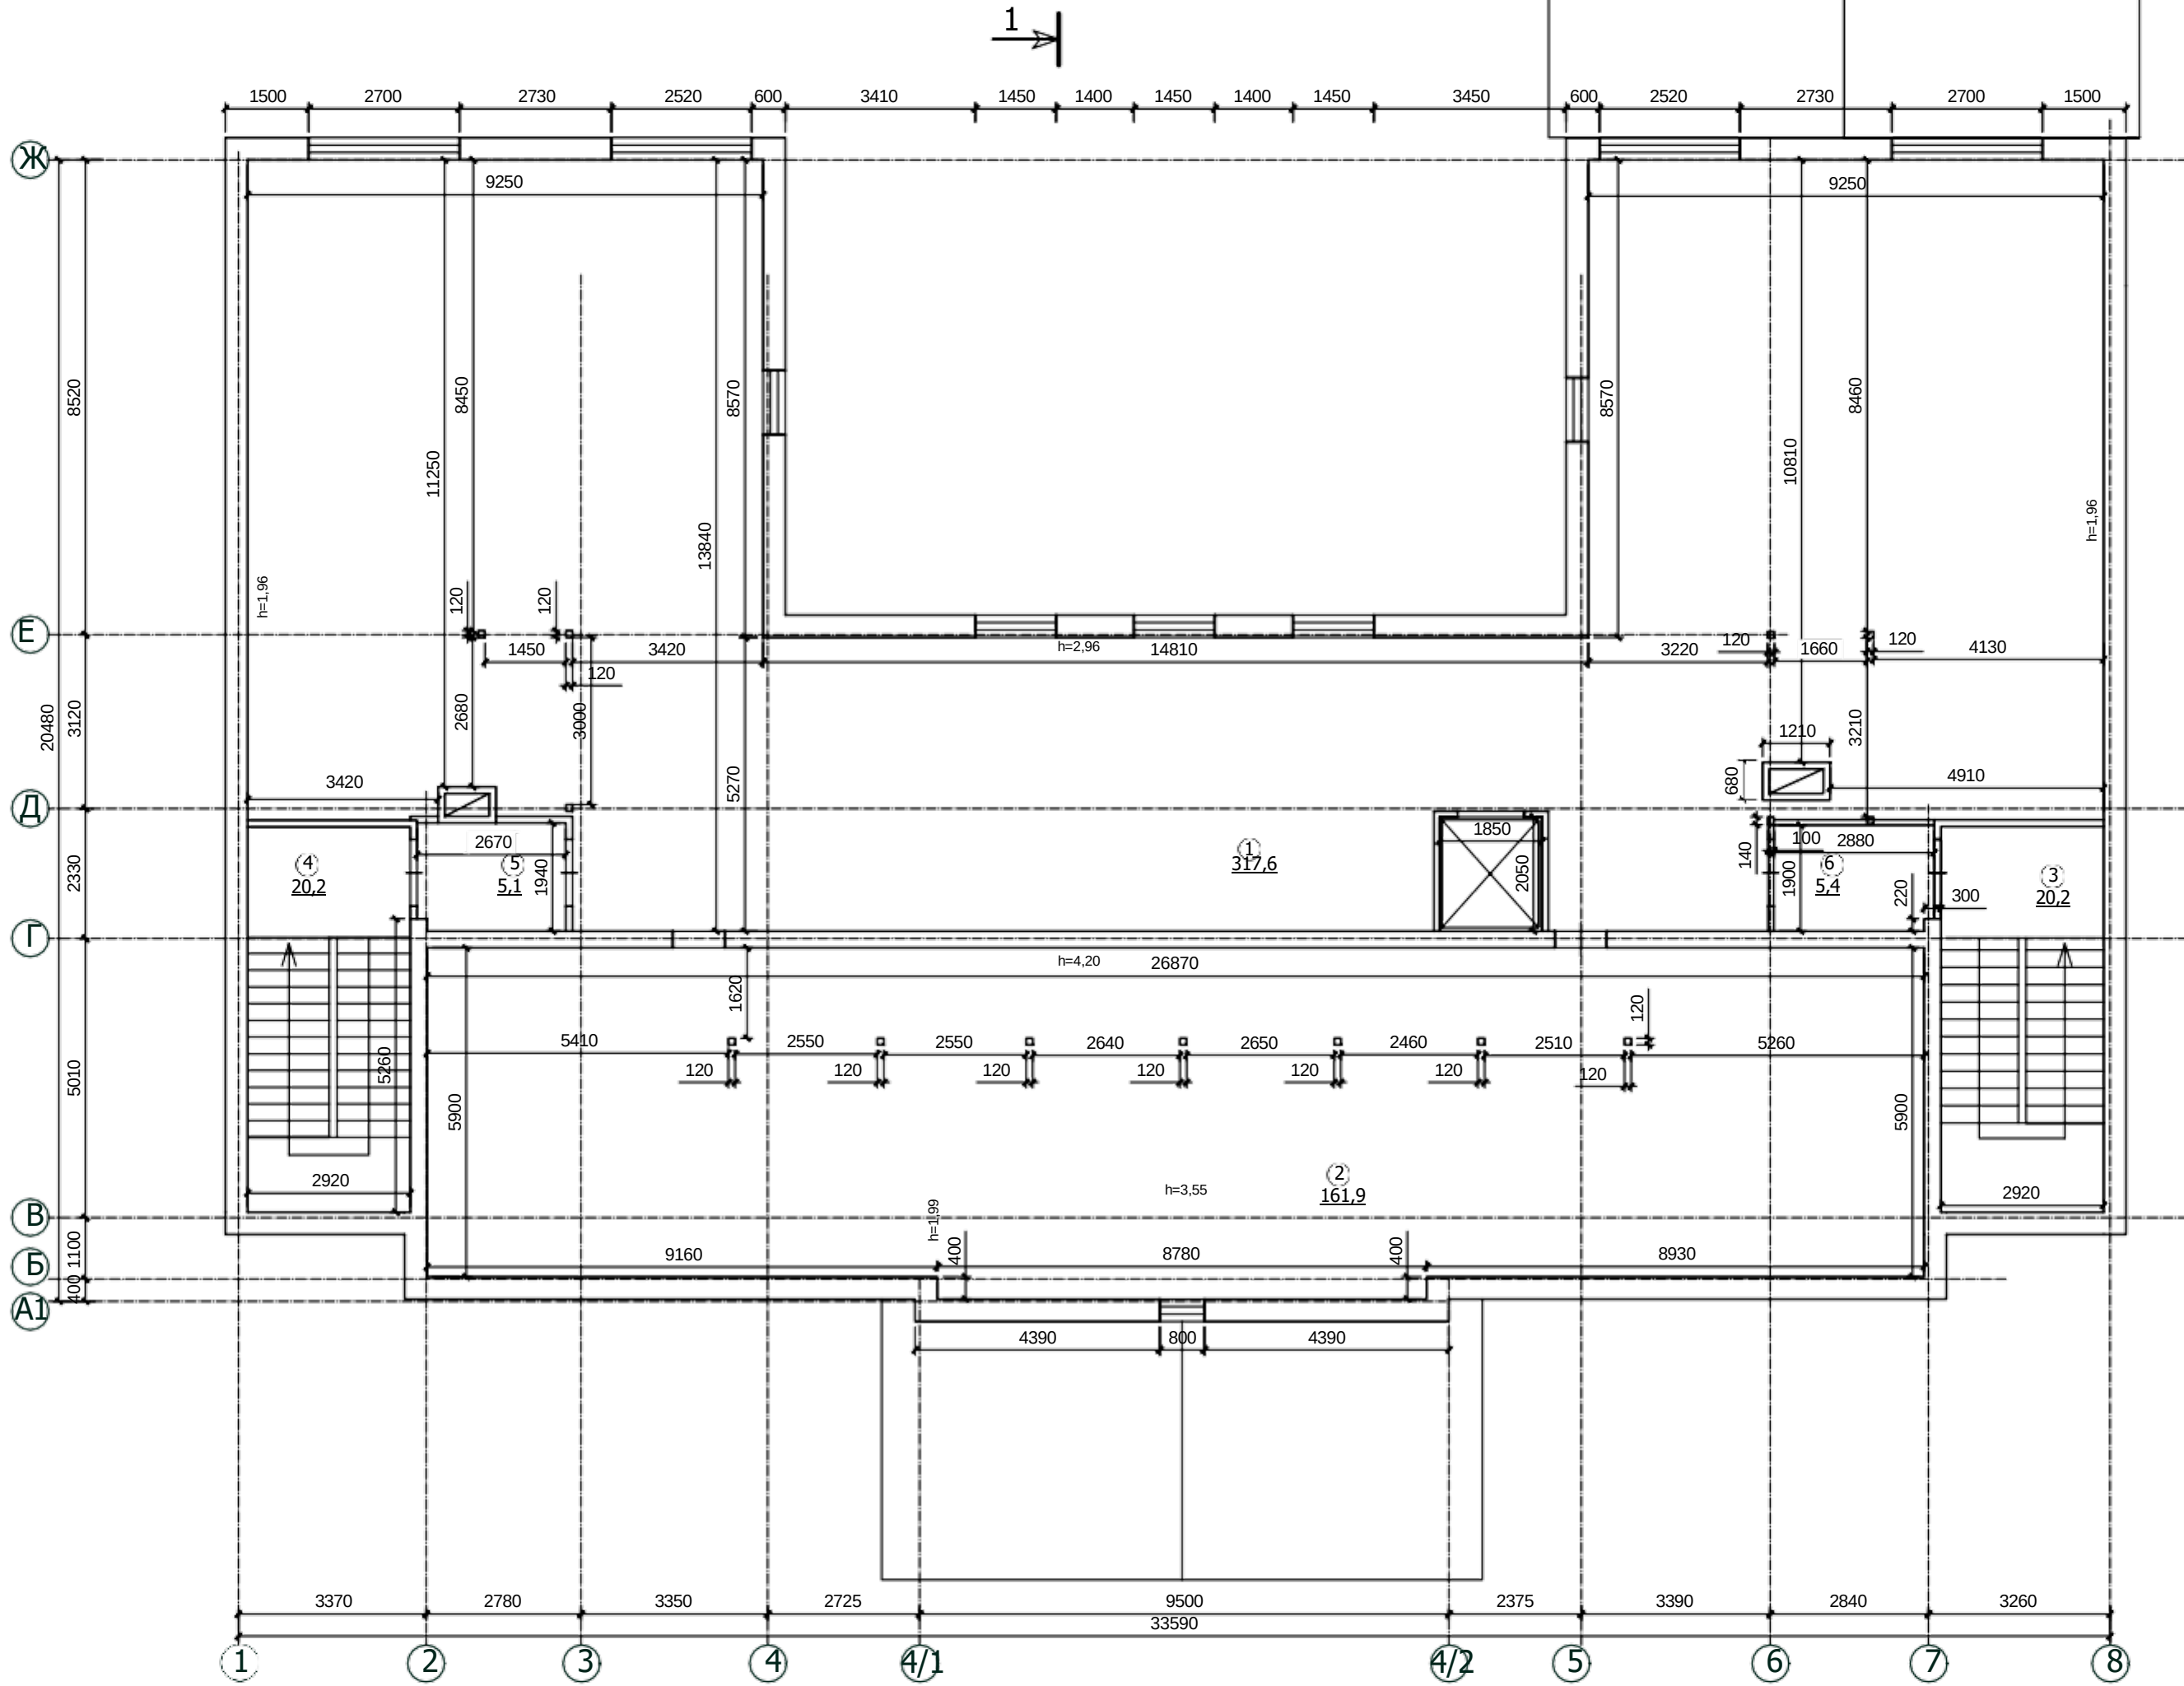


Экспликация помещений:

№ по плану	Помещение	Площадь м2
1	Помещение	307,1
2	Помещение	161,9
3	Лестничная клетка	20,2
4	Лестничная клетка	20,2
5	Коридор	5,1
6	Коридор	5,4
Итого:		519,9
Общая площадь этажа		536,6

							Заказчик: ИП				Шифр: П 29/0824		
							Адрес: : Российская Федерация, Московская область, Люберецкий р-н, рп Малаховка, ул Чайковского,д1						
Изм.	Кол. уч.	Лист	№ док.	Подп.	Дата								
Ген. дер.							Проект реконструкции административного здания				Стадия	Лист	Листов
ГАП											П	14	
ГИП							План мансарды после реконструкции М 1:100				ООО ПСК "СЕРВИС"		

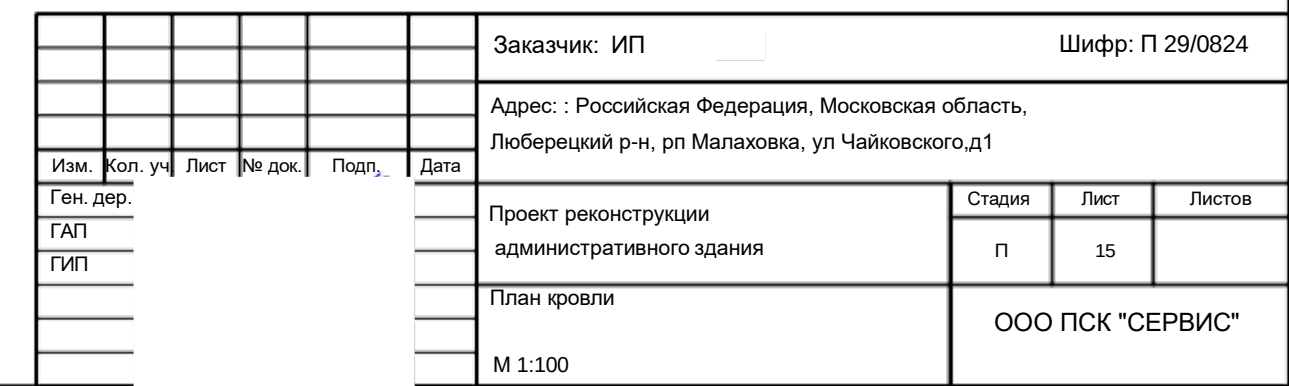[illegible]

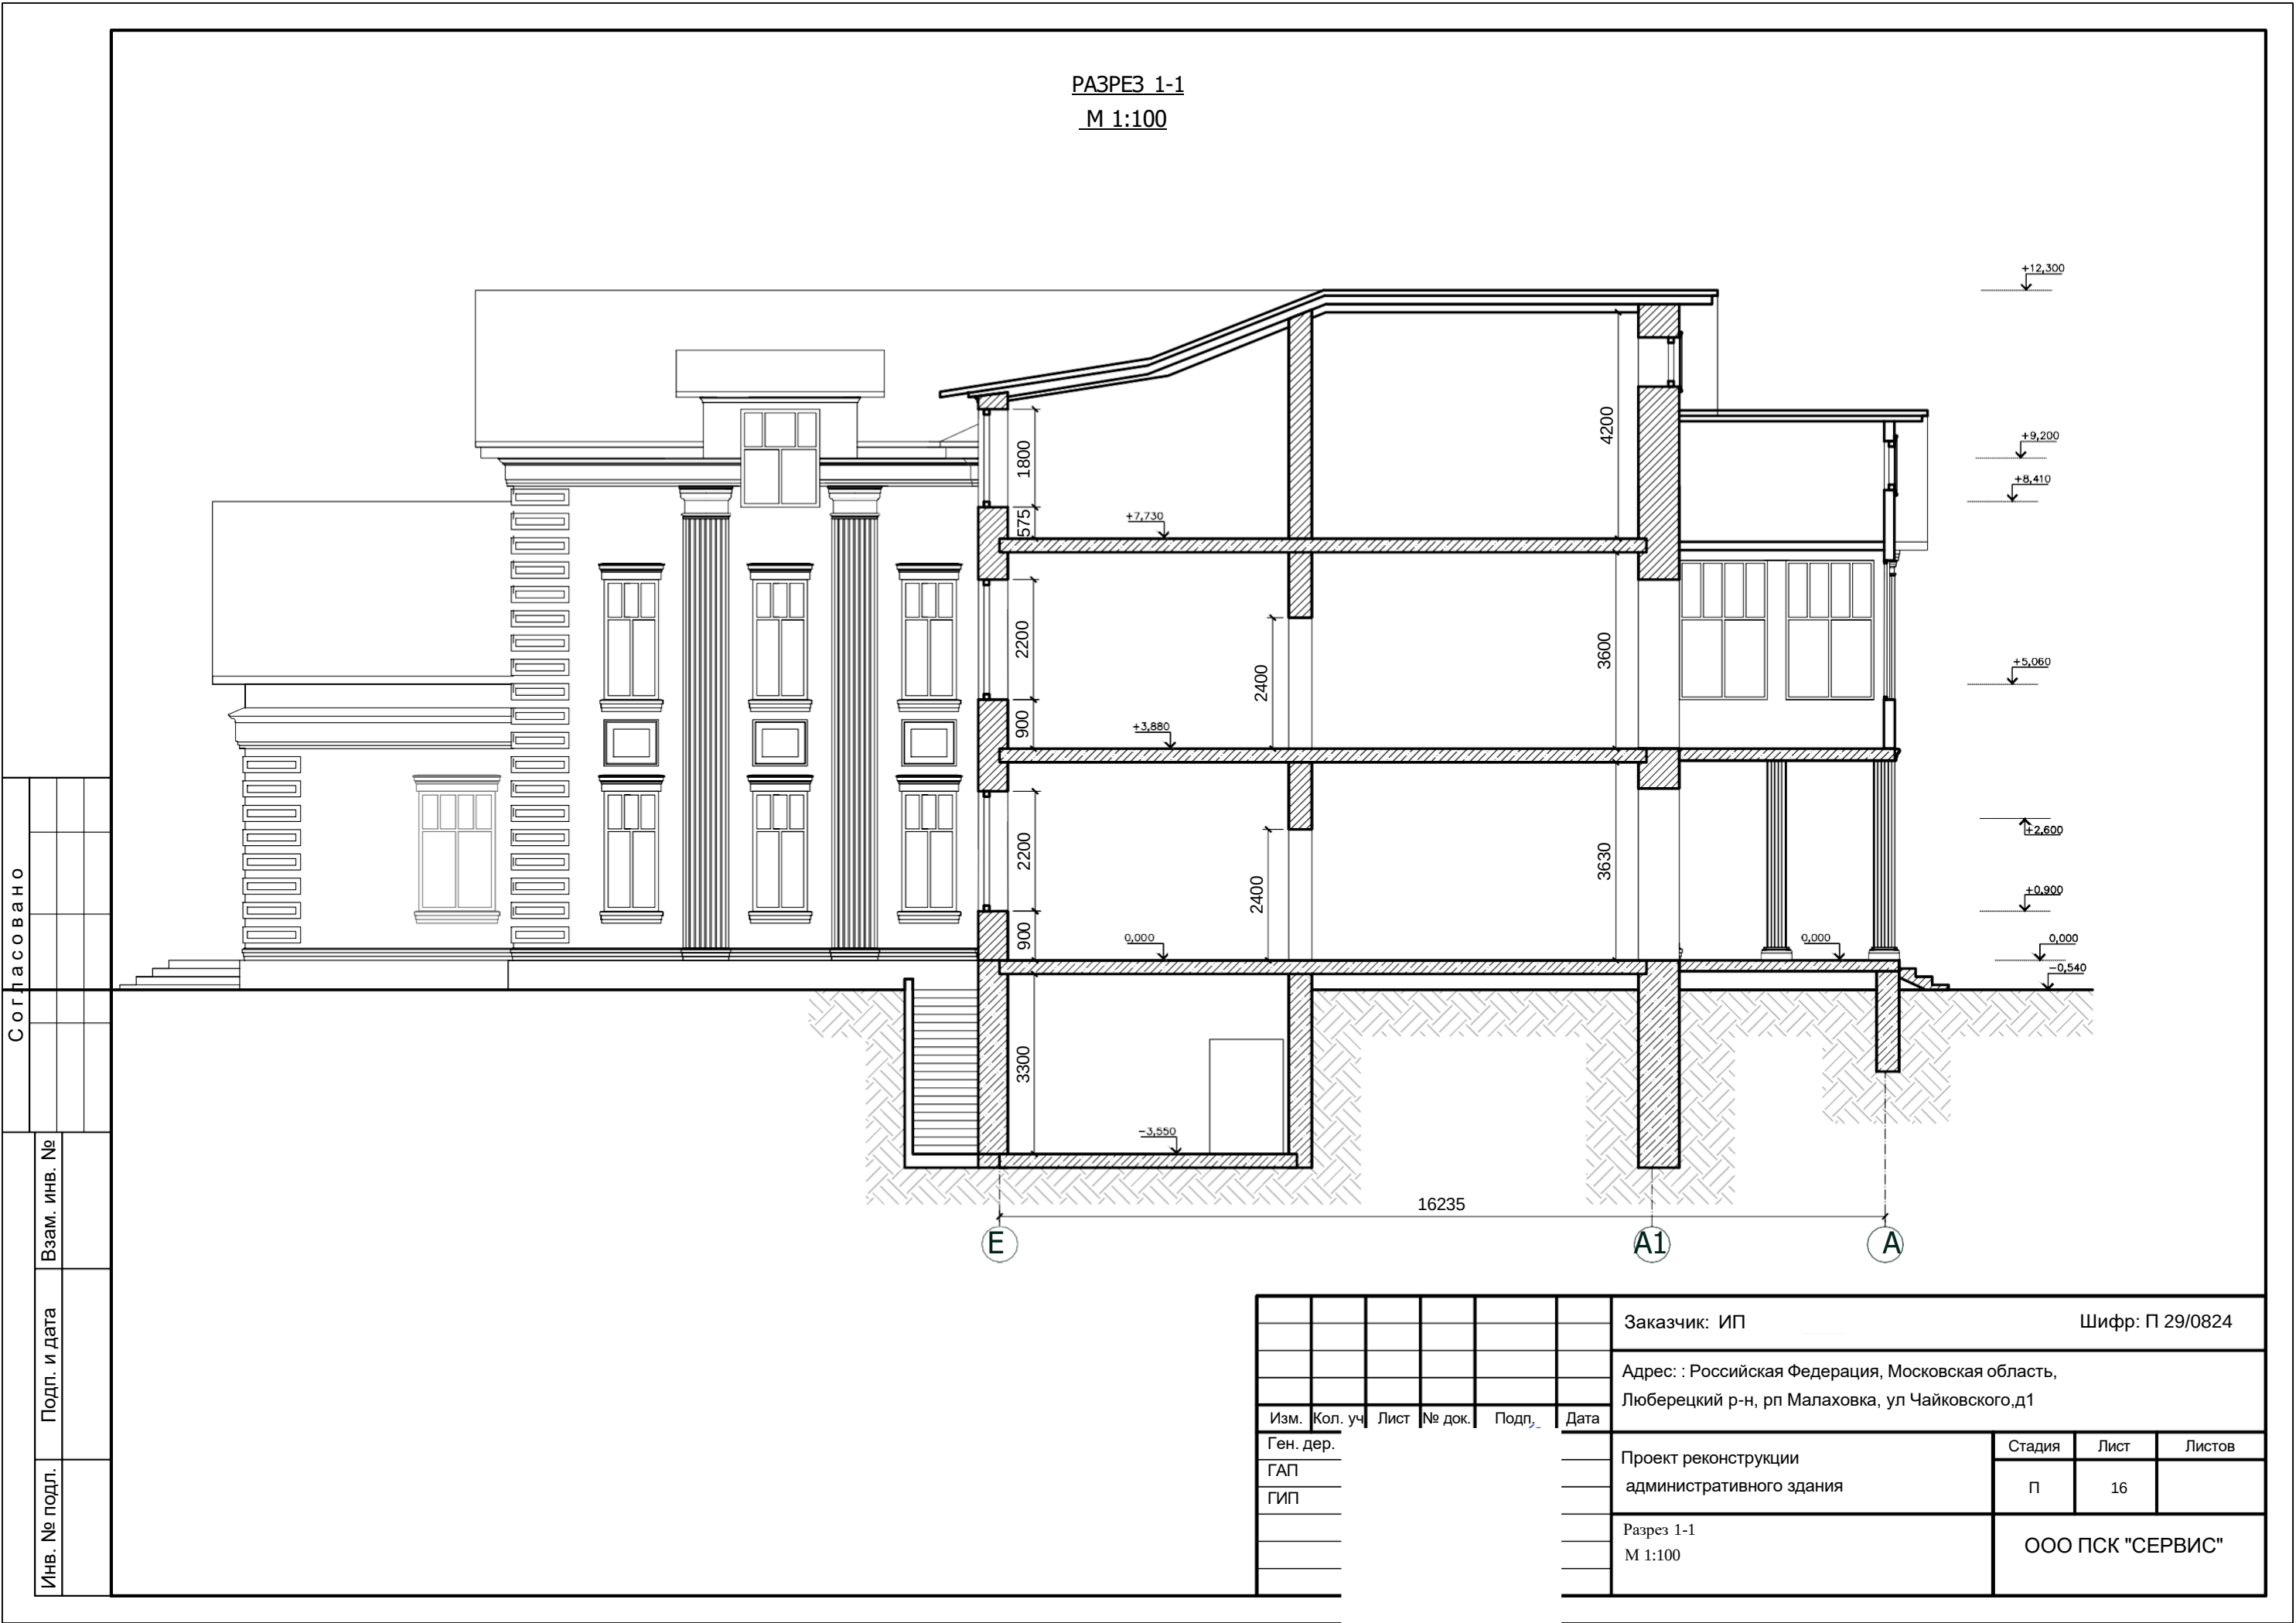

ФАСАД В ОСЯХ 1-8
М 1:100



			Согласовано	
Инв. № подл.	Подп. и дата	Взам. инв. №		

						Заказчик: ИП				Шифр: П 29/0824			
						Адрес: : Российская Федерация, Московская область, Люберецкий р-н, рп Малаховка, ул Чайковского,д1							
Изм.	Кол. уч	Лист	№ док.	Подп.	Дата	Проект реконструкции административного здания				Стадия	Лист	Листов	
Ген. дер.										П	17		
ГАП													
ГИП													
						Фасад в осях 1-8 М 1:100				ООО ПСК "СЕРВИС"			

Согласовано

Взам. инв. №

Подп. и дата

Инв. № подл.

ФАСАД В ОСЯХ 8-1
М 1:100



						Заказчик: ИП				Шифр: П 29/0824		
						Адрес: : Российская Федерация, Московская область, Люберецкий р-н, рп Малаховка, ул Чайковского,д1						
Изм.	Кол. уч.	Лист	№ док.	Подп.	Дата	Проект реконструкции административного здания				Стадия	Лист	Листов
Ген. дер.										П	18	
ГАП						Фасад в осях 8-1 М 1:100				ООО ПСК "СЕРВИС"		
ГИП												

ФАСАД В ОСЯХ А-И
М 1:100




						Заказчик: ИП				Шифр: П 29/0824		
						Адрес: : Российская Федерация, Московская область, Люберецкий р-н, рп Малаховка, ул Чайковского,д1						
Изм.	Кол. уч.	Лист	№ док.	Подп.	Дата	Проект реконструкции административного здания				Стадия	Лист	Листов
Ген. дер.										П	19	
ГАП												
ГИП						Фасад в осях А-И М 1:100				ООО ПСК "СЕРВИС"		

ФАСАД В ОСЯХ И-А
М 1:100



						Заказчик: ИП				Шифр: П 29/0824		
						Адрес: : Российская Федерация, Московская область, Люберецкий р-н, рп Малаховка, ул Чайковского,д1						
Изм.	Кол. уч	Лист	№ док.	Подп.	Дата	Проект реконструкции административного здания				Стадия	Лист	Листов
Ген. дер.										П	20	
ГАП										ООО ПСК "СЕРВИС"		
ГИП						Фасад в осях И-А М 1:100						

ФАСАД В ОСЯХ 1-8
М 1:100

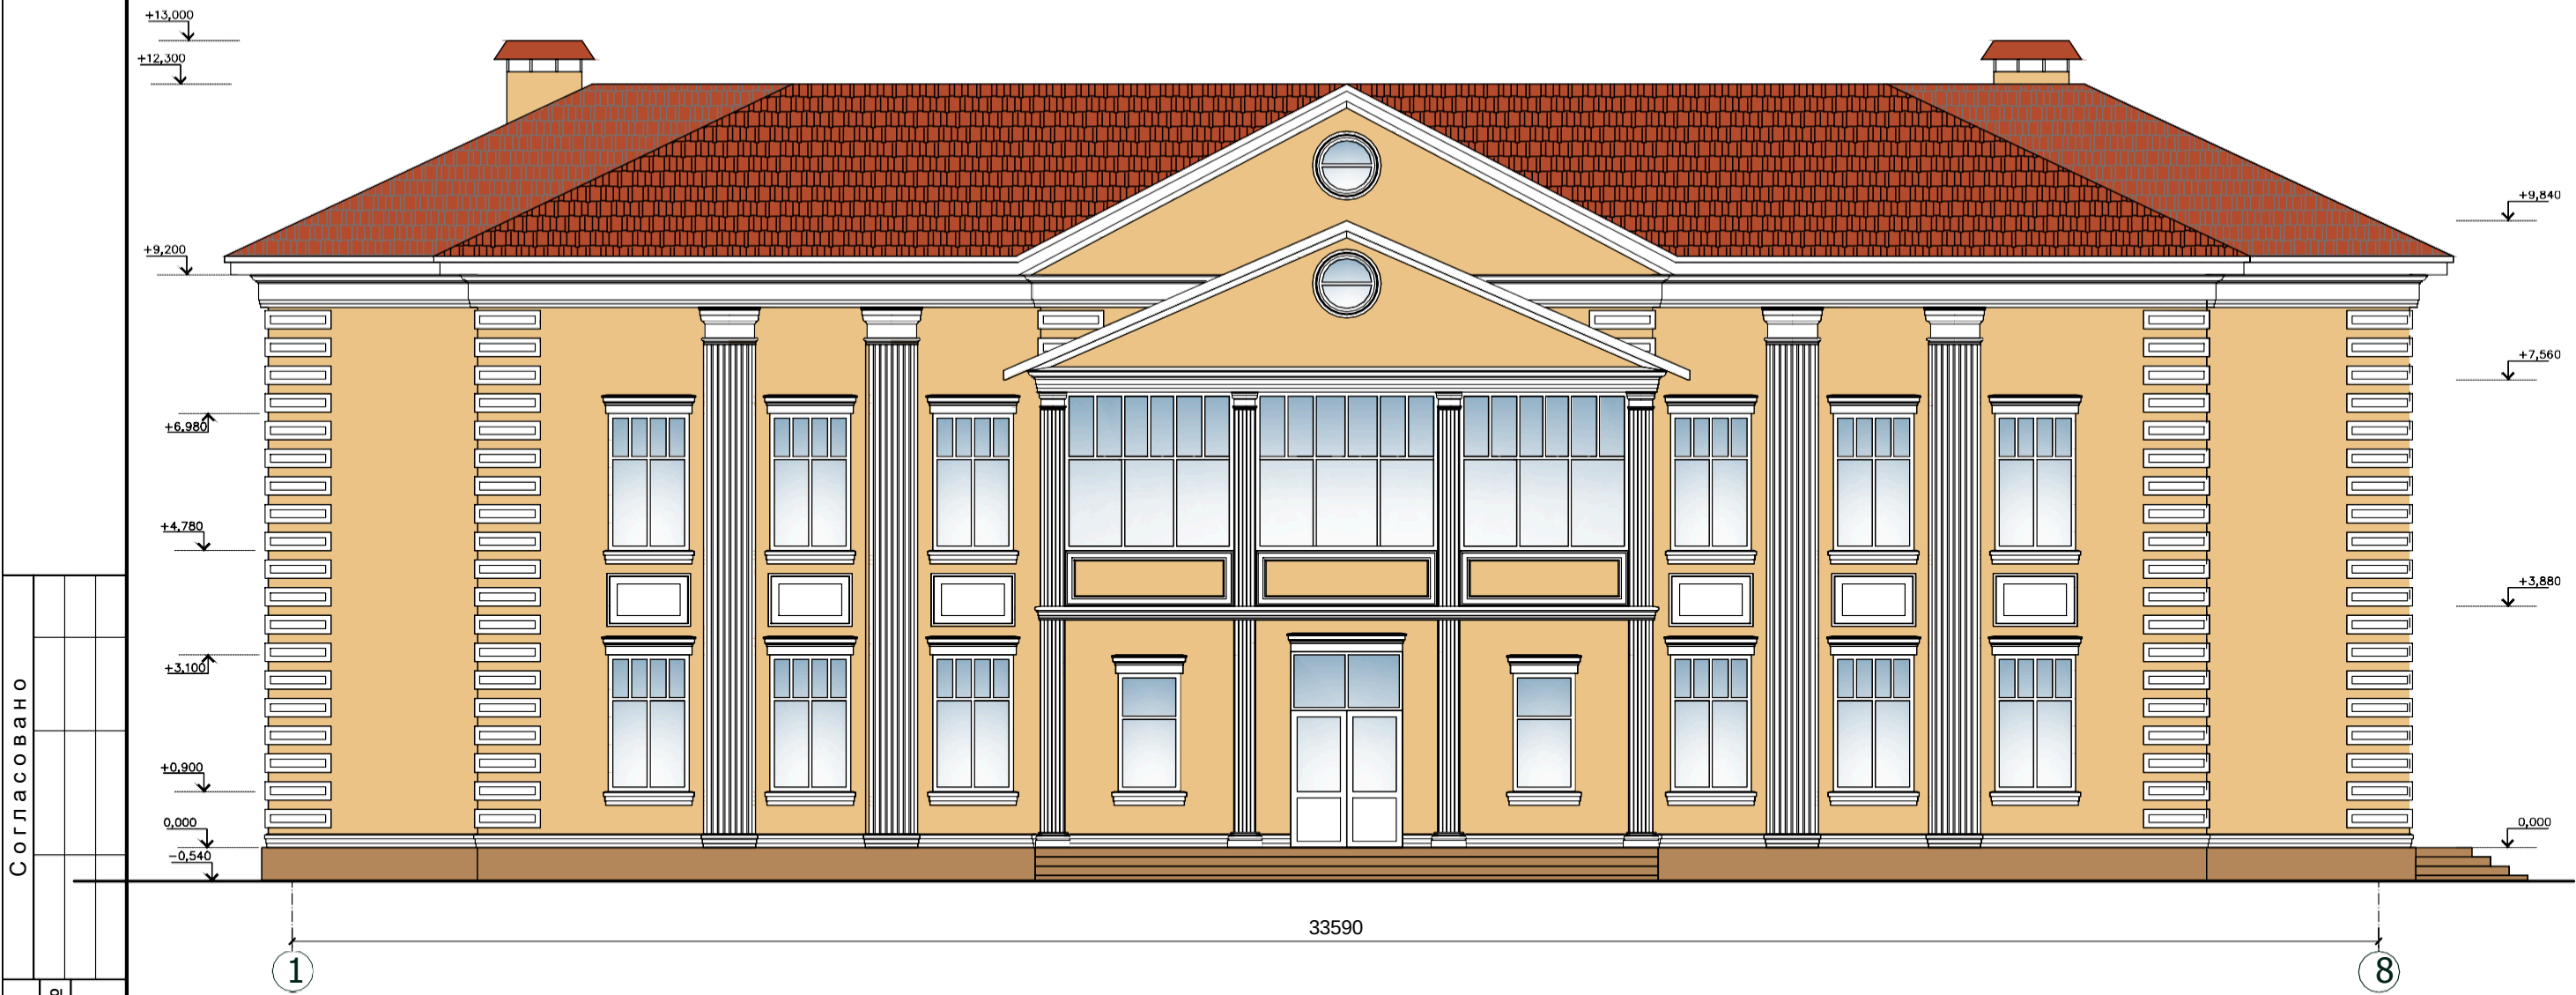

Согласовано					
Изм.	Кол. уч.	Лист	№ док.	Подп.	Дата
Ген. дер.					
ГАП					
ГИП					
Инв. № подл.	Подп. и дата	Взам. инв. №			

Заказчик: ИП						Шифр: П 29/0824		
Адрес: : Российская Федерация, Московская область, Люберецкий р-н, рп Малаховка, ул Чайковского,д1								
Проект реконструкции административного здания						Стадия	Лист	Листов
						П	21	
Фасад в осях 1-8 Цветовое решение М 1:100						ООО ПСК "СЕРВИС"		

Согласовано

Взам. инв. №

Подп. и дата

Инв. № подл.

ФАСАД В ОСЯХ 8-1
М 1:100



						Заказчик: ИП				Шифр: П 29/0824		
						Адрес: : Российская Федерация, Московская область, Люберецкий р-н, рп Малаховка, ул Чайковского,д1						
Изм.	Кол. уч.	Лист	№ док.	Подп.	Дата							
Ген. дер.						Проект реконструкции административного здания				Стадия	Лист	Листов
ГАП										П	22	
ГИП						Фасад в осях 8-1 Цветовое решение М 1:100				ООО ПСК "СЕРВИС"		

ФАСАД В ОСЯХ А-И
М 1:100



						Заказчик: ИП				Шифр: П 29/0824		
						Адрес: : Российская Федерация, Московская область, Люберецкий р-н, рп Малаховка, ул Чайковского,д1						
Изм.	Кол. уч.	Лист	№ док.	Подп.	Дата	Проект реконструкции административного здания				Стадия	Лист	Листов
Ген. дер.										П	23	
ГАП						Фасад в осях А-И Цветовое решение М 1:100				ООО ПСК "СЕРВИС"		
ГИП												

ФАСАД В ОСЯХ И-А
М 1:100



						Заказчик: ИП				Шифр: П 29/0824		
						Адрес: : Российская Федерация, Московская область, Люберецкий р-н, рп Малаховка, ул Чайковского,д1						
Изм.	Кол. уч.	Лист	№ док.	Подп.	Дата	Проект реконструкции административного здания				Стадия	Лист	Листов
Ген. дер.										П	24	
ГАП						Фасад в осях И-А Цветовое решение М 1:100				ООО ПСК "СЕРВИС"		
ГИП												