


ПЛАН ПОДВАЛА
ПОСЛЕ РЕКОНСТРУКЦИИ
М 1:100

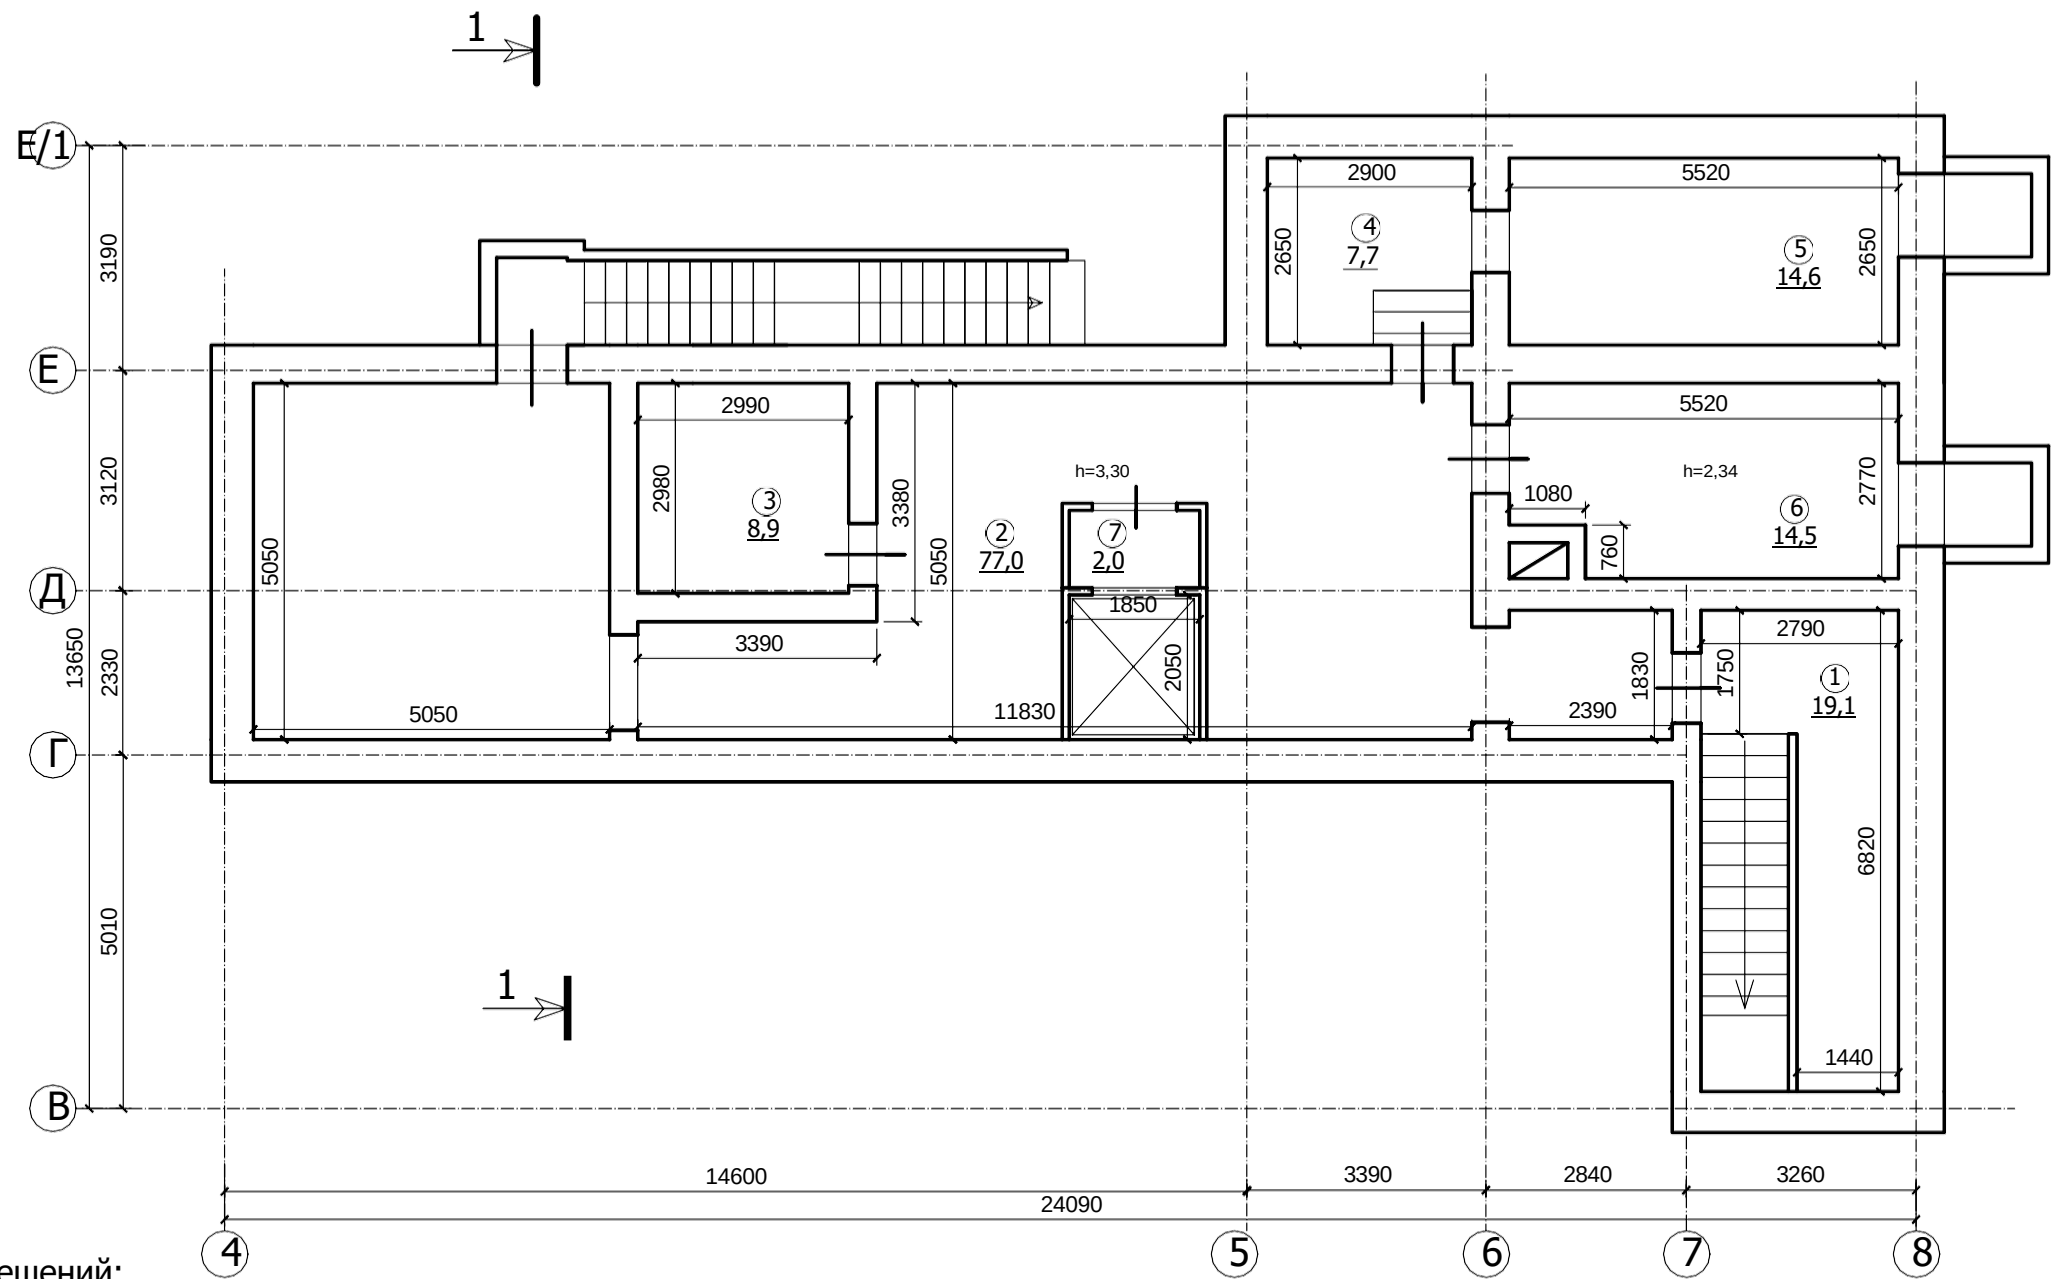

Экспликация помещений:

№ по плану	Помещение	Площадь м2
1	Помещение	19,1
2	Коридор	77,0
3	Помещение	8,9
4	Помещение	7,7
5	Помещение	14,6
6	Помещение	14,5
7	Тамбур	2,0
Итого:		143,7
Общая площадь этажа		168,5

						Заказчик: ИП							Шифр: П 29/0824		
						Адрес: : Российская Федерация, Московская область, Люберецкий р-н, рп Малаховка, ул Чайковского,д1									
Изм.	Кол. уч.	Лист	№ док.	Подп.	Дата	Проект реконструкции административного здания							Стадия	Лист	Листов
Ген. дер.													П	11	
ГАП															
ГИП															
						План подвала после реконструкции							ООО ПСК "СЕРВИС"		
						М 1:100									


Копировал

А3

Согласовано
Уд. ? под. Подп. и дата
Инв. ?


Экспликация помещений:

№ по плану		Площадь м2
1	Вестибюль	268,5
2	Лестничная клетка	15,1
3	Помещение	64,6
4	Помещение	24,7
5	Помещение	25,2
6	Помещение	37,6
7	Помещение	63,3
8	Лестничная клетка	10,8
9	Тамбур	4,2
10	Помещение	1,5
Итого:		515,5
Общая площадь этажа		567,5

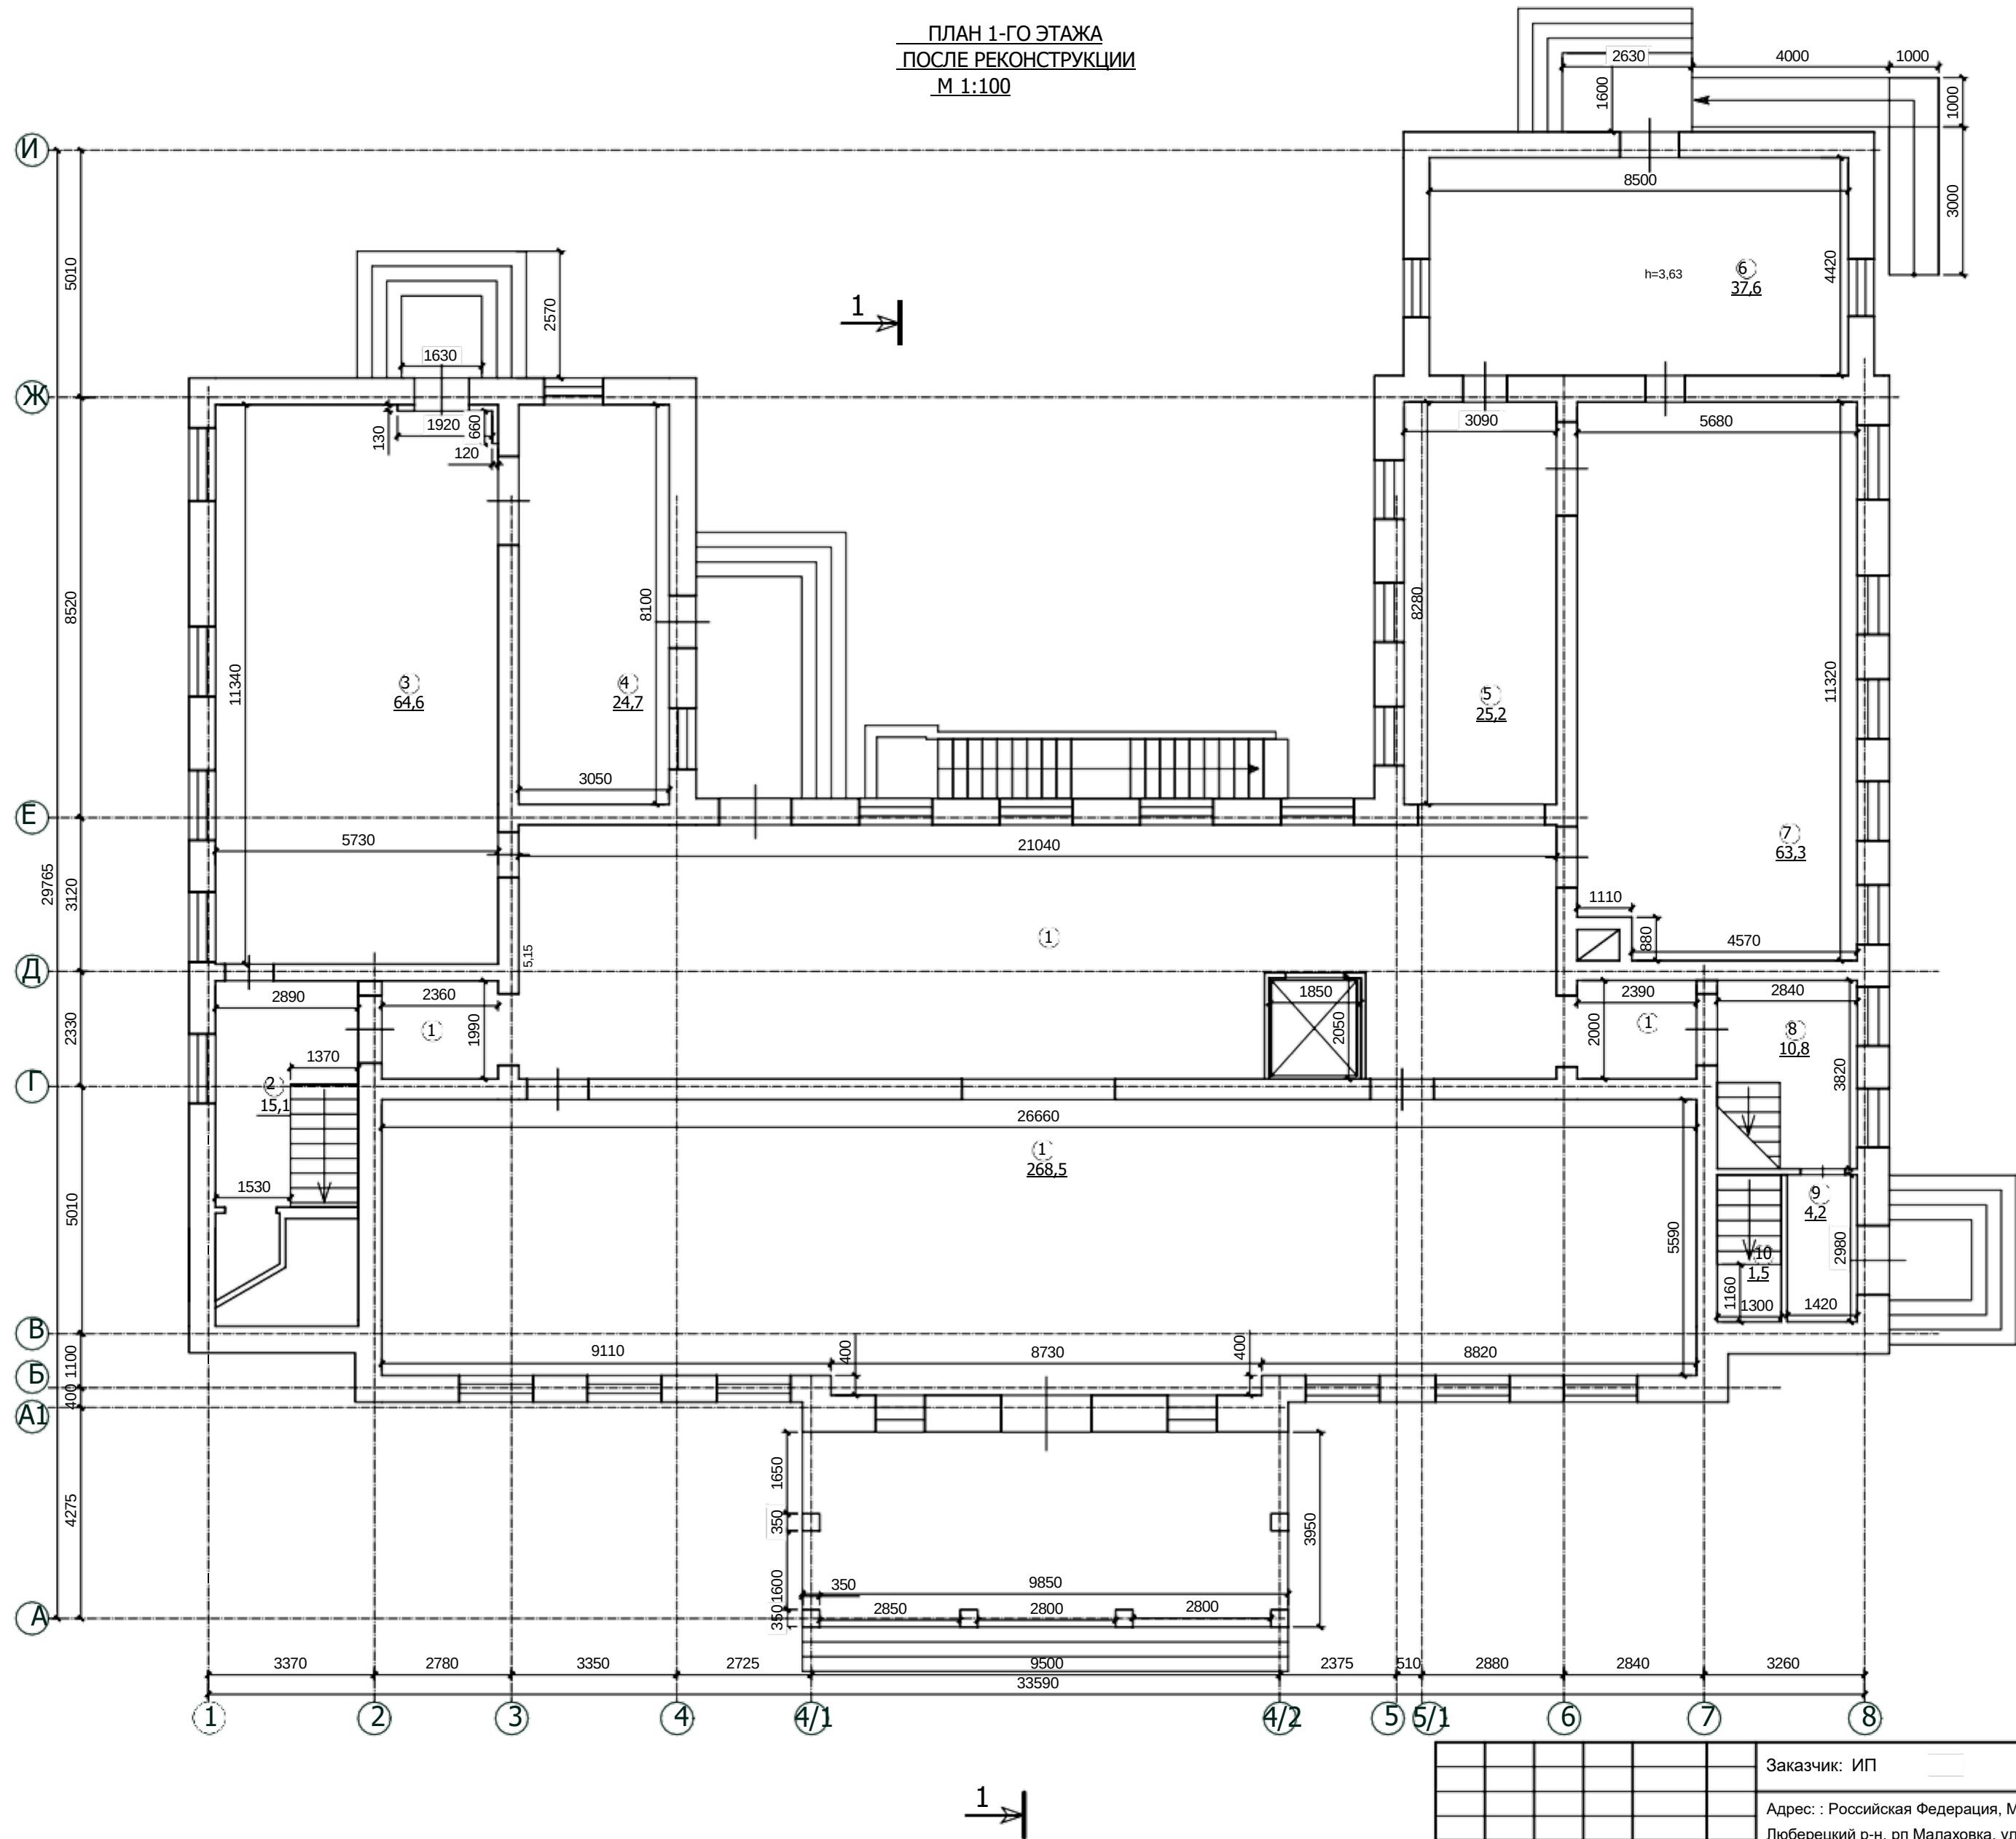

							Заказчик: ИП				Шифр: П 29/0824		
							Адрес: : Российская Федерация, Московская область, Люберецкий р-н, рп Малаховка, ул Чайковского,д1						
Изм.	Кол. уч.	Лист	№ док.	Подп.	Дата	Проект реконструкции административного здания					Стадия	Лист	Листов
Ген. дер.											П	12	
ГАП											ООО ПСК "СЕРВИС"		
ГИП													
						План 1-го этажа после реконструкции М 1:100							

ПЛАН 2-ГО ЭТАЖА
ПОСЛЕ РЕКОНСТРУКЦИИ
М 1:100

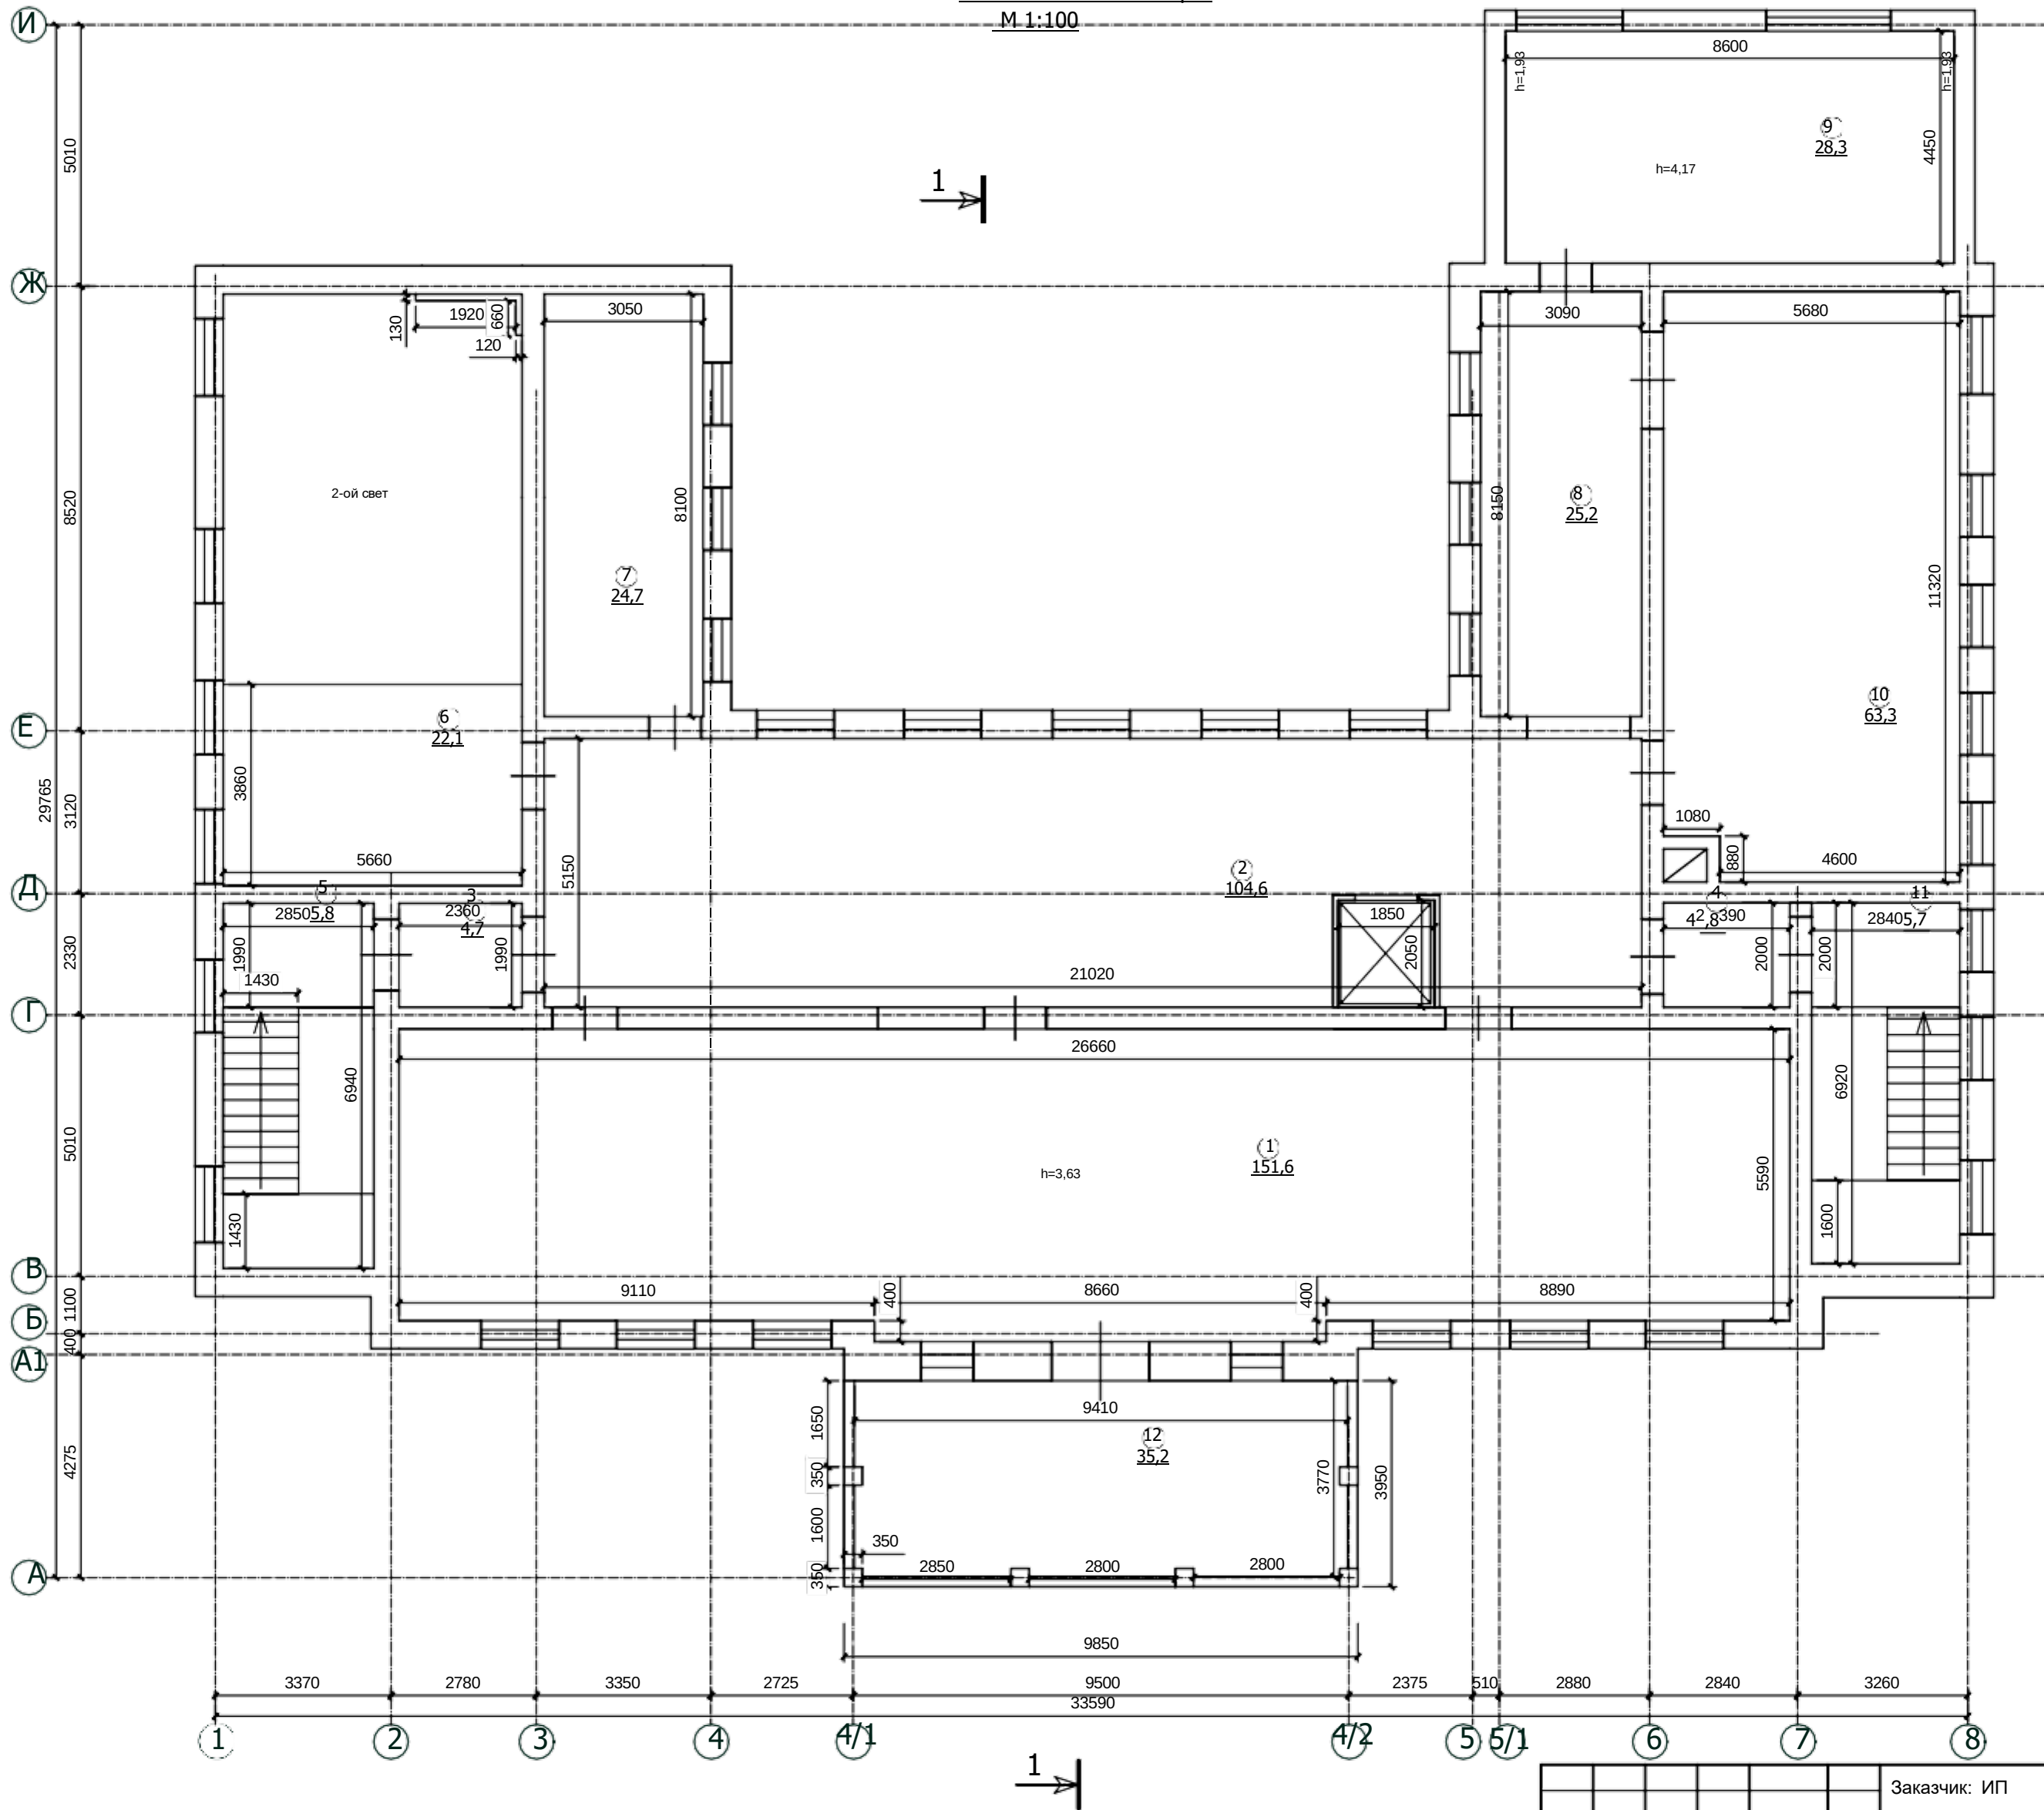

Экспликация помещений:

№ по плану	Помещение	Площадь, м2
1	Вестибюль	151,6
2	Вестибюль	104,6
3	Коридор	4,7
4	Коридор	4,8
5	Лестничная клетка	5,8
6	Помещение	22,1
7	Помещение	24,7
8	Помещение	25,2
9	Помещение	38,3
10	Помещение	63,3
11	Лестничная клетка	5,7
12	Помещение	35,2
Итого:		486,0
Общая площадь этажа		570,5


							Заказчик: ИП				Шифр: П 29/0824		
							Адрес: : Российская Федерация, Московская область, Люберецкий р-н, рп Малаховка, ул Чайковского,д1						
Изм.	Кол. уч.	Лист	№ док.	Подп.	Дата								
Ген. дер.							Проект реконструкции административного здания				Стадия	Лист	Листов
ГАП											П	13	
ГИП							План 2-го этажа после реконструкции М 1:100				ООО ПСК "СЕРВИС"		

Согласовано

И.п. ? подп. И.п. ?

Подп. и дата

ПЛАН МАНСАРДЫ
ПОСЛЕ РЕКОНСТРУКЦИИ
М 1:100

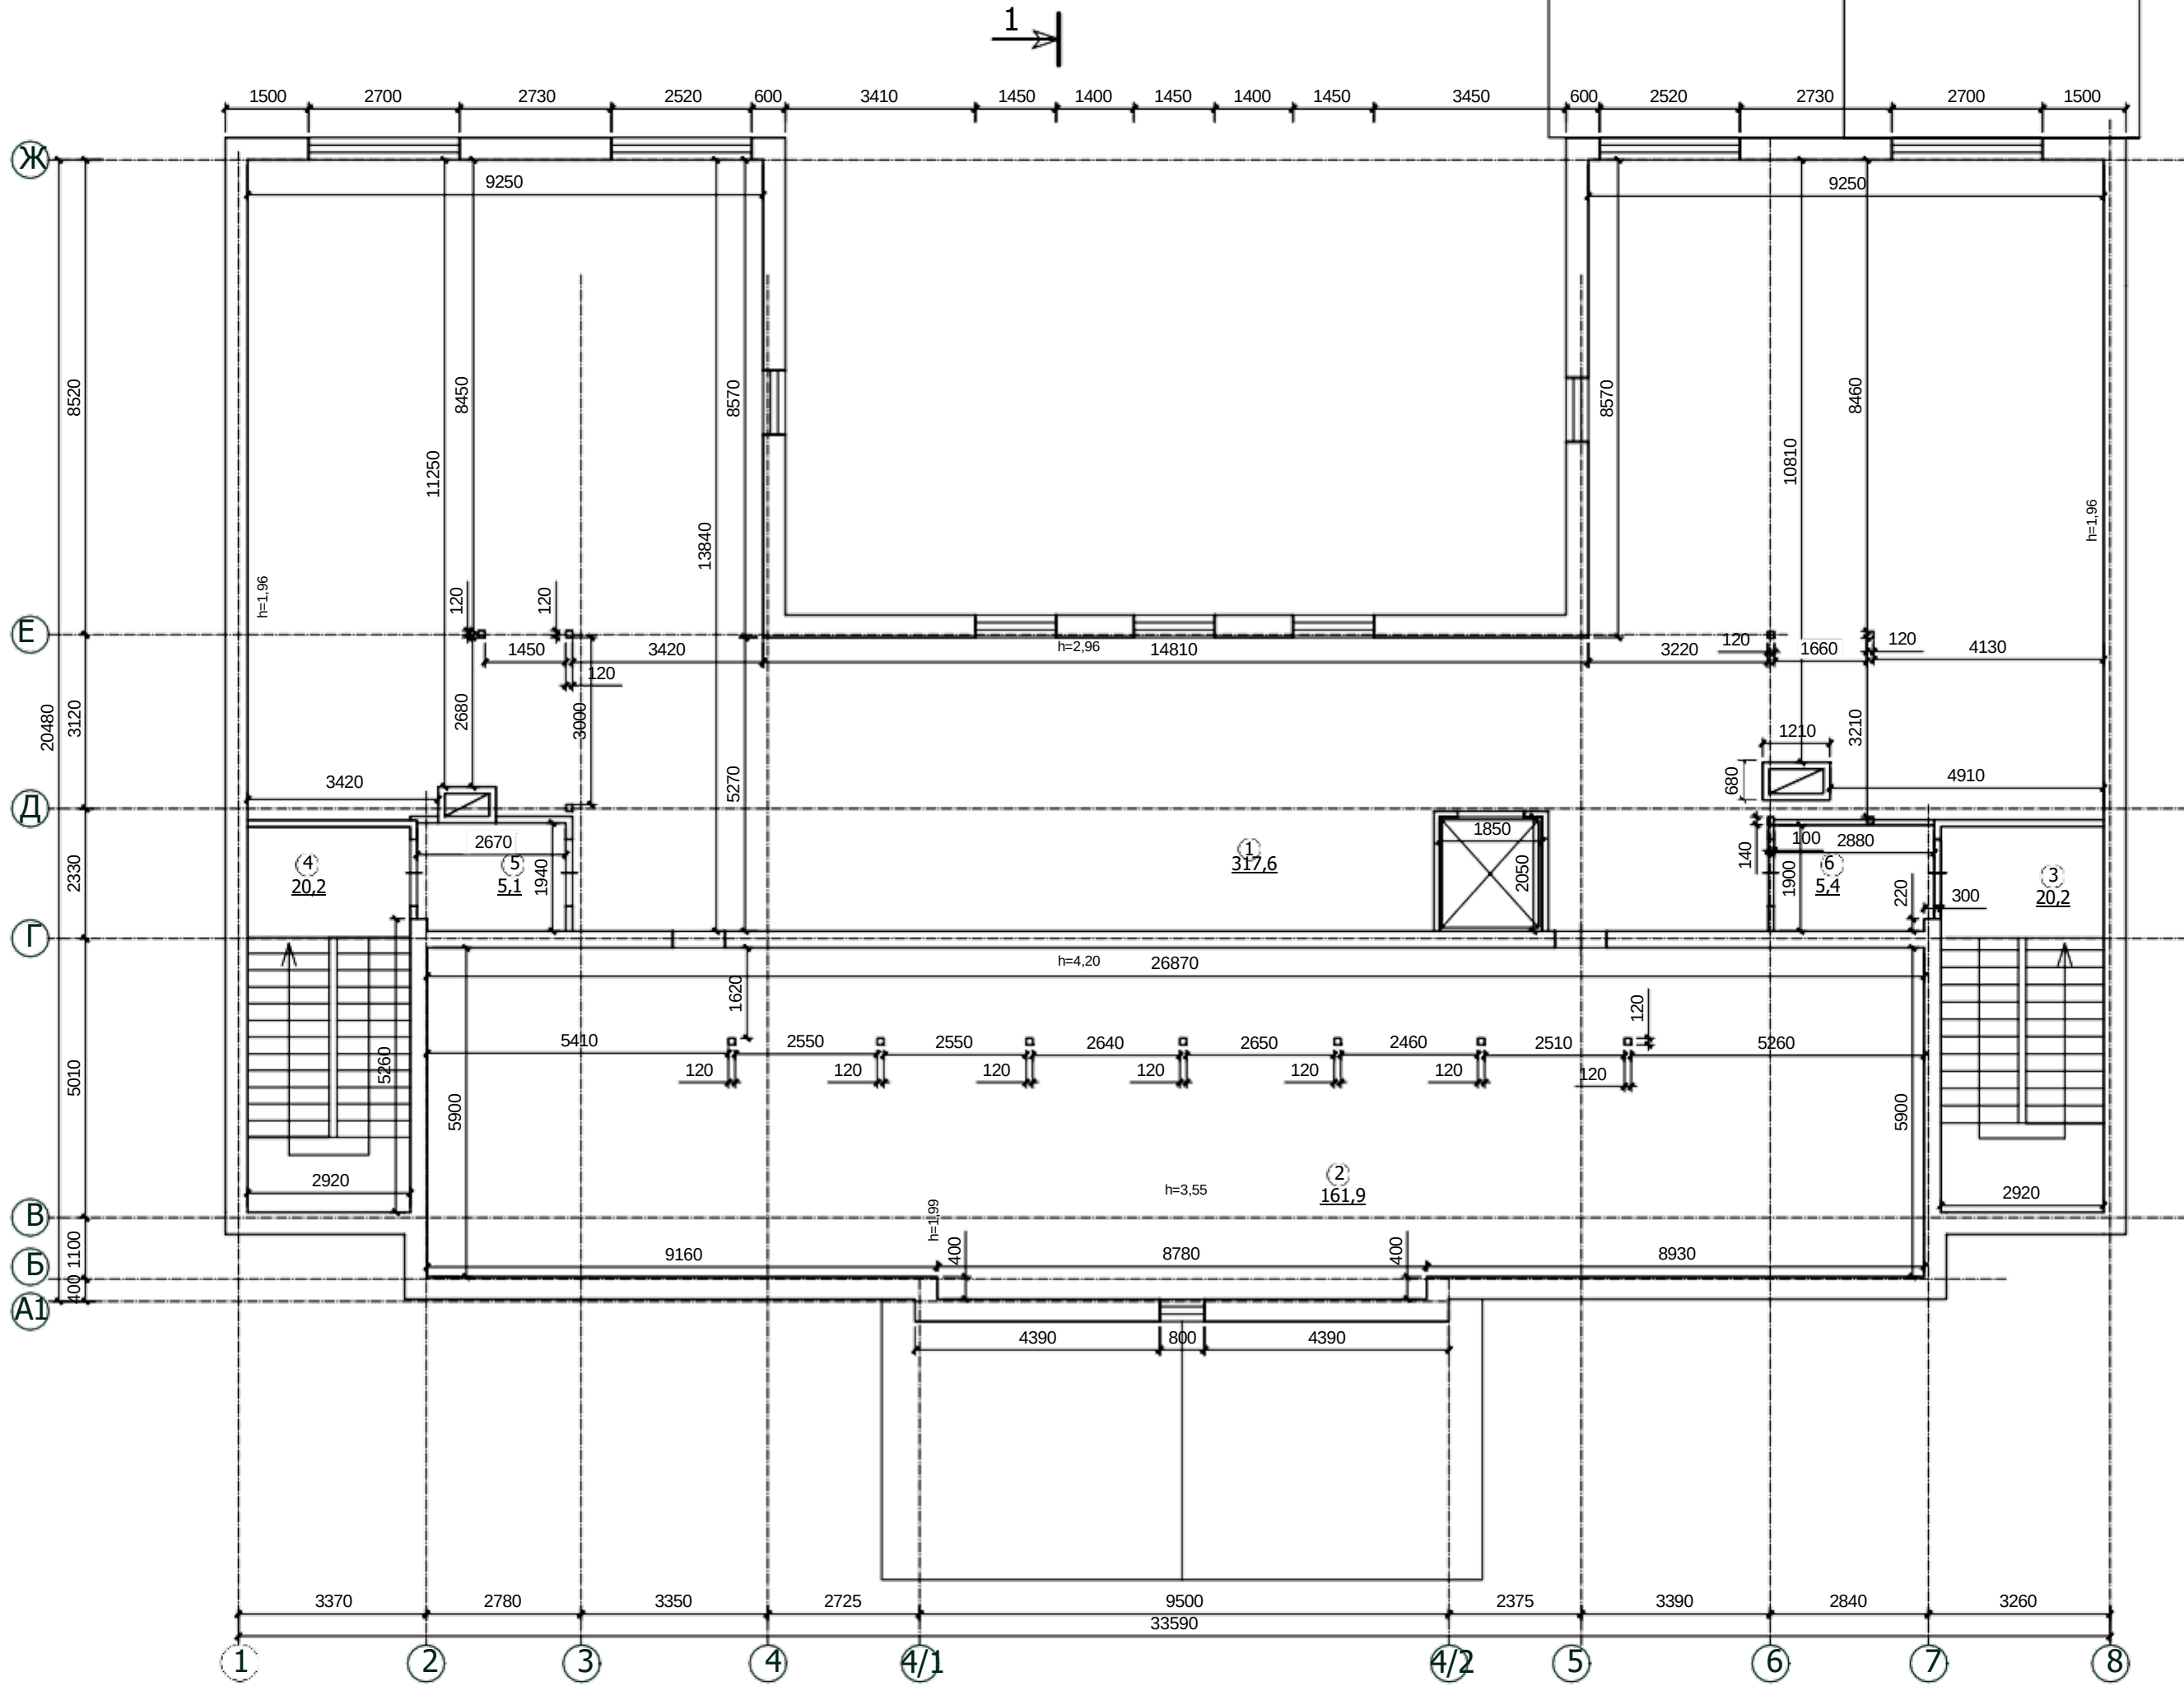

Экспликация помещений:

№ по плану	Помещение	Площадь м2
1	Помещение	307,1
2	Помещение	161,9
3	Лестничная клетка	20,2
4	Лестничная клетка	20,2
5	Коридор	5,1
6	Коридор	5,4
Итого:		519,9
Общая площадь этажа		536,6

							Заказчик: ИП				Шифр: П 29/0824		
							Адрес: : Российская Федерация, Московская область, Люберецкий р-н, рп Малаховка, ул Чайковского,д1						
Изм.	Кол. уч.	Лист	№ док.	Подп.	Дата								
Ген. дер.							Проект реконструкции административного здания				Стадия	Лист	Листов
ГАП											П	14	
ГИП							План мансарды после реконструкции М 1:100				ООО ПСК "СЕРВИС"		