


ПЛАН ПОДВАЛА ДО РЕКОНСТРУКЦИИ ПО ПЛАНУ БТИ

М 1:100

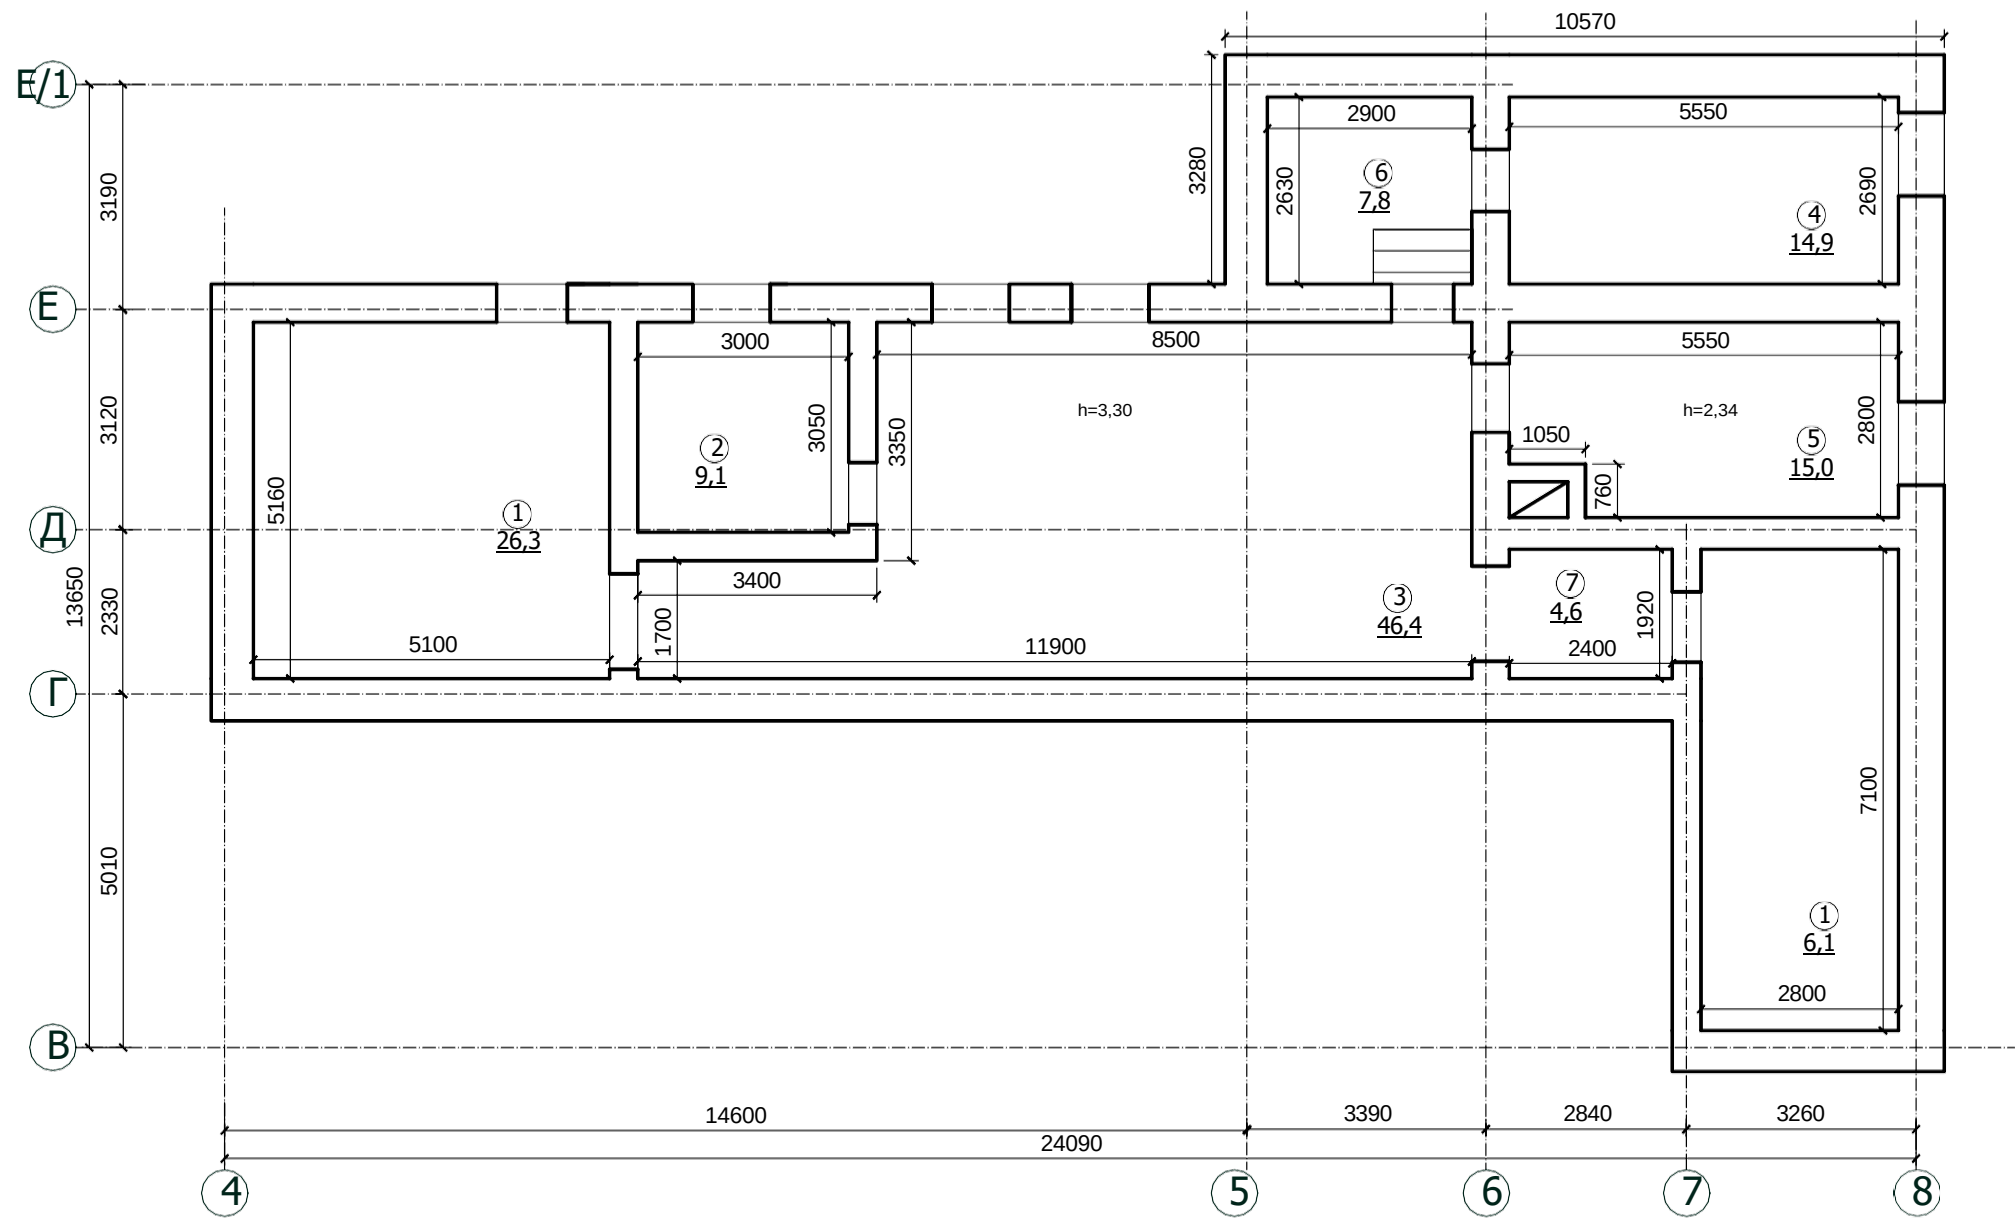

Экспликация помещений:

№ по плану		Площадь м2
1	Помещение	26,3
2	Помещение	9,1
3	Помещение	46,4
4	Помещение	14,9
5	Помещение	15,0
6	Помещение	7,8
7	Помещение	4,6
Итого:		124,1

						Заказчик: ИП							Шифр: П 29/0824																
						Адрес: : Российская Федерация, Московская область, Люберецкий р-н, рп Малаховка, ул Чайковского,д1																							
Изм.	Кол. уч.	Лист	№ док.	Подп.	Дата																								
Ген. дер.													Проект реконструкции административного здания							Стадия	Лист	Листов							
ГАП																				План подвала до реконструкции по планам БТИ М 1:100							П	2	
ГИП																											ООО ПСК "СЕРВИС"		


Копировал

А3

Согласовано
Уд. ? подп. Подп. и дата
Инб. ?


Экспликация помещений:

№ по плану		Площадь м2
1	Помещение	18,9
2	Помещение	16,8
3	Помещение	111,3
4	Помещение	50,8
5	Помещение	63,8
6	Помещение	4,7
7	Помещение	26,2
8	Помещение	27,4
9	Помещение	39,6
10	Помещение	60,3
11	Помещение	4,8
12	Помещение	49,4
13	Помещение	15,5
Итого:		489,7

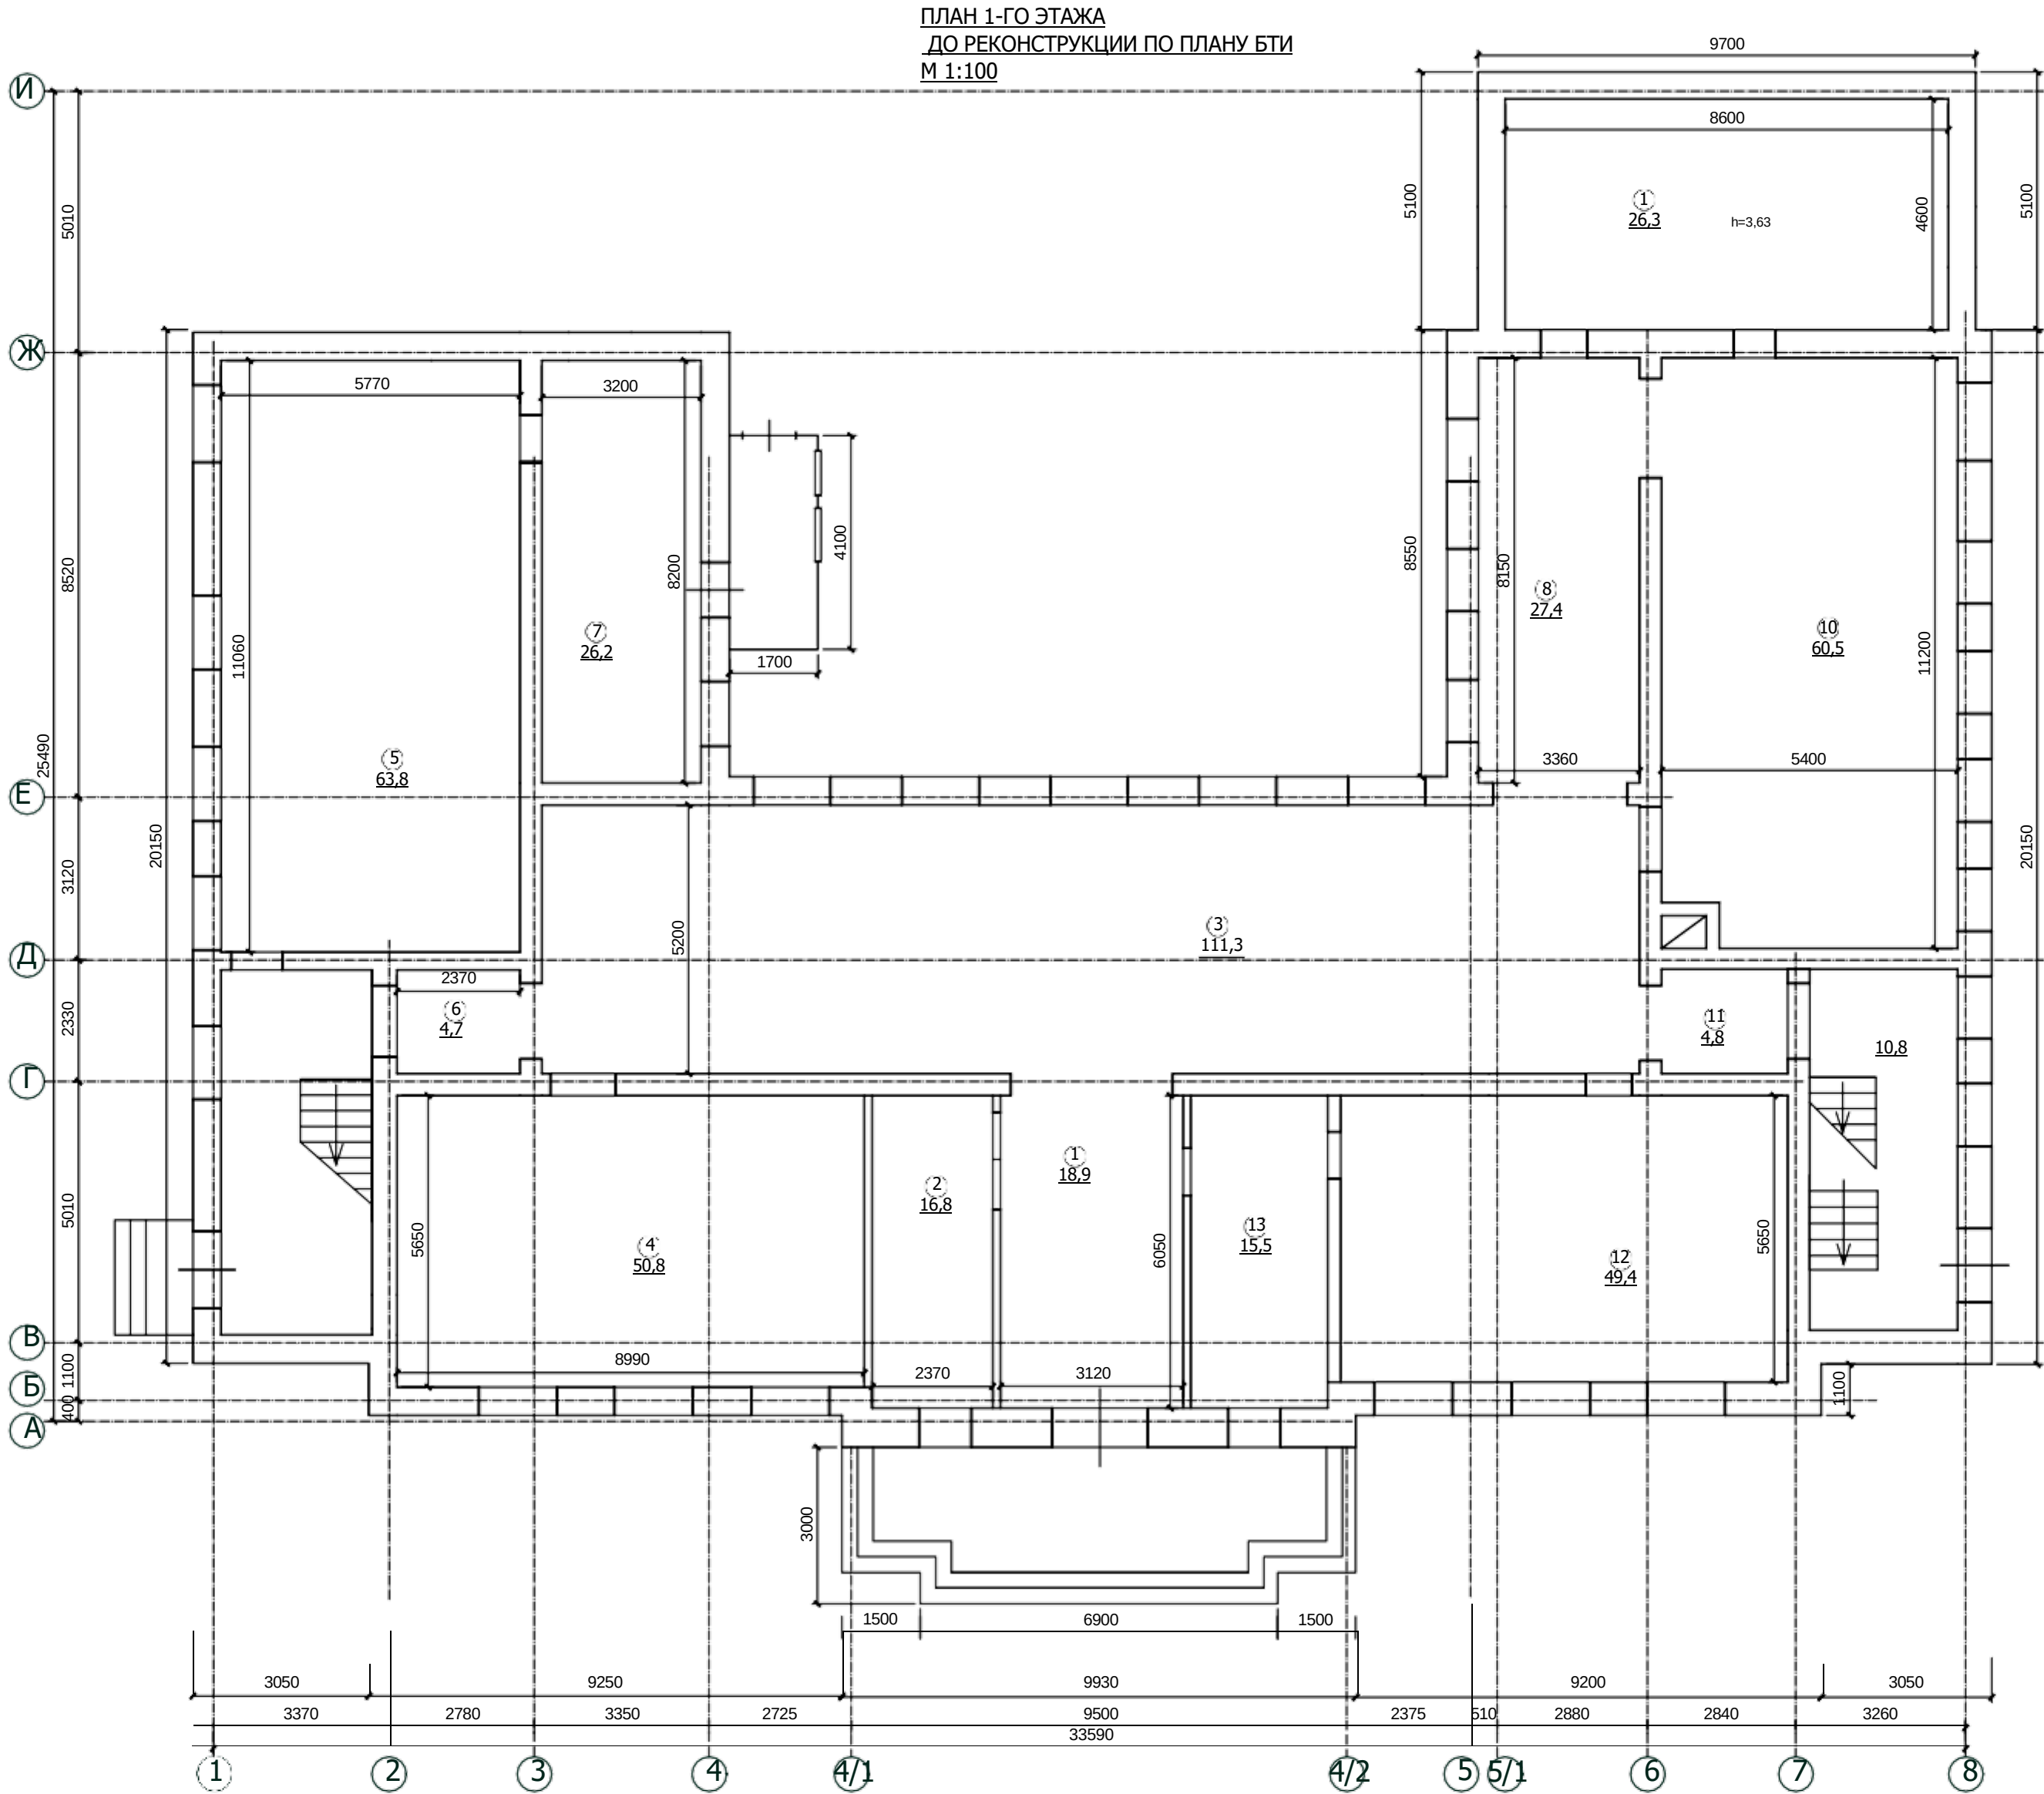

Изм.	Кол. уч.	Лист	№ док.	Подп.	Дата	Заказчик: ИП	Шифр: П 29/0824		
Ген. дер.						Адрес: : Российская Федерация, Московская область, Люберецкий р-н, рп Малаховка, ул Чайковского,д1			
ГАП						Проект реконструкции административного здания	Стадия П	Лист 3	Листов
ГИП						План 1-го этажа до реконструкции по планам БТИ М 1:100	ООО ПСК "СЕРВИС"		

ПЛАН 2-ГО ЭТАЖА
ДО РЕКОНСТРУКЦИИ ПО ПЛАНУ БТИ
М 1:100

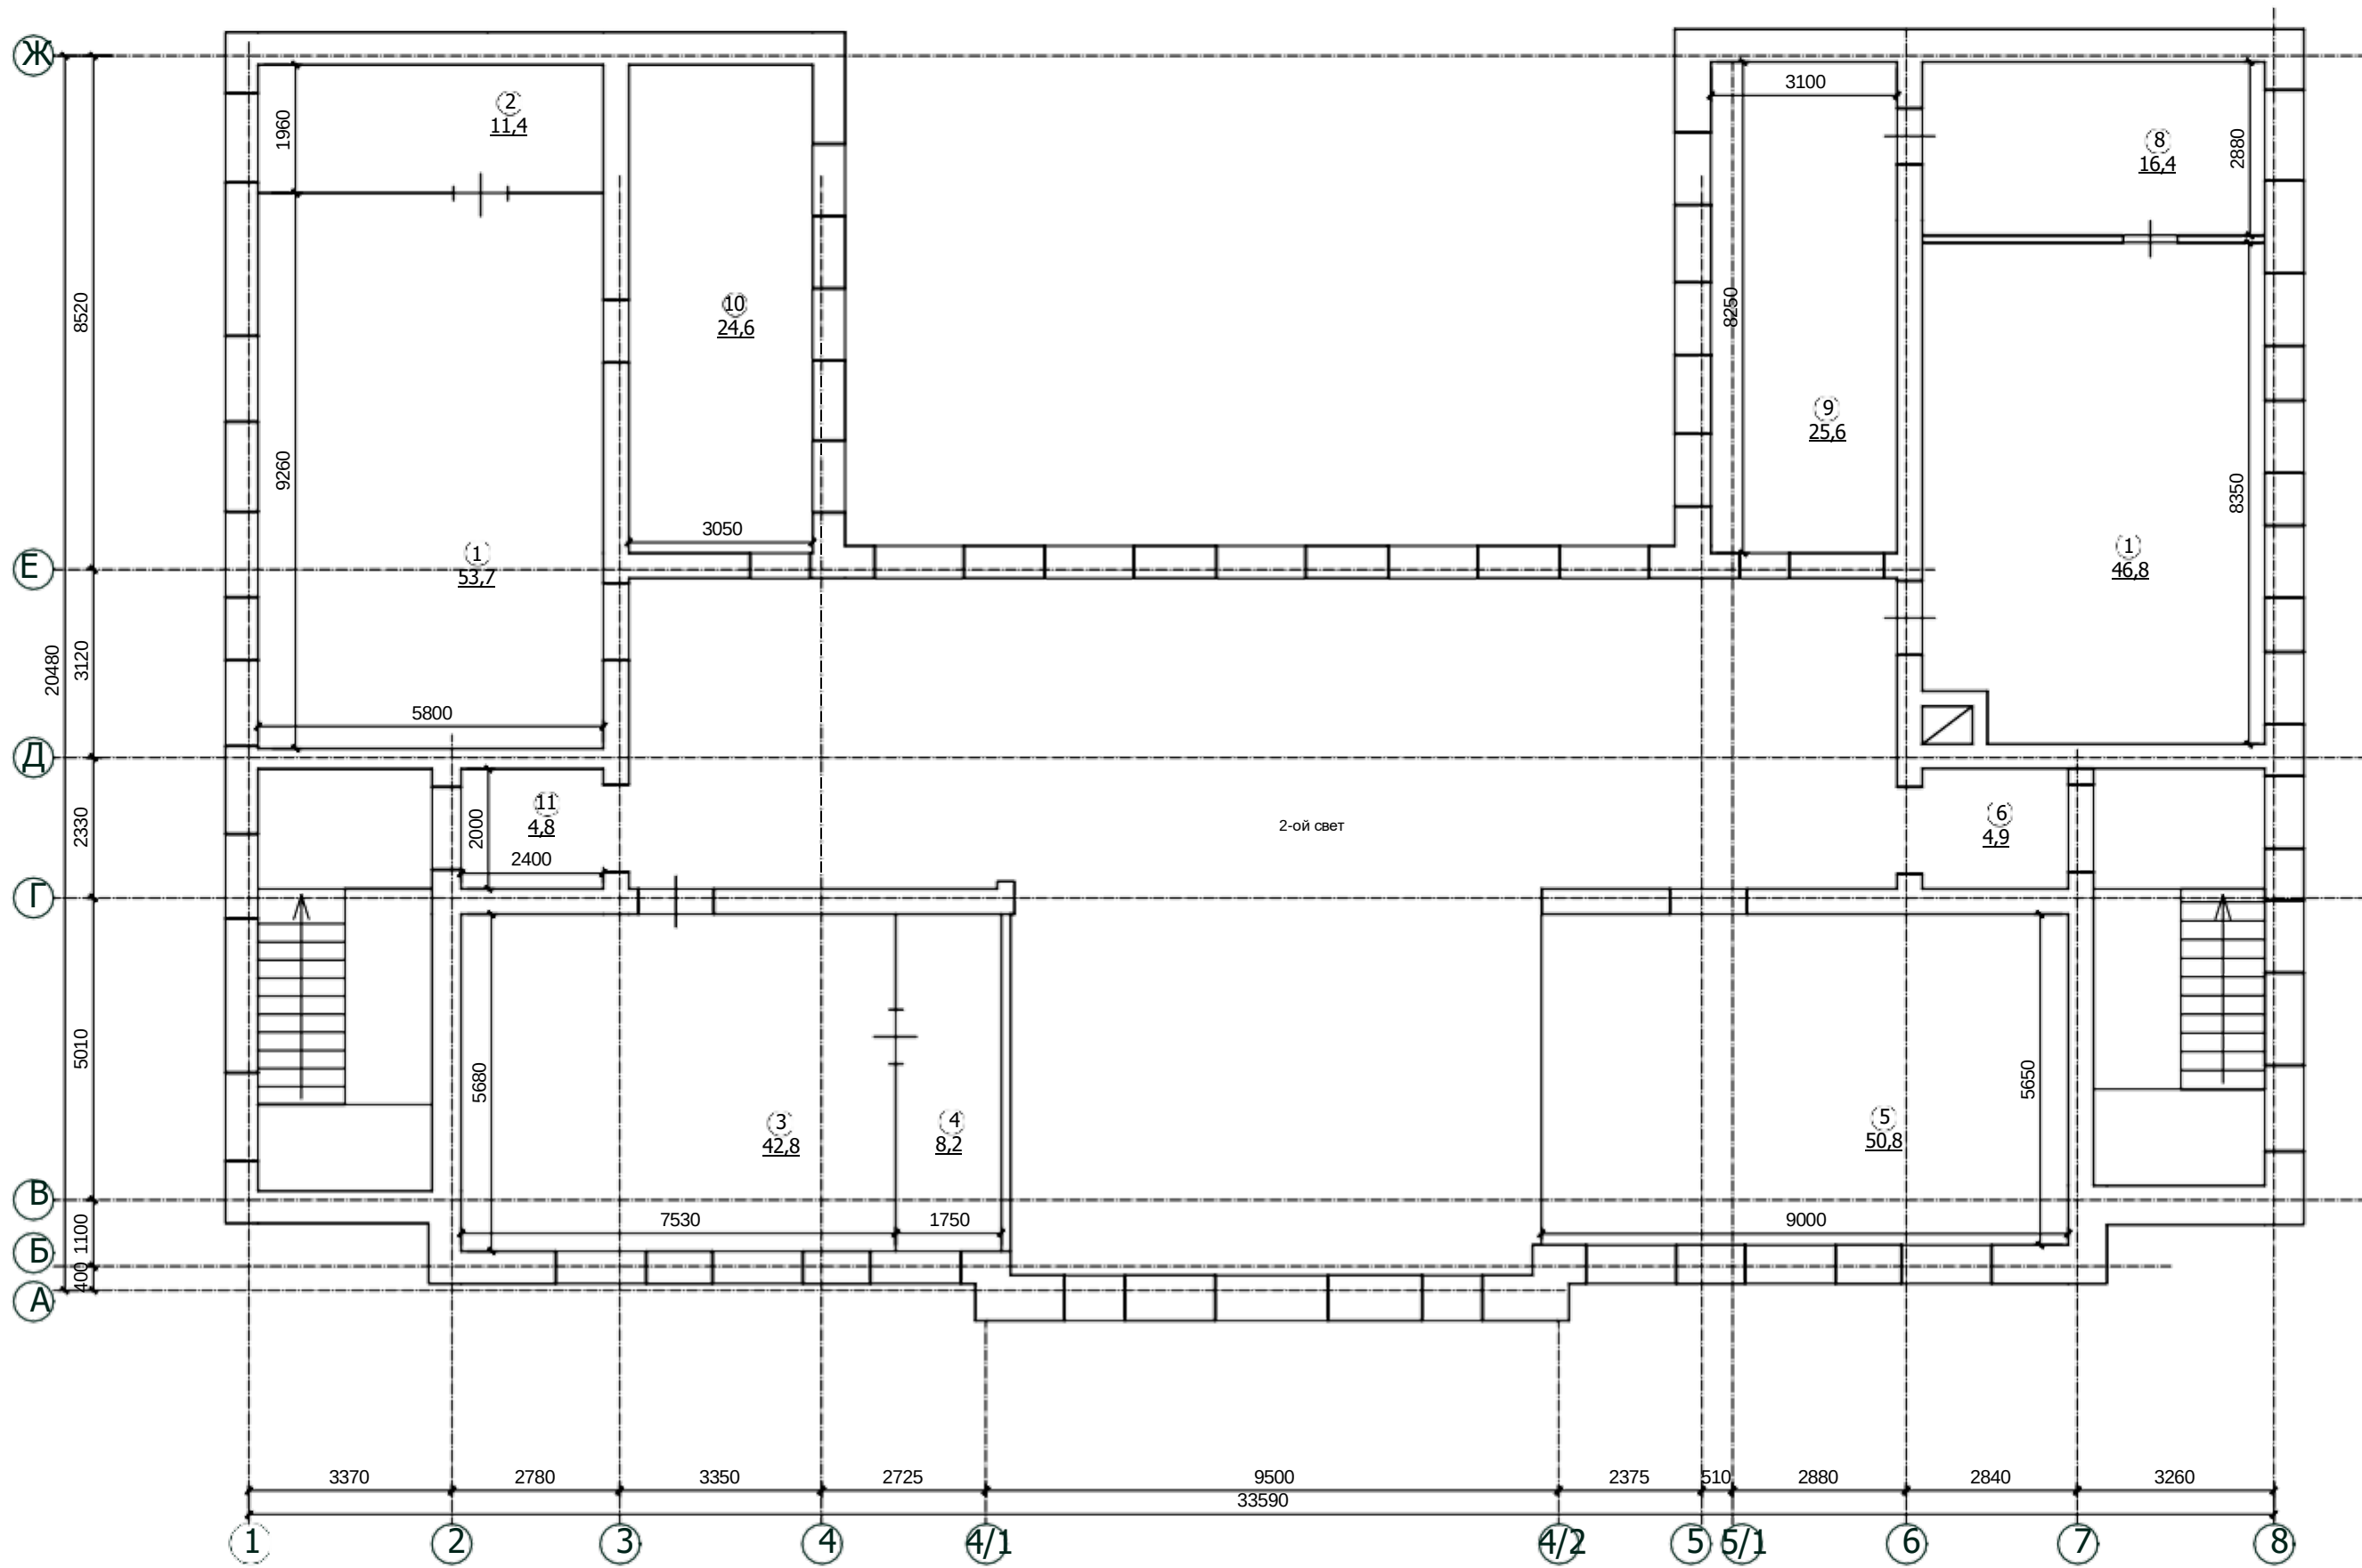

Экспликация помещений:

№ по плану	Помещение	Площадь м2
1	Помещение	53,0
2	Помещение	11,4
3	Помещение	42,0
4	Помещение	8,2
5	Помещение	50,8
6	Помещение	4,9
7	Помещение	46,8
8	Помещение	16,4
9	Помещение	25,6
10	Помещение	24,6
11	Помещение	4,8
Итого:		290,0

						Заказчик: ИП _____ Шифр: П 29/0824					
						Адрес: : Российская Федерация, Московская область, Люберецкий р-н, рп Малаховка, ул Чайковского,д1					
Изм.	Кол. уч.	Лист	№ док.	Подп.	Дата						
Ген. дер.						Проект реконструкции административного здания			Стадия	Лист	Листов
ГАП									П	4	
ГИП						План 2-го этажа до реконструкции по планам БТИ М 1:100			ООО ПСК "СЕРВИС"		